ORIGINAL.

27
(1)

LAKE GEORGE SUMMER RESORT.
CLARE CO. MICH.

Examined and Approved
Nov 11-1915

Dedication.

Know All Men By These Presents, That we James Duncan as Proprietor and Anna Duncan his wife, have caused The Land embraced in The annexed Plat To be surveyed, Laid out and Platted, To be known as Lake George Summer Resort Clare Co. Michigan and That The streets and alleys as shown on said Plat are hereby dedicated To The use of The Public.

Signed and Sealed in Presence of
Benj. J. Lewis
Arthur D. Johnson

James Duncan (LS)
Anna Duncan (LS)

State of Michigan, }
County of Clare. } ss.

On This 28 day of October 1915 before me, a Justice of The Peace for said County, Personally came The above named James Duncan and Anna Duncan his wife, Known To me To be The Persons who executed The above dedication, and acknowledged The same To be Their Free act and deed. Charles A. Thurston Justice of the Peace
Justice of The Peace, Clare Co. Michigan.
My commission expires ____________________

Surveyor's Certificate.

I hereby certify That The Plat hereon delineated is a correct one, and That Permanent monuments, consisting of 2 inch Gaspipe 24 To 30 inches Long, have been Planted at Points marked Thus ∘ as Thereon shown at all angles in The boundaries of The Land Platted, and at all intersections of streets or streets and alleys.

Arthur D. Johnson.
Surveyor.

Certificate of Municipal Approval.

This Plat was approved By The Township Board of The Township of Lincoln, at a meeting held October 5 1915.
[illegible] Clerk.

Certificate of approval by County Board.

This Plat was approved on The 27th day of October 1915.

Arthur Long
Judge of Probate.
Francis M. Morrissey
County Clerk.
Peter A. Oman
County Treasurer.

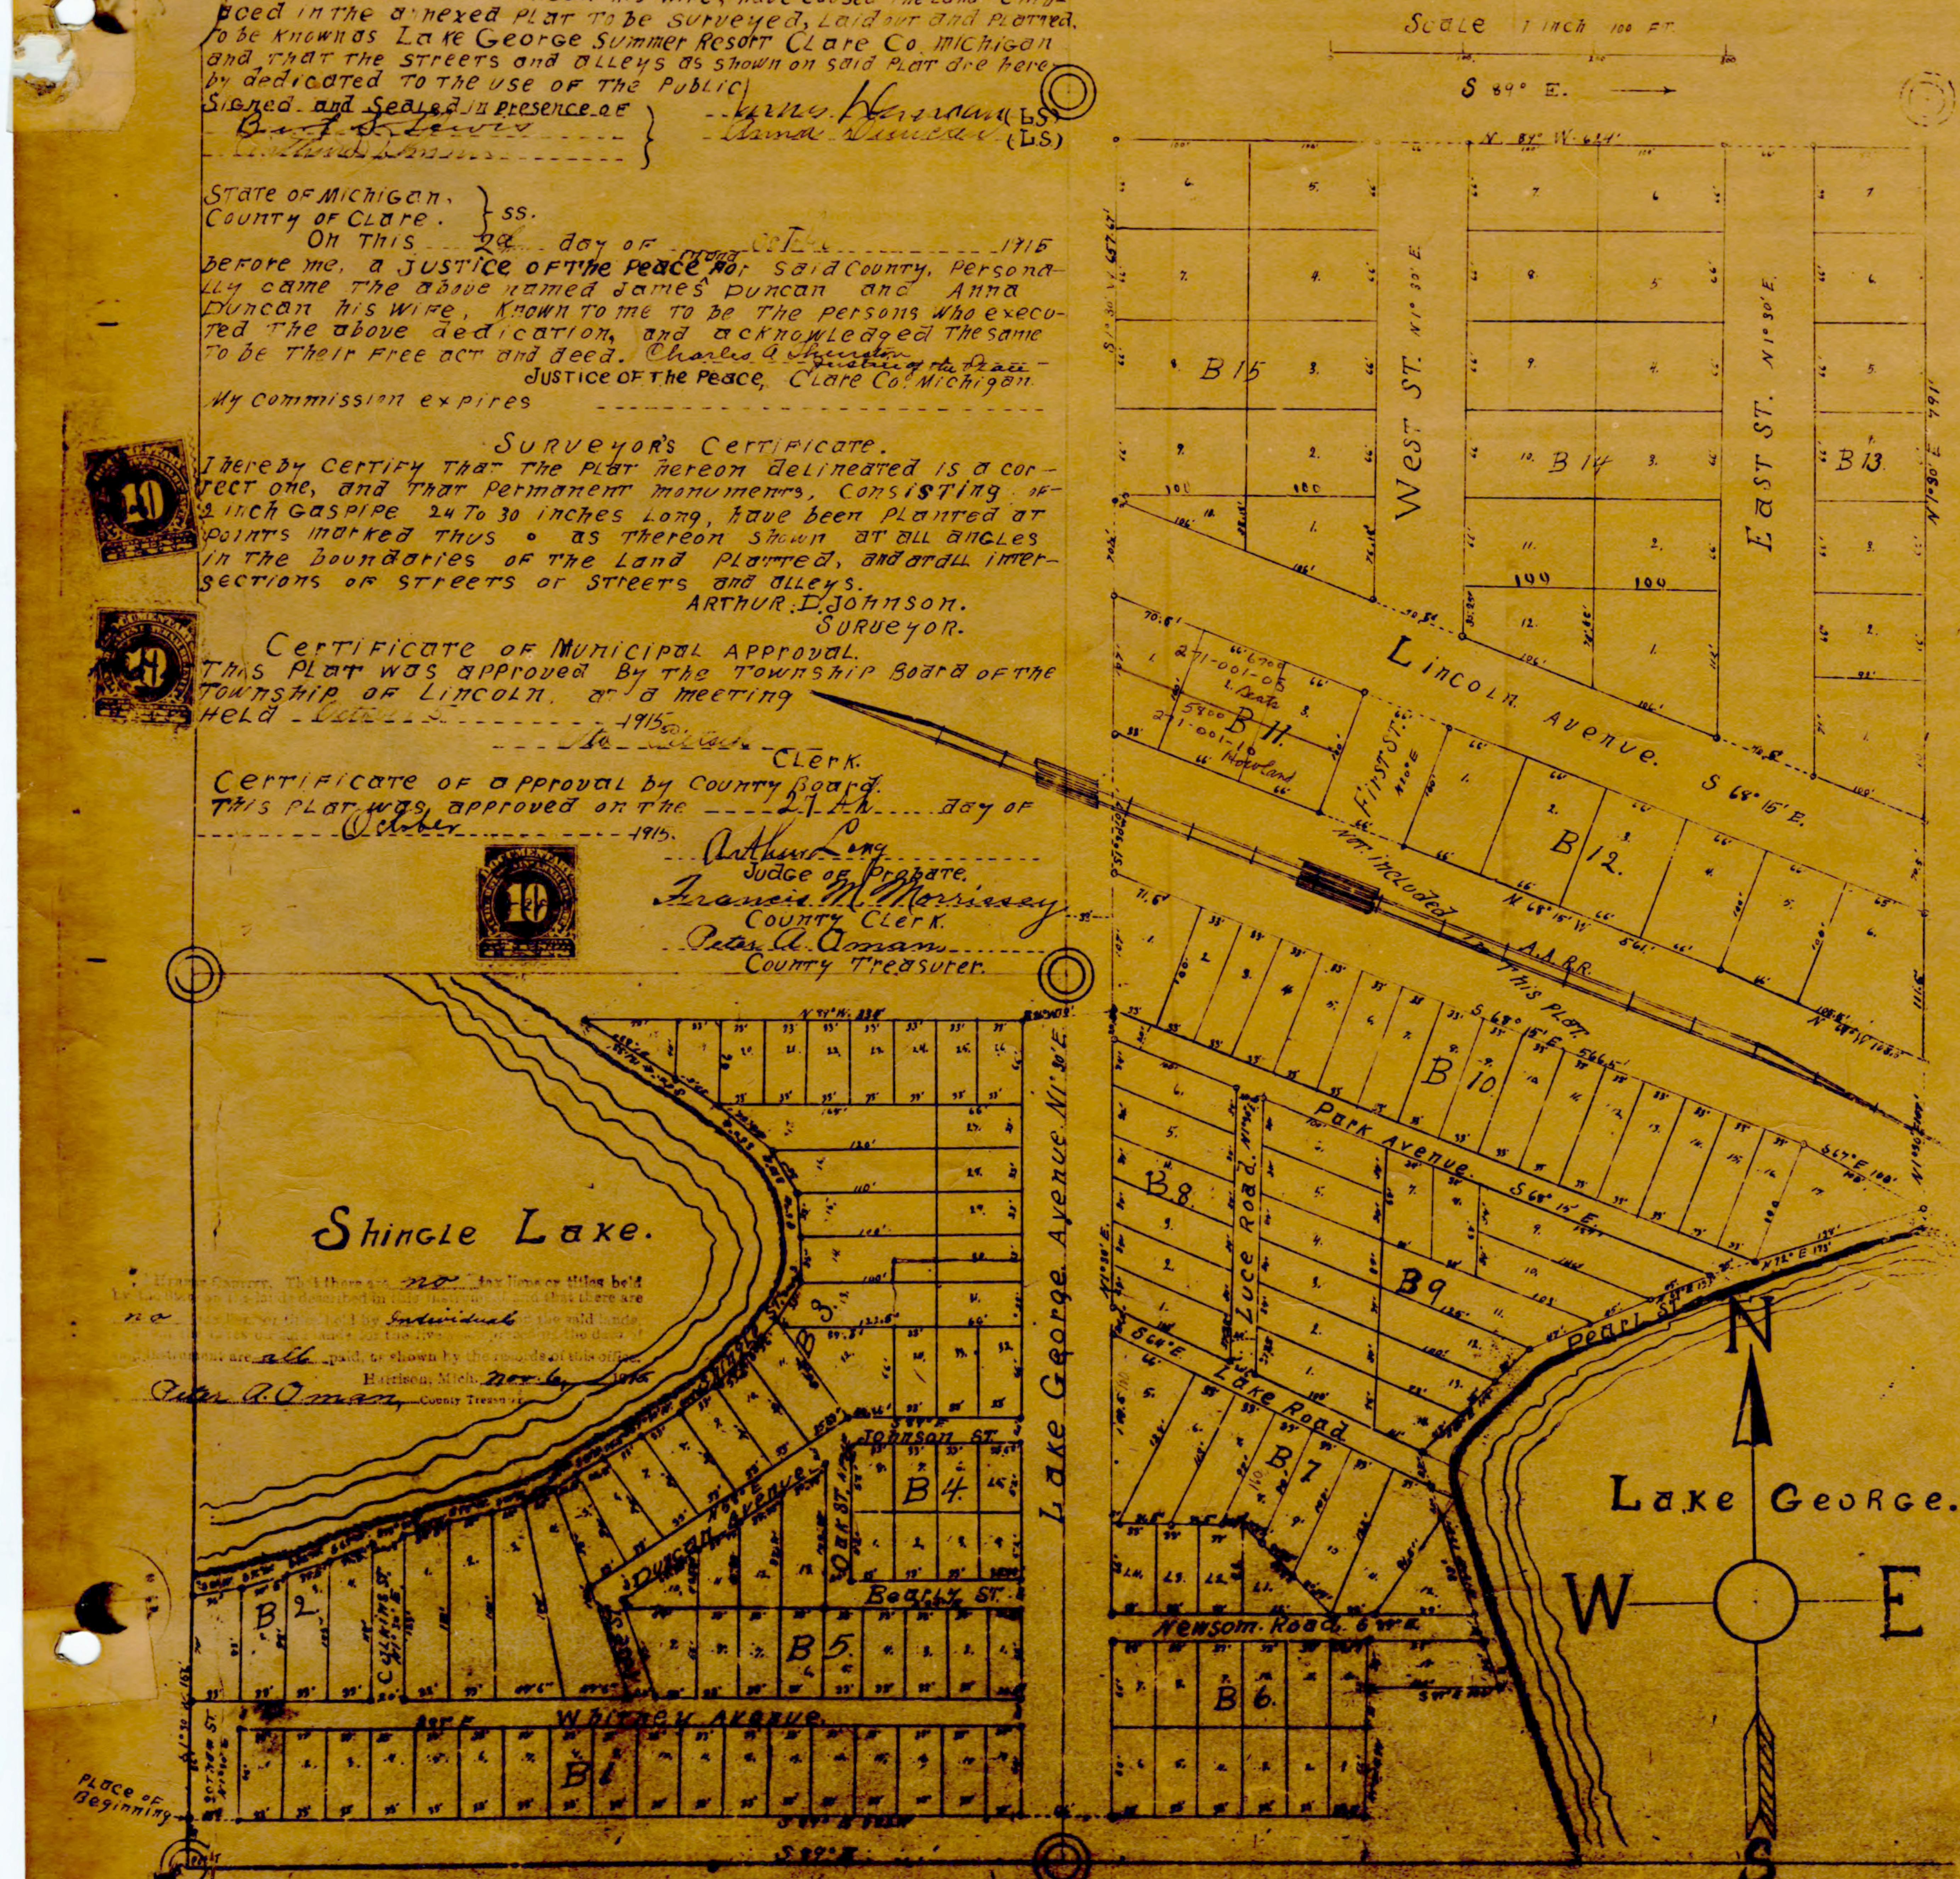

[illegible] County. That there are no tax liens or titles held by the State on the lands described in this instrument, and that there are no tax liens or titles held by individuals on the said lands, [illegible] the taxes on said lands for the five years preceding the date of said instrument are all paid, as shown by the records of this office.
Harrison, Mich. Nov. 6 [illegible]
Peter A. Oman, County Treasurer

Description of Land Platted. Part of The N.W.¼ of S.W.¼ of Section 8. T. 18. N. R. 5 W.

The Land embraced in The annexed Plat of Lake George Summer Resort Clare County Michigan. Is described as follows. Beginning at a Point 33 Feet North of ¼ Post at The S.W. Corner of The N.W.¼ of S.W.¼ of Section 8. T. 18. N. R. 5 W. (Lincoln Twp.) Clare County Michigan. Proceeding Thence S. 89° E 888.17 Feet. Thence N. 1° 30' E 99 Feet Thence S. 89° E 100 Feet. Thence N. 18° W. 118 Feet. Thence N. 15° E 118 Feet. Thence N 67° E 137 Feet. Thence N. 72° E 113 Feet. Thence N. 1° 30' E. 791 Feet. Thence N. 89° W 624 Feet. Thence S 1° 30' W 657.67 Feet. Thence S. 86° W 70 Feet. Thence N 89° W. 334 Feet Thence S 55° E 121.33 Feet Thence S 60° E 55.66 Feet. Thence S. 88° E 35 Feet. Thence S 5° E 33 Feet. Thence S. 35 Feet. Thence S 40° W. 33 Feet. Thence S. 44° W. 36 Feet. Thence S. 45° W 33.5 Feet. Thence S. 54° W. 38 Feet. Thence S. 57° 30' W 33 Feet. Thence S. 60° W 55.5 Feet. Thence S. 53° W. 22.5 Feet. Thence S. 68° W. 25 Feet. Thence S. 80° W. 25 Feet. Thence S. 78° W 36 Feet. Thence S. 73° W. 33.5 Feet. Thence S. 73° 30' W. 20.5 Feet. Thence S. 69° W. 35.5 Feet. Thence S. 72° W. 35.5 Feet. Thence S. 76° W 34.5 Feet. Thence S 80° W. 36 Feet. Thence S. 1° 30' W. 156 Feet. To Place of beginning. Excepting R.R. Right of way. which is not included in This Plat, and is described as follows.

Beginning at The N.W. Corner of Lot 1. Block 10. Proceeding Thence S 68° 15' E 566.5 Feet. Thence S 67° E 100 Feet. Thence N. 1° 30' E 107 Feet. Thence N. 67° W. 105.5 Feet Thence N 68° 15' W. 561 Feet. Thence S. 1° 30' W 107. Feet. To Place of beginning.

All dimensions are given in Feet and decimals Thereof.

STATE OF MICHIGAN, }
COUNTY OF CLARE } ss.

This instrument was presented and received for record this 19th day of November A. D. 1915 at 9 o'clock a. m. and recorded in liber One of ______ on page 27 as a proper certificate was furnished in compliance with Section 3957, Compiled Laws of 1897.

Francis M. Morrissey
Register of Deeds