Examined and Approved
Dec 9-1920
Deputy Auditor General

Original.

MAP OF "LINCOLN RESORT."

A subdivision of Part of Lot 2 Section 16 T 18 N R 6 W Clare Co Michigan.

Description of land platted.

The land embraced in the annexed plat of "Lincoln Resort." A subdivision of Part of Lot 2 Section 16 T 18 N. R. 6 W Clare Co. Michigan is described as follows. Comencing at a point 116 feet W. of S. E. Cor of Lot 2 Section 16 T. 18. N. R. 6 W. Clare Co. Michigan. Proceeding thence N. 48° 30' W 1663 feet thence S 1° W. 103 feet to high water line on the east shore of Lake George. Thence in a south easterly course along the highwater line 1503 feet thence East 297 feet to place of beginning.

Certificate of Municipal Approval.

This plat was approved by the Township Board of the Township of Lincoln Clare Co Michigan. at a meeting held

July ... 1920
(Date)

Elizabeth Bixby
Clerk.

Certificate of Co. Board approval.

This plat was approved by the Co. Board of the Co. of Clare State of Michigan at a meeting held

July 28, 1920.
(Date)

Thomas J. Dorsey Judge of Probate
Emma Hoy Deputy Co Clerk
Co Treasurer.

Surveyors Certificate.

I hereby certify that the plat hereon delineated is a correct one, and that permenent monuments, consisting of 3/4 inch gaspipe from 24 to 30 inches long, have been planted at points marked thus (°) as thereon shown at all angles in the boundaries of the land platted, and at all intersections of streets or streets and alleys.

Arthur D Johnson
Registered Surveyor.

I HEREBY CERTIFY that there are No tax liens or titles held by the State on the lands described in this instrument and that there are No tax liens or titles held by individuals on the said lands, and that the taxes on said lands for the five years preceding the date of said instrument are all paid as shown by the records of this office.

Harrison, Mich. Aug 3. 1920

Elmer E. Clute
County Treasurer

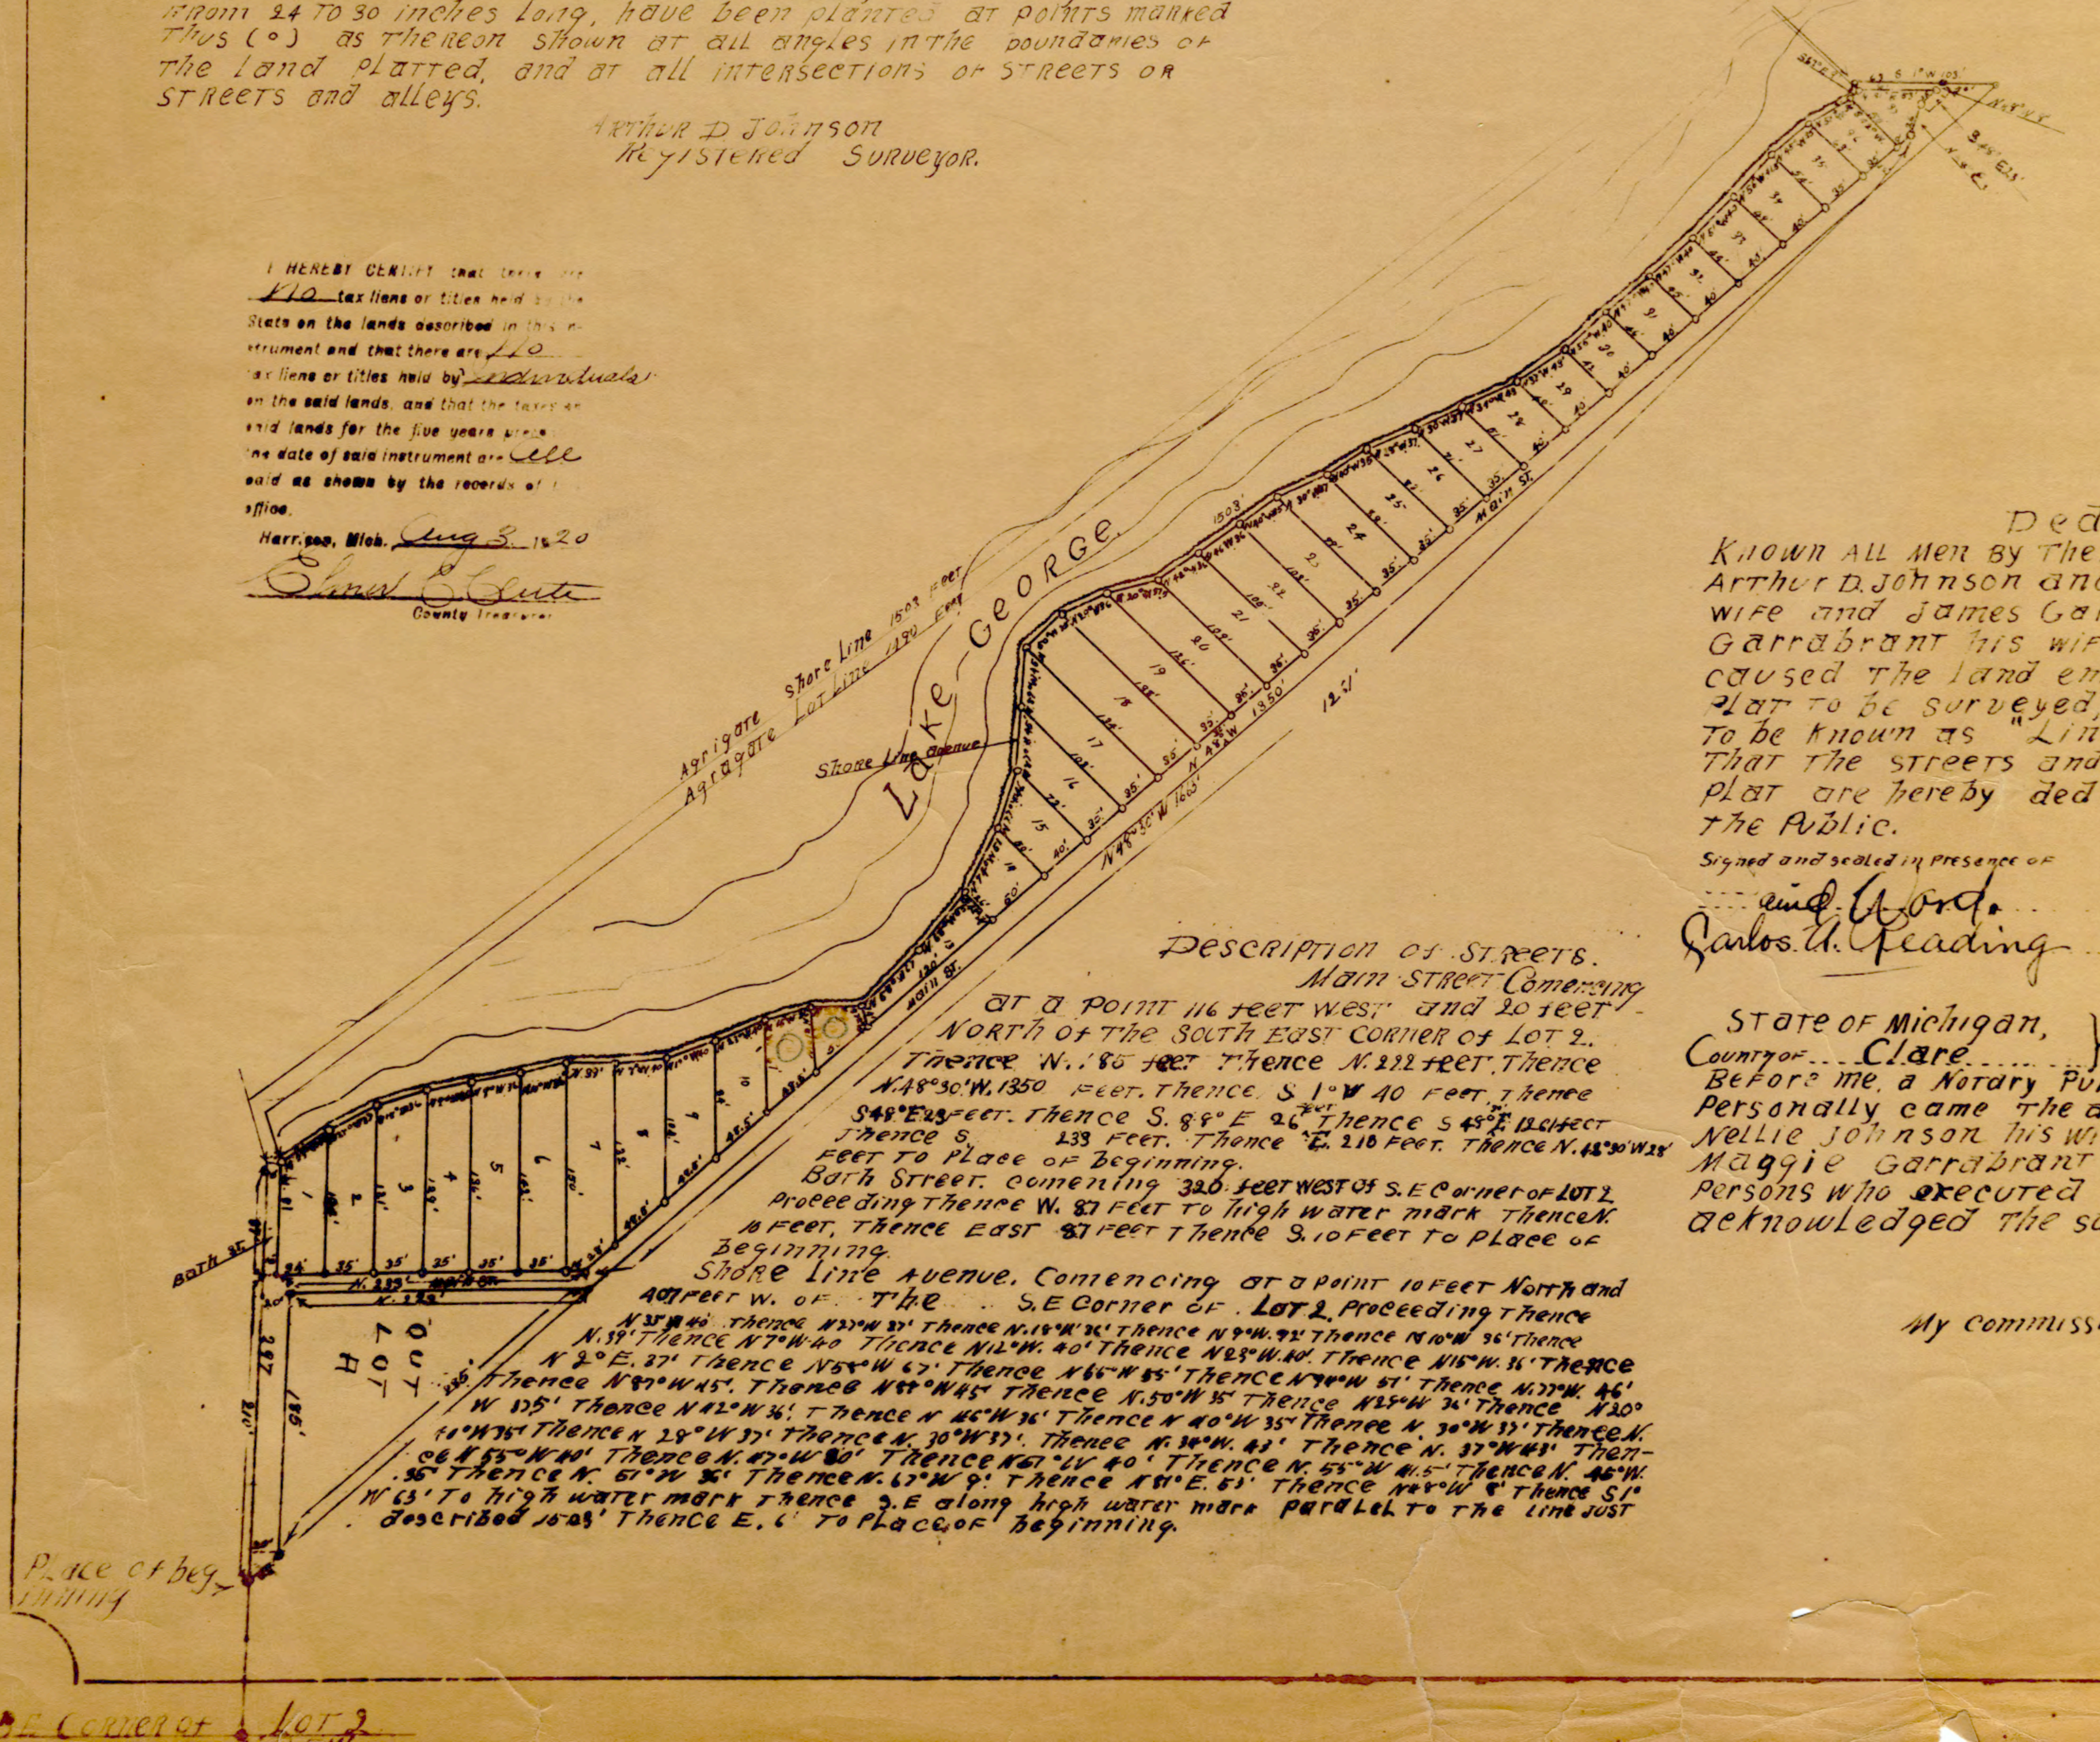

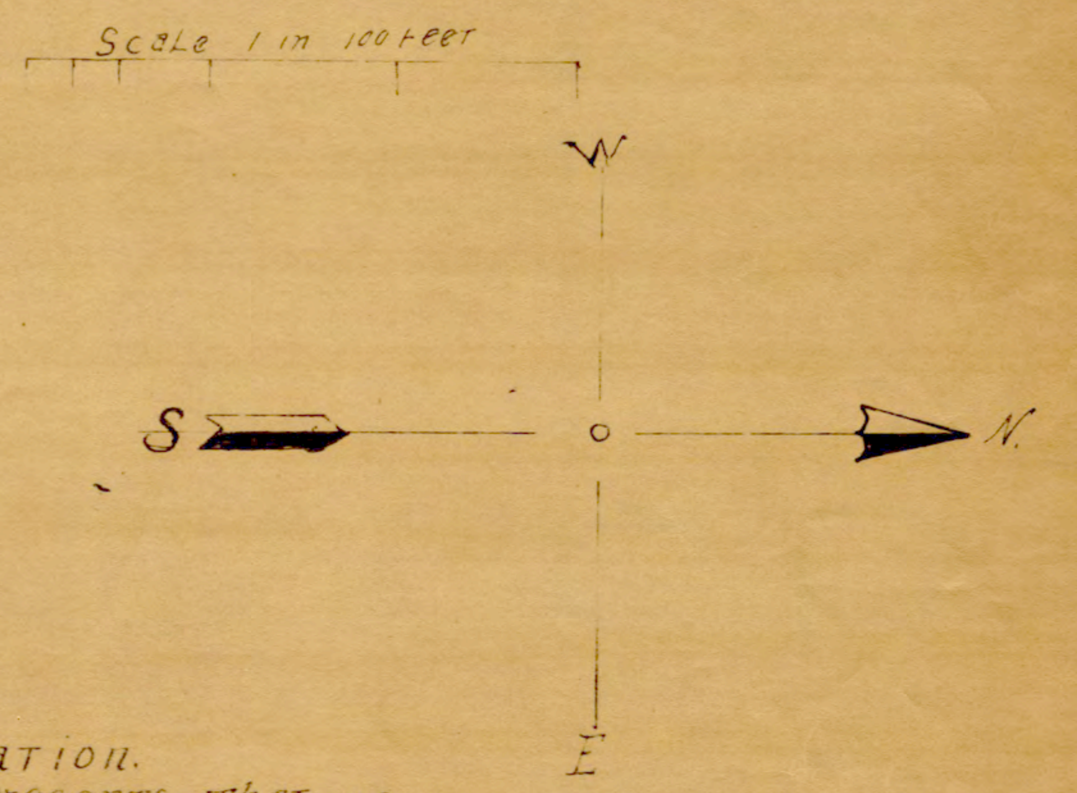

Dedication.

Known all men by these presents, that we Arthur D. Johnson and Nellie Johnson his wife and James Garrabrant and Maggie Garrabrant his wife, Proprietors, have caused the land embraced in the annexed plat to be surveyed, laid out and platted to be known as "Lincoln Resort", a subdivision of part of Lot 2 Section 16 T 18 N. R. 6 W. Clare Co. and that the streets and alleys as shown on said plat are hereby dedicated to the use of the public.

Signed and sealed in presence of

Emil A. Word.
Carlos U. Reading

Arthur D. Johnson [L.S.]
Nellie Johnson [L.S.]
James Garrabrant [L.S.]
Maggie Garrabrant [L.S.]

State of Michigan,
County of Clare } ss.

On this 17 day of July 1920 before me, a Notary Public in and for said County, personally came the above named Arthur D. Johnson and Nellie Johnson his wife and James Garrabrant and Maggie Garrabrant his wife, known to me to be the persons who executed the above dedication and acknowledged the same to be their free act and deed.

Carlos U. Reading,
Notary Public Clare Co. Mich.
My commission expires December 4th 1923.

Description of Streets.

Main Street Comencing at a point 116 feet west and 20 feet north of the South East corner of Lot 2. Thence N. 185 feet Thence N. 222 feet. Thence N. 48° 30' W. 1350 feet. Thence S 1° W 40 feet. Thence S 48° E 23 feet. Thence S. 88° E 26 feet Thence S 48° E 1261 feet Thence S. 233 feet. Thence E. 210 feet. Thence N. 48° 30' W 28 feet to place of beginning.

Bath Street. Comening 320 feet west of S. E Corner of Lot 2 proceeding thence W. 87 feet to high water mark thence N. 10 feet, thence East 87 feet thence S. 10 feet to place of beginning.

Shore line Avenue. Comencing at a point 10 feet North and 407 feet W. of the S. E Corner of Lot 2. Proceeding thence N 35° W 40' Thence N 27° W 37' Thence N. 18° W 36' Thence N 9° W. 92' Thence N 10° W 36' Thence N. 39' Thence N 7° W 40 Thence N 12° W. 40' Thence N 23° W. 40'. Thence N 15° W. 36' Thence N 2° E. 37' Thence N 58° W 67' Thence N 66° W 55' Thence N 70° W 51' Thence N. 77° W. 46' Thence N 87° W 45'. Thence N 88° W 45' Thence N. 50° W 35' Thence N 25° W 36' Thence N 20° W 175' Thence N 12° W 36'. Thence N 45° W 36' Thence N 40° W 35' Thence N. 30° W 37' Thence N. 40° W 35' Thence N 28° W 37' Thence N. 30° W 37'. Thence N. 34° W. 43' Thence N. 37° W 43' Thence N 55° W 40' Thence N. 47° W 30' Thence N 57° W 40' Thence N. 55° W 41.5' Thence N. 45° W. 35' Thence N. 51° W 36' Thence N. 67° W 9'. Thence N 81° E. 53' Thence N 48° W 8' Thence S 1° W 63' to high water mark thence S. E along high water mark paralel to the line just described 1503' Thence E. 6' to place of beginning.

State of Michigan,
County of Clare. } ss.
Received for record the 4th day of ... A. D. 1920 at 1:30 o'clock P. M. and recorded in Vol. 1 of Village Plats page 30

Emma Hoy
Dep'y Register of Deeds