Supervisor's Plat of "OAKWOOD"

LOCATED IN THE SW. CORNER OF THE SW. 1/4 OF THE SE. 1/4 OF SEC. 8 T.18N. R.5W. LINCOLN TWP. CLARE COUNTY STATE OF MICHIGAN

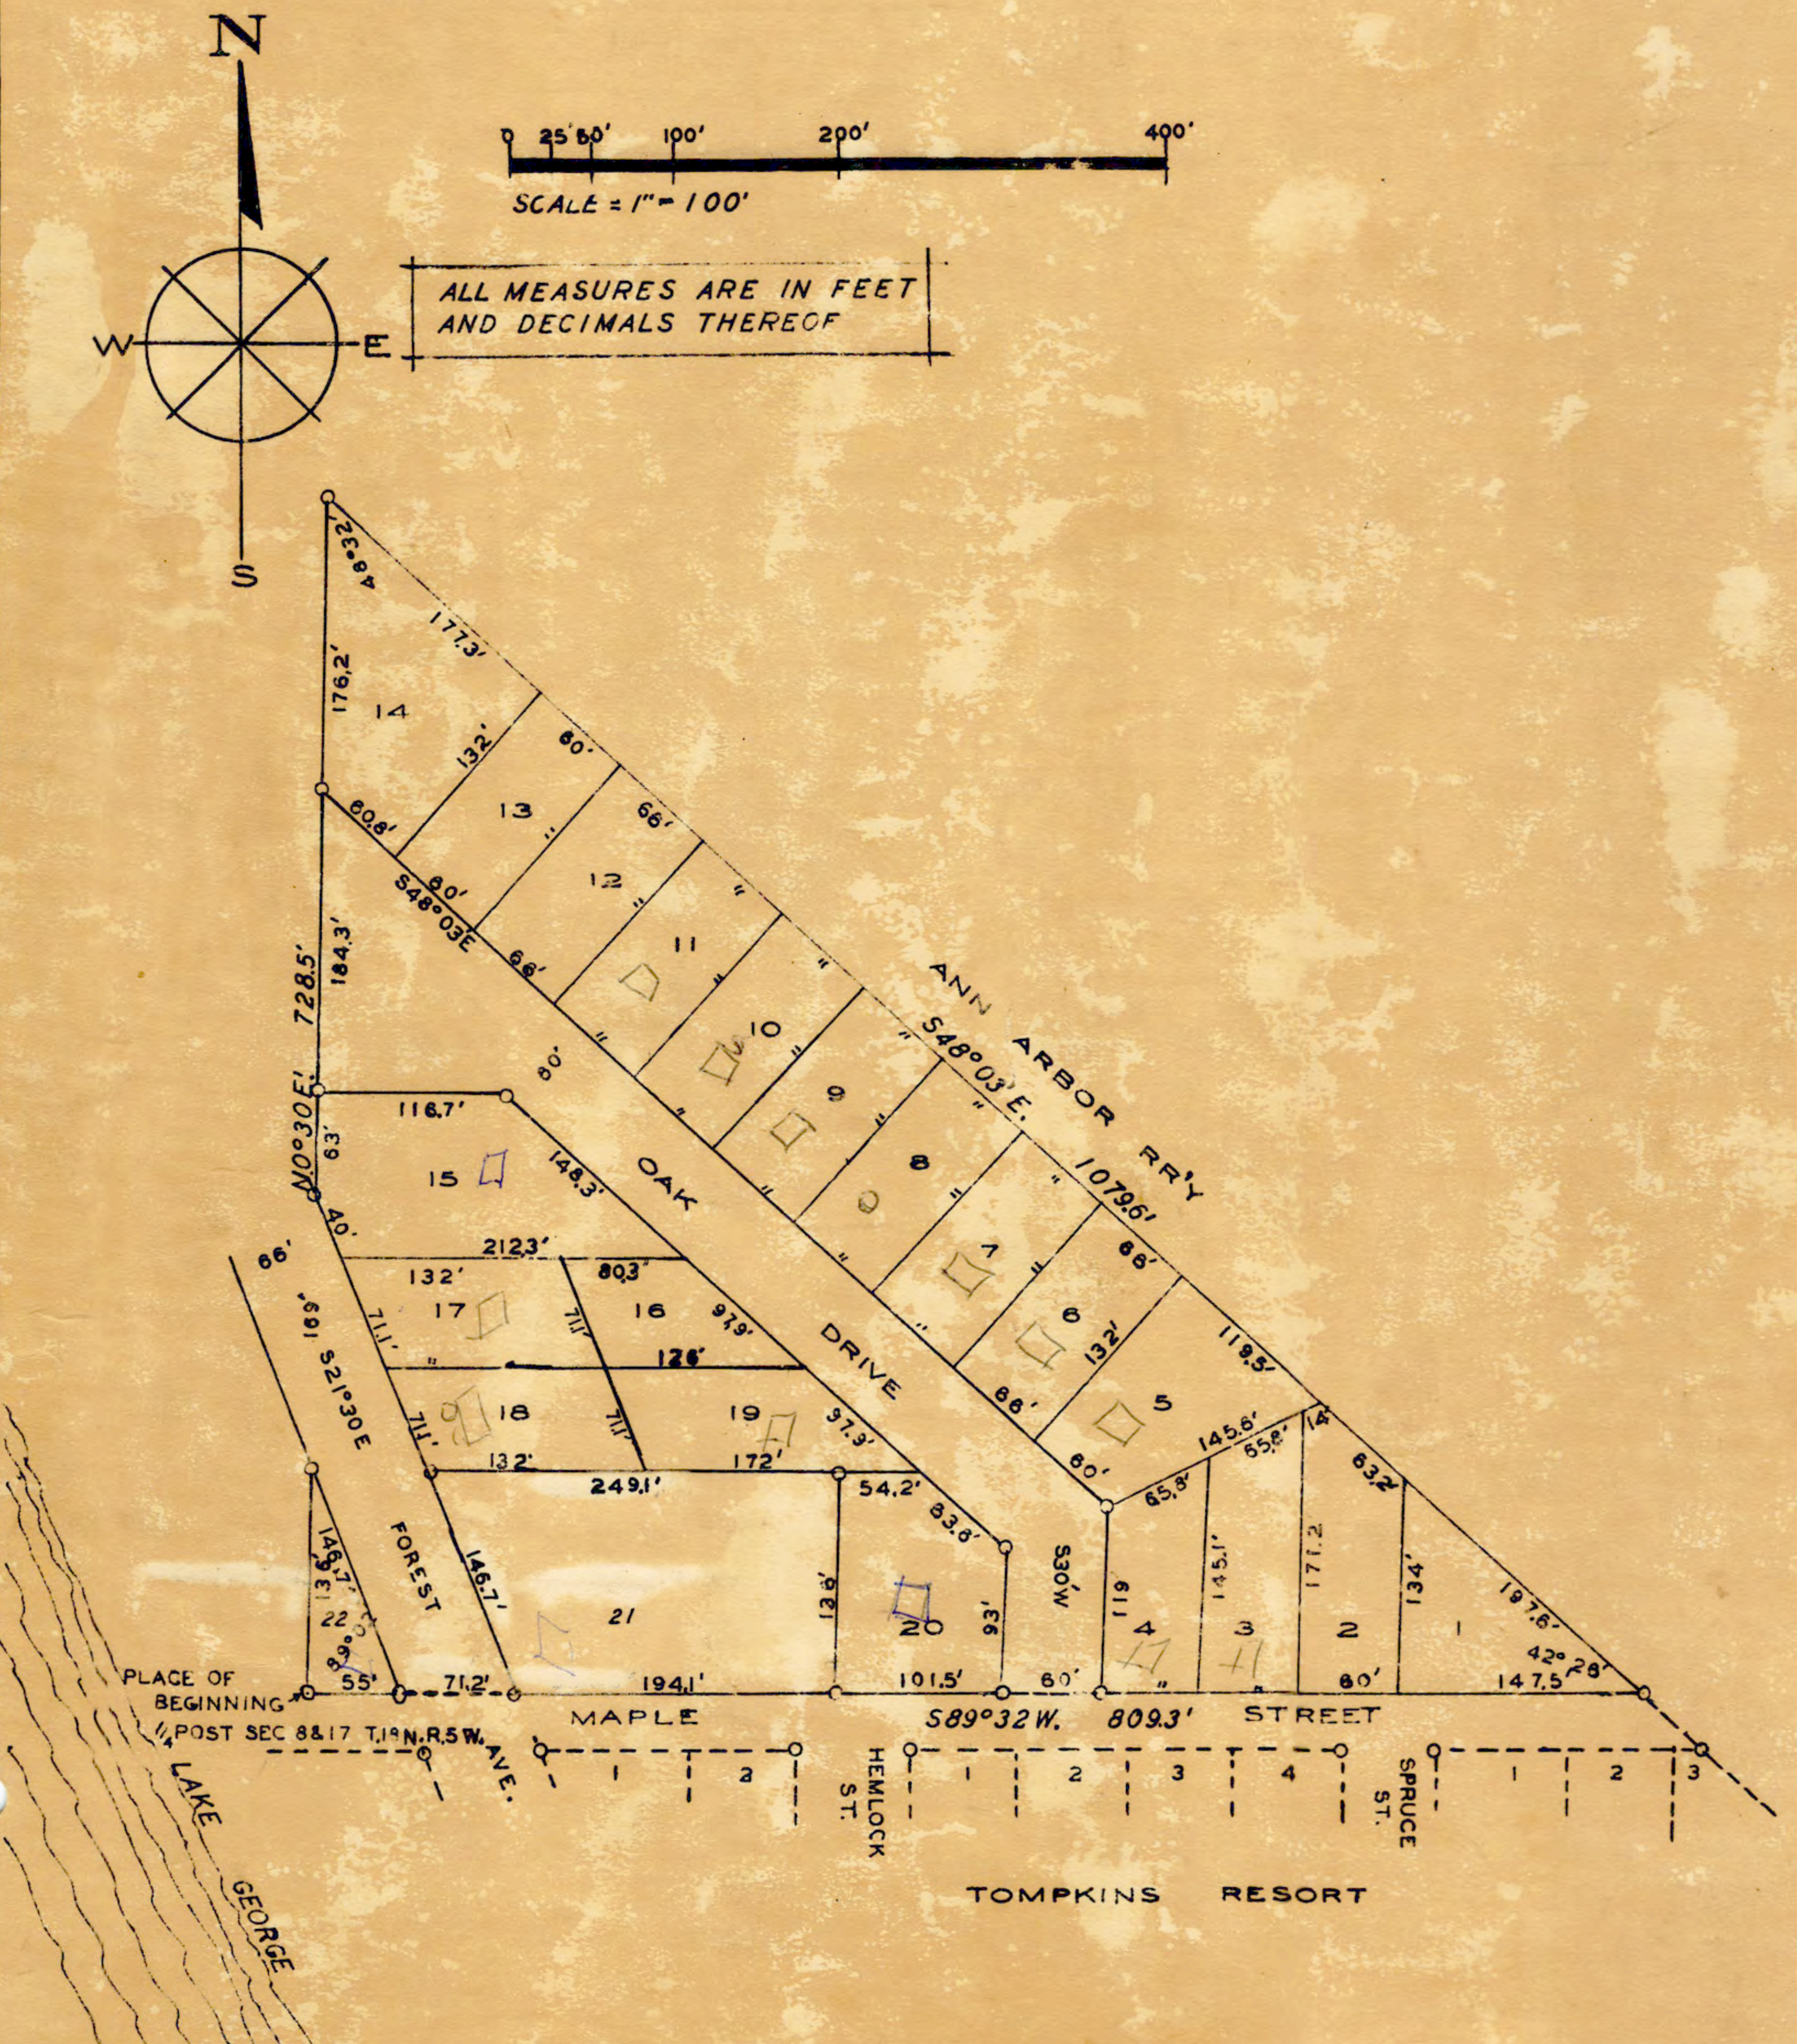

DESCRIPTION OF LAND PLATTED

The land embraced in the annexed plat of Supervisor's plat of Oakwood Located in the SW. corner of the SW1/4 of the SE1/4 of Sec. 8, T18N, R5W, *LINCOLN TWP CLARE CO STATE OF MICHIGAN* is described as follows:

Beginning at the 1/4 post of Sec . 8 and 17 of T18N (Lincoln) R5W, thence N0°30'E 728.5 ft., Thence S48°03'E 1079.6 ft., Thence S89°32'W 809.3 ft., to the place of beginning. This plat has *22* lots

APPROVAL BY COUNTY PLAT BOARD

This plat was approved on the 18th day of July 1957 by the Clare County Plat Board

Wm. A. Henderson
Wm. A. Henderson (County Register of Deeds)

Albert Haley (County Clerk)
Albert Haley (Chairman of Supervisors)

Lewis F. Rutter
LEWIS F. RUTTER ~~Peter A. Smith~~ (County Treasurer)

Bruce Williams
Bruce Williams (County Drain Commissioner)

APPROVAL BY BOARD OF COUNTY ROAD COMMISSIONERS

This plat has been examined and was approved on the 4th day of May 1957 by the Clare County Board of Road Commissioners.

Avery Barber
Avery Barber (Chairman)

Fred L. Jones
Fred L. Jones (Member)

Ed R. Bruce
Ed R. Bruce (Member)

I hereby certify this copy is a true copy of map or plat forwarded the Register of deeds for recording.

Date August 2, 1957

FILED IN AUDITOR GENERAL'S DEPT.

Date August 7, 1957

EXAMINED AND APPROVED

Date August 2, 1957

Frank Szymanski
Auditor General

By D. S. MacElroy
Plat Engineer

COPY

Register's Office
Clare County. } ss.

Plat of Supervisor's Plat of Oakwood

was Recorded this 5th day of August A.D., 1957 at 11 O'clock AM, in Liber 5 of Plats on Page 7

William A. Henderson
Register of Deeds

ORIGINAL ON FILE

DEDICATION

KNOW ALL MEN BY THESE PRESENTS, That I, Russell Kress Supervisor, of Lincoln Township of Clare County, State of Michigan, by virtue of authority in me vested by Section 51, Act 172, of 1929, having been duly authorized by the Township Board have caused the land described in the annexed plat to be surveyed, laid out and platted, to be known as Supervisor's Plat of Oakwood, Located in the SW. corner of the SW. 1/4 of the SE1/4 of Sec. 8, T18N, R5W, *LINCOLN TWP CLARE CO. STATE OF MICHIGAN* and that the streets and alleys as shown on said plat are now being used for such purposes. AND THE PLAT CONFORMS WITH THE REQUIREMENTS OF SEC. 51 ACT 172 OF PUBLIC ACTS OF 1929 AS AMENDED

Louis H. Hoover
LOUIS H. HOOVER (Witness)

Kenneth Clark
KENNETH CLARK (Witness)

Russell K. Kress (Seal)
Russell Kress
Supervisor of the township of Lincoln

ACKNOWLEDGMENT

STATE OF MICHIGAN
County of Clare } ss.

On this 24th day of January A.D. 1957, before me, a Notary Public in and for said county, personally came the above named Russell Kress, Supervisor, of Lincoln Township, known to me to be the person who executed the above dedication, and acknowledged the same to be his free act and deed as such Supervisor

James S. Bicknell
James S. Bicknell
Notary Public in and for Clare County.

My Commission expires July 18 1959.

MUNICIPAL APPROVAL

This plat was approved by the Twp. Board of the Twp of Lincoln of County of Clare at a meeting held Lake George Nov 13, 1956

Howard Ryckman
Howard Ryckman (Clerk)

SURVEYOR'S CERTIFICATE

I hereby certify that the plat hereon delineated is a correct one, and that permanent monuments consisting of iron rods at least one half inch in diameter and 36 inches in length, encased in concrete cylinders four inches in diameter and 36 inches in length, have been set at points marked thus (0) as thereon shown at all angles in the boundaries of the land platted, at all intersections of the lines of streets and at intersections of the lines of streets with the boundaries of the plat.

Frank McClung
Frank McClung No. 165
Registered Land Surveyor ~~Registered Professional Engineer~~

340