Examined and Approved
Nov 30-1923
Jo. L. Hussey
Deputy Auditor General

COPY PLAT OF
SHORE WOOD SUMMER RESORT.
CLARE COUNTY MICHIGAN.

DESCRIPTION OF LAND PLATTED.

The Land embraced in the annexed plat of Shore Wood Summer Resort Clare County Michigan, is described as follows. Comencing at 1/4 Section Corner common to Sections 8 and 17 T.18.N.R.5 W. Clare County Michigan, proceeding Thence N.169 feet Thence W. 20 feet. Thence N.40°W. 190 feet. Thence N. 65°W.100 feet. Thence N. 40°W. 190 feet. Thence N. 20°W 350 feet. Thence N.32°30' W 240 feet. Thence N.10°W. 60 feet. Thence W.165 feet Thence S.10°E 150 feet. Thence S. 32°30' E. 250 feet. Thence S.20°E. 360 feet. Thence S.40°E 200 feet Thence S. 65°E. 100 feet. Thence S. 40°E 274 feet. Thence E.100 feet to place of beginning. The entire plat being part of Lot 2. Section 8.

DEDICATION.

Know all Men by these presence That we Norman Tolson as proprietor and Magdalena W. Tolson his wife, have caused the Land embraced in the annexed plat to be surveyed laid out and platted to be known as Shore Wood Summer Resort, Clare County Mich. and that the streets and alleys as shown on said plat are hereby dedicated to the use of the public.

Signed and sealed in presence of
[illegible] ---
Chas. E. Willey ---

Norman Tolson ---[L.S]
Magdalena W. Tolson ---[L.S]

State of Missouri. } ss.
County of Jackson --- }

On this -- 22d -- day of Nov 1923
Before me a Notary public. in and for said County. personally came the above named Norman Tolson and Magdalena W. Tolson his wife known to me to be the persons who executed the above dedication and acknowledged the same to be their free act and deed.

William [illegible] ---

- Notary Public for ~~Clare County Mich.~~ Jackson County Mo.

My Commission expires January 15 1927

SURVEYORS CERTIFICATE.

I hereby Certify that the plat hereon delineated is a correct one and that permanent monuments consisting of gaspipe ranging from 3/4 inch to 1 1/4 inch in diameter and from 18 inch to 30 inches in length have been planted at points marked thus. (o) as thereon shown at all angles in the boundaries of the Land platted. and at all intersections. of streets or streets and alleys.

Arthur D. Johnson
Registered Surveyor.

CERTIFICATE OF MUNICIPAL APPROVAL.

This plat was approved by the Township Board of the Township of Lincoln at a meeting held -- Nov 26 -- -- 1923

W. Hansen --
Clerk

CERTIFICATE OF APPROVAL BY COUNTY BOARD.

This plat was approved on the -- 27th ------ day of November -- 1923

Thomas J. Dowey
Judge of Probate

Emma Hoag ---
Deputy County Clerk

Fred W. Schaaf ---
County Treasurer.

Clare County.
Plat of
Shorewood Summer Resort
Recorded this 1st day of
Dec A.D. 1923 At 2 O'Clock
P.M. in Liber 1 of Plats
141
Marion C. Johnson
Deputy Register of Deeds.

I hereby certify that there are no tax liens or titles held by the state on the Lands described in this instrument and that there are no tax liens or titles held by individuals on the said Lands. and that the taxes on said Lands for the five years preceding the date of said instrument are all paid as shown by the records of this office.
Harrison Mich. November 27 1923
Fred W. Schaaf
C. Treasurer.

[illegible] PLAT [illegible] FOR RECORD
CONFIRMED Nov 30-1923
Jo. L. Hussey
DEPUTY AUDITOR GENERAL.

FILED IN AUDITOR GENERAL'S DEPT.
Dec 6 1923
Jo. L. Hussey
[illegible] AUDITOR GENERAL.

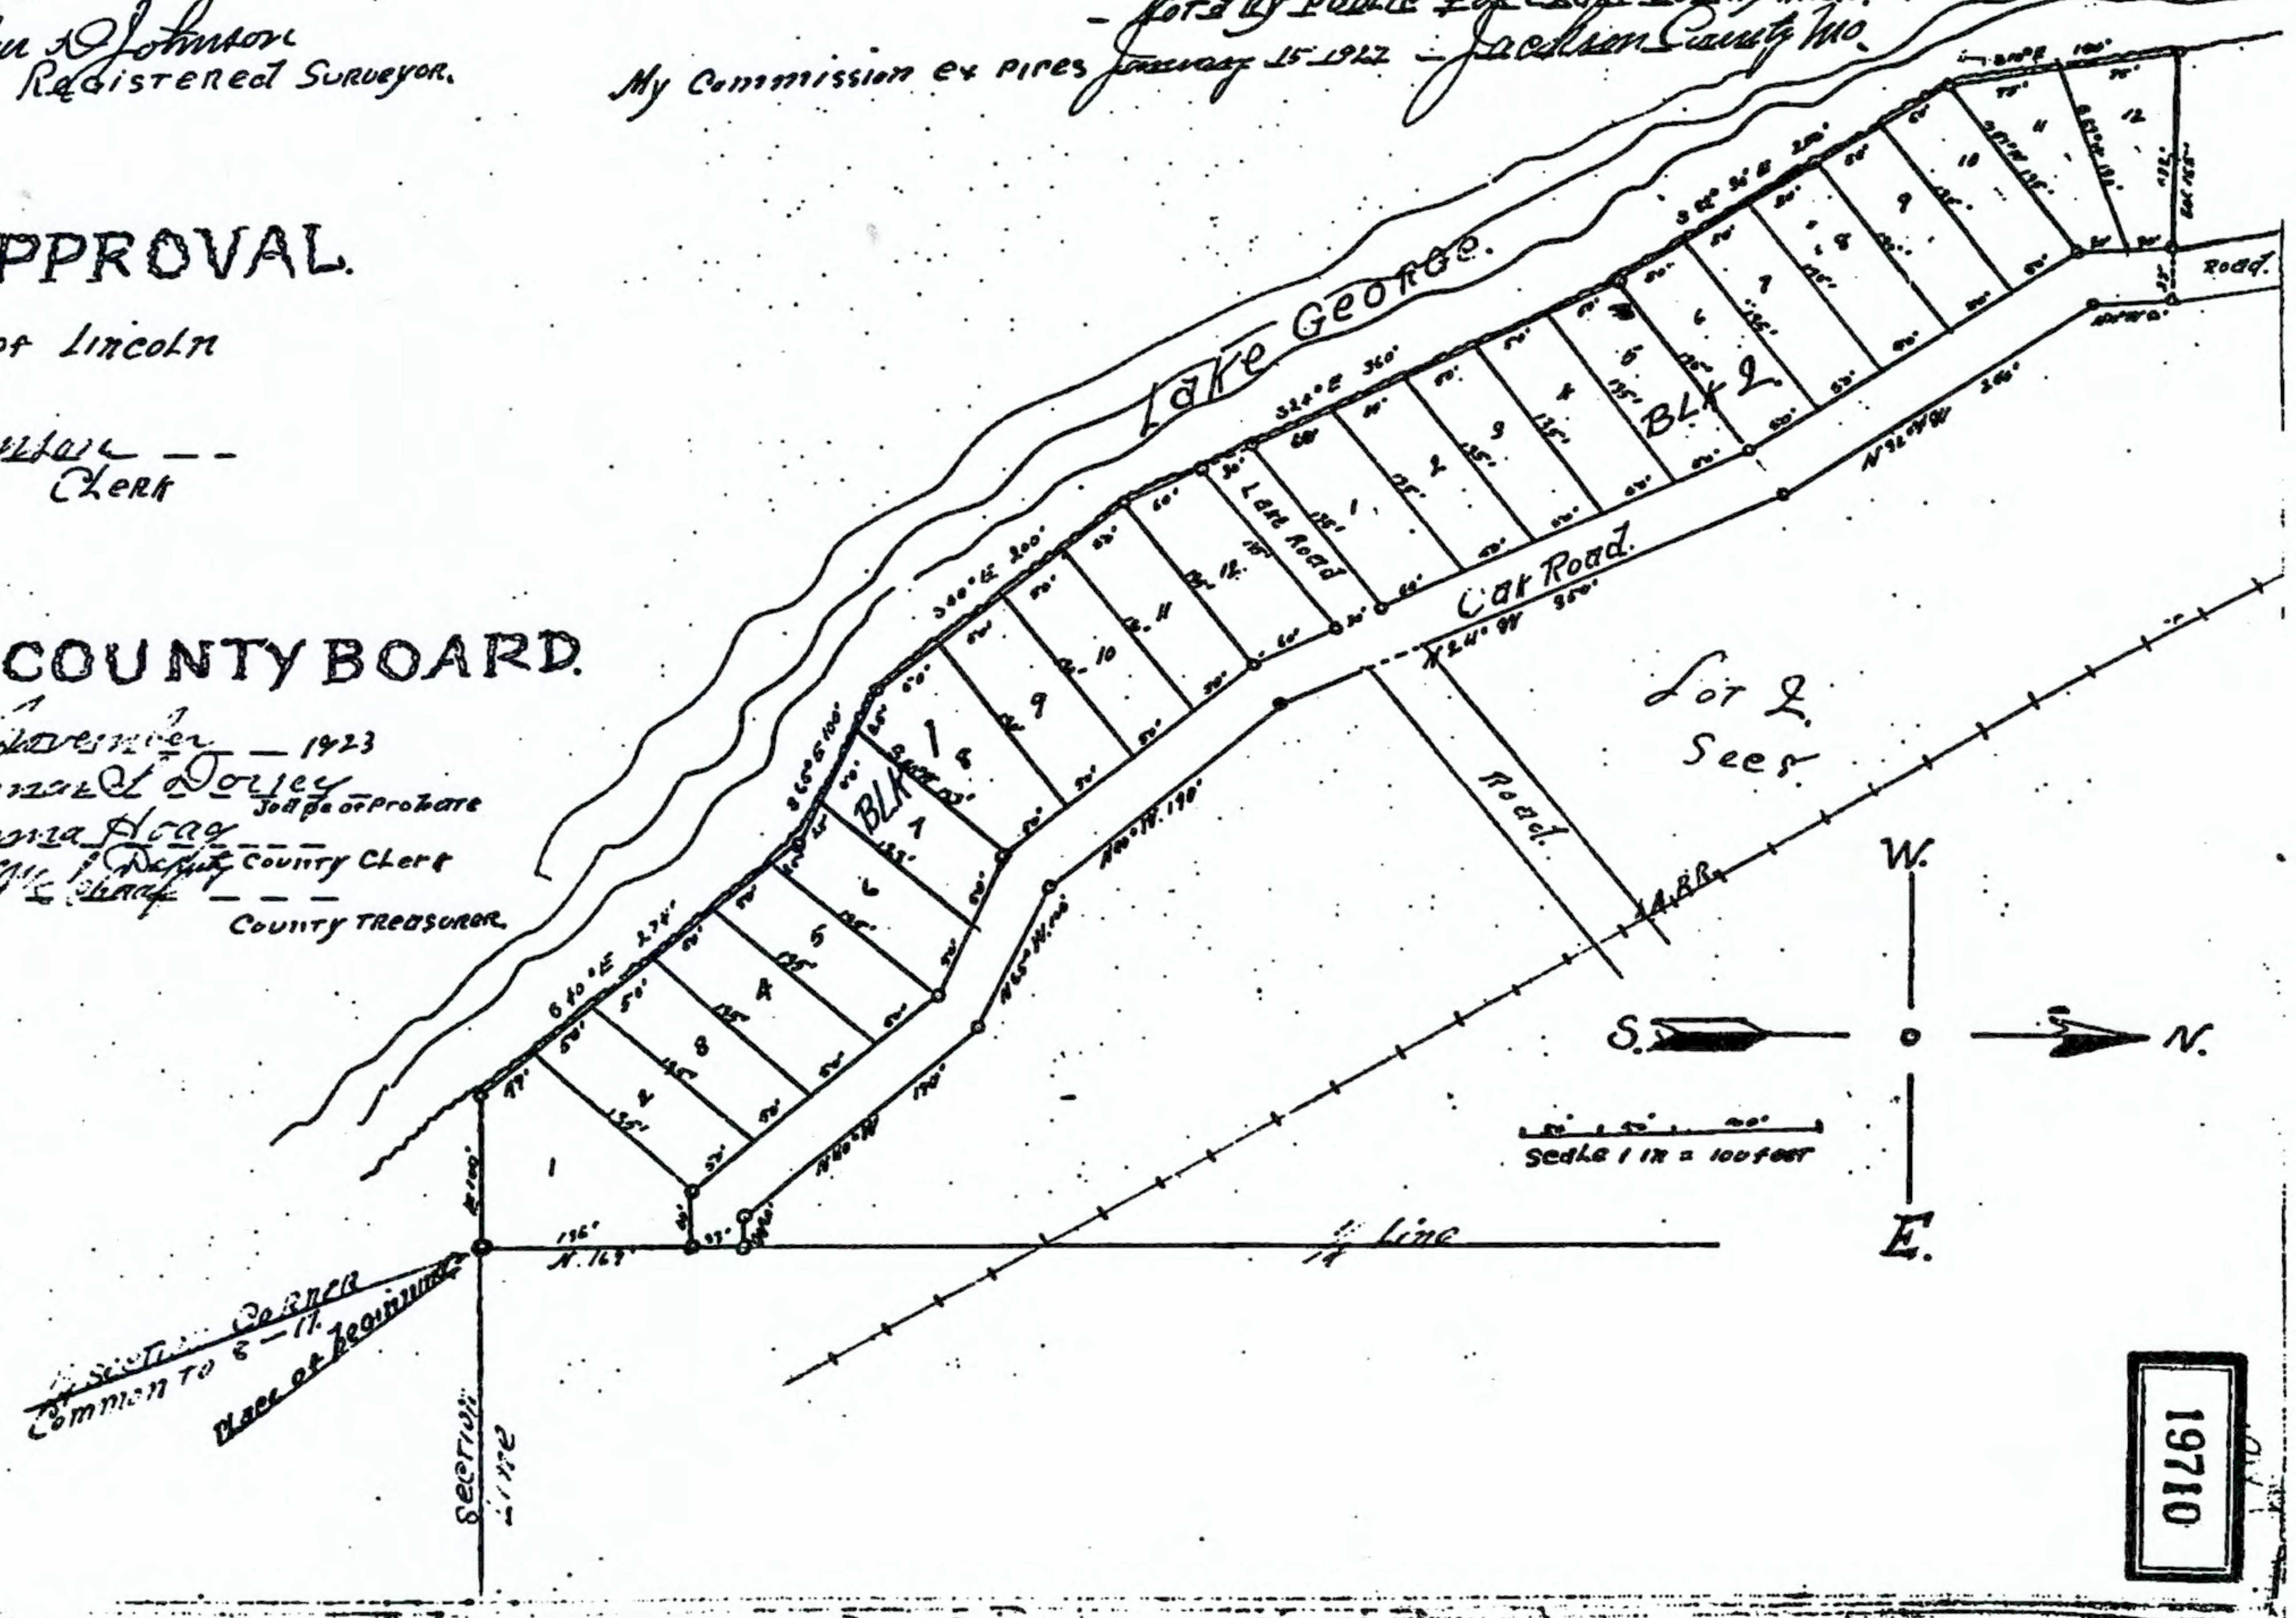

19710