
TINDALL SUBDIVISION

Part of the SE¼ NW¼ of Section 30, T 18 N, R 5 W, Lincoln Township, Clare County, Michigan.

SCALE 1" = 50'
ALL DIMENSIONS ARE IN FEET AND DECIMALS THEREOF
0 50 100 200 300

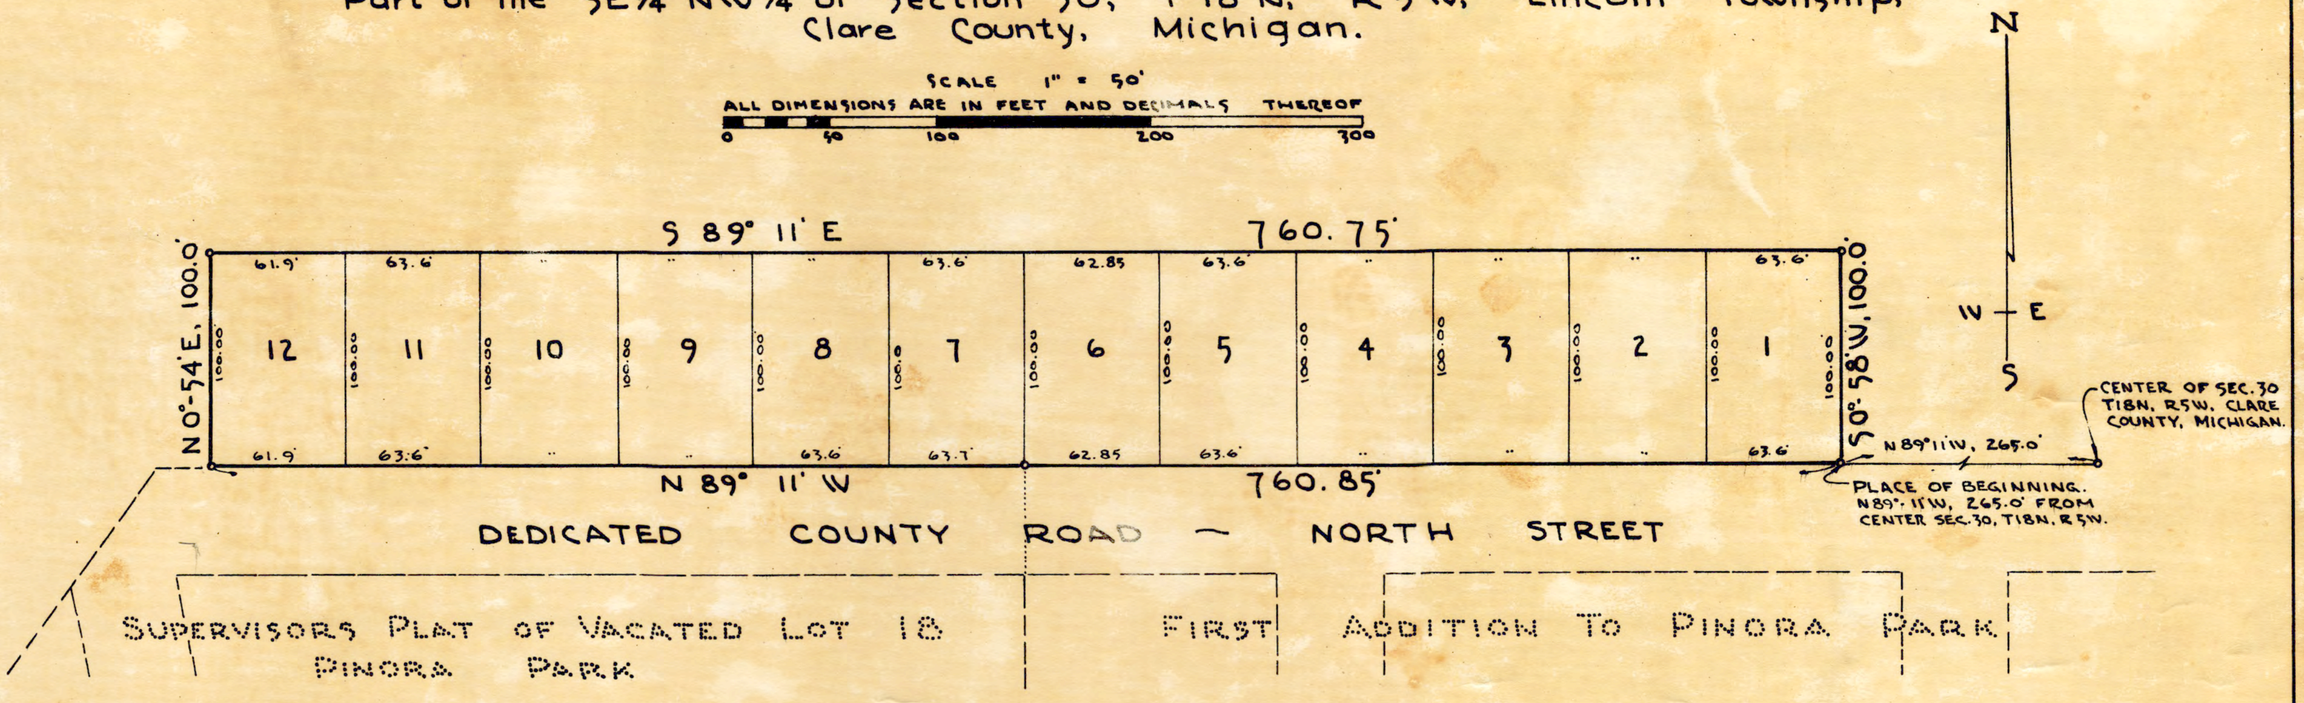

DEDICATION

KNOW ALL MEN BY THESE PRESENTS, That we Odis Tindall and Miriam Tindall his wife, as proprietors, have caused the land embraced in the annexed plat to be surveyed, laid out and platted, to be known as TINDALL SUBDIVISION, Part of the SE 1/4 NW 1/4 of Section 30, T 18 N, R 5 W, Lincoln Township, Clare County, Michigan, and that the streets and alleys as shown on said plat are hereby dedicated to the use of the public.

Signed and Sealed in the Presence of

Evelyn Warner
EVELYN WARNER

Ida Mae Loomis
IDA MAE LOOMIS

Odis Tindall (L.S.)
Odis Tindall

Miriam Tindall (L.S.)
Miriam Tindall

ACKNOWLEDGMENT

STATE OF MICHIGAN) ss
County of Clare)

On this 5th day of September A.D. 19 59, before me, a Notary Public in and for said county, personally came the above named Odis Tindall and Miriam Tindall his wife, known to me to be the persons who executed the above dedication, and acknowledged the same to be their free act and deed.

IDA MAE LOOMIS
Notary Public, Clare County, Michigan
My Commission expires My Commission Expires Sept. 25, 1959

Ida Mae Loomis
IDA MAE LOOMIS
Notary Public, Clare County, Michigan

DESCRIPTION OF LAND PLATTED

The land embraced in the annexed plat of TINDALL SUBDIVISION, Part of the SE 1/4 of the NW 1/4 of Section 30, T 18 N, R 5 W, Lincoln Township, Clare County, Michigan, is described as follows: Beginning N 89° 11' W, 265.0 ft. from the Center of Section 30, T 18 N, R 5 W, Lincoln Township, Clare County, Michigan, thence N 89° 11' W, 760.85 ft., thence N 00° 54' E, 100.00 ft., thence S 89° 11' E, 760.75 ft., thence S 00° 58' W, 100.00 ft. to the Place of Beginning. This plat contains 12 numbered lots.

CERTIFICATE OF MUNICIPAL APPROVAL

This plat was approved by the Township Board of the Township of Lincoln at a meeting held Sept. 14, 1959 and that the width of lots is in compliance with requirements of Section 30, Act 172, of 1929, as amended.

Virgil W. Stiner
~~Howard Ryckman~~ Clerk
Virgil W. Stiner.

COPY
Register's Office } ss.
Clare County. }
Plat of Tindall Subdivision
was Recorded this 4th day of December A.D., 1959 at 1:15 O'clock P M, in Liber 5 of plats on Page 48
Wm. A. Henderson
Register of Deeds

I hereby certify this copy is a true copy of map or plat forwarded the Register of deeds for recording
Date December 3, 1959
FILED IN AUDITOR GENERAL'S DEPT.
Date December 8, 1959
EXAMINED AND APPROVED
Date December 3, 1959
Otis M. Smith
OTIS M. SMITH
AUDITOR GENERAL
By D. L. MacElroy
D. L. MacElroy - Plat Engineer

COUNTY TREASURER'S CERTIFICATE RELATING TO TAXES

Office of the County Treasurer, Clare County, Michigan.

I hereby certify, That there are no tax liens or titles held by the State on the lands described hereon, and that there are no tax liens or titles held by individuals on said lands, for the five years preceding the 12 day of November 1959 and that the taxes for said period of five years are paid, as shown by the records of this office.
This certificate does not apply to taxes, if any, now in process of collection by township, city or village collecting officers.

Lewis F. Rutter
Lewis F. Rutter County Treasurer

CERTIFICATE OF APPROVAL BY BOARD OF COUNTY ROAD COMMISSIONERS

This plat has been examined and was approved on the 7th day of October 1959 by the Clare County Board of Road Commissioners.

Avery Barber
Avery Barber Chairman

Fred L. Jones
Fred L. Jones

N. V. Myers
N. V. Myers

CERTIFICATE OF APPROVAL BY COUNTY BOARD

This plat was approved on the 12th day of November 1959 by the Clare County Plat Board.

Wm. A. Henderson
Wm. A. Henderson Register of Deeds

Lewis F. Rutter
Lewis F. Rutter County Treasurer

Bruce Williams
Bruce Williams Drain Commissioner

Albert Haley
~~Thomas W. Hecker~~ Ch. Bd. of Supervisors
ALBERT HALEY

SURVEYOR'S CERTIFICATE

I hereby certify that the plat hereon delineated is a correct one and that permenent metal monuments consisting of bars not less than one-half inch in diameter and 36 inches in length, encased in a concrete cylinder at least 4 inches in diameter and 36 inched in depth have been placed at points marked thus (o) as hereon shown at all angles in the boundaries of the land platted, at all the intersections of streets, intersections of alleys, or of streets and alleys, and at the intersections of streets and alleys with the bounderies of the plat as shown on said plat.

Paul B. Lapham
Paul B. Lapham
Registered Surveyor No. 9433