Plat of:

CANOE SUBDIVISION

LOCATED IN THE N.W. 1/4 OF THE S.E. 1/4 OF SECTION 22 T. 18 N. (LINCOLN) R. 5 W. CLARE COUNTY - STATE OF MICHIGAN.

N

APPROVAL BY BOARD OF COUNTY ROAD COMMISSIONERS

This plat has been examined and was approved on the 6th day of September 1958 by the Clare County Board of Road Commissioners.

Audley Barber (Chairman)
Ayery Barber

Fred Jones (Member)
Fred Jones

Ed. R. Bruce (Member)
Ed. R. Bruce

APPROVAL BY COUNTY PLAT BOARD

This plat was approved on the 12th day of September 1958 by the Clare County Plat Board

Wm. A. Henderson (County Register of Deeds)
Wm. A. Henderson

Albert Haley (Chairman of Supervisors)
Thomas W. Hecker
Thom as W. Hecker

Lewis F. Rutter (County Treasurer)
Lewis F. Rutter


Bruce Williams (County Drain Commissioner)
Bruce Williams

CERTIFICATE OF MUNICIPAL APPROVAL

This plat was approved by the Township Board of the Township of Lincoln at a meeting held July 14, 1958 and that the width of lots is in compliance with requirements of Section 30, Act 172, of 1929, as amended.

Howard Ryckman
Howard Ryckman Clerk.

PLACE OF BEGINNING: BEING THE N.W. CORNER OF THE S.E. 1/4 OF SECTION 22 T. 18 N. R. 5 W. CLARE CO.

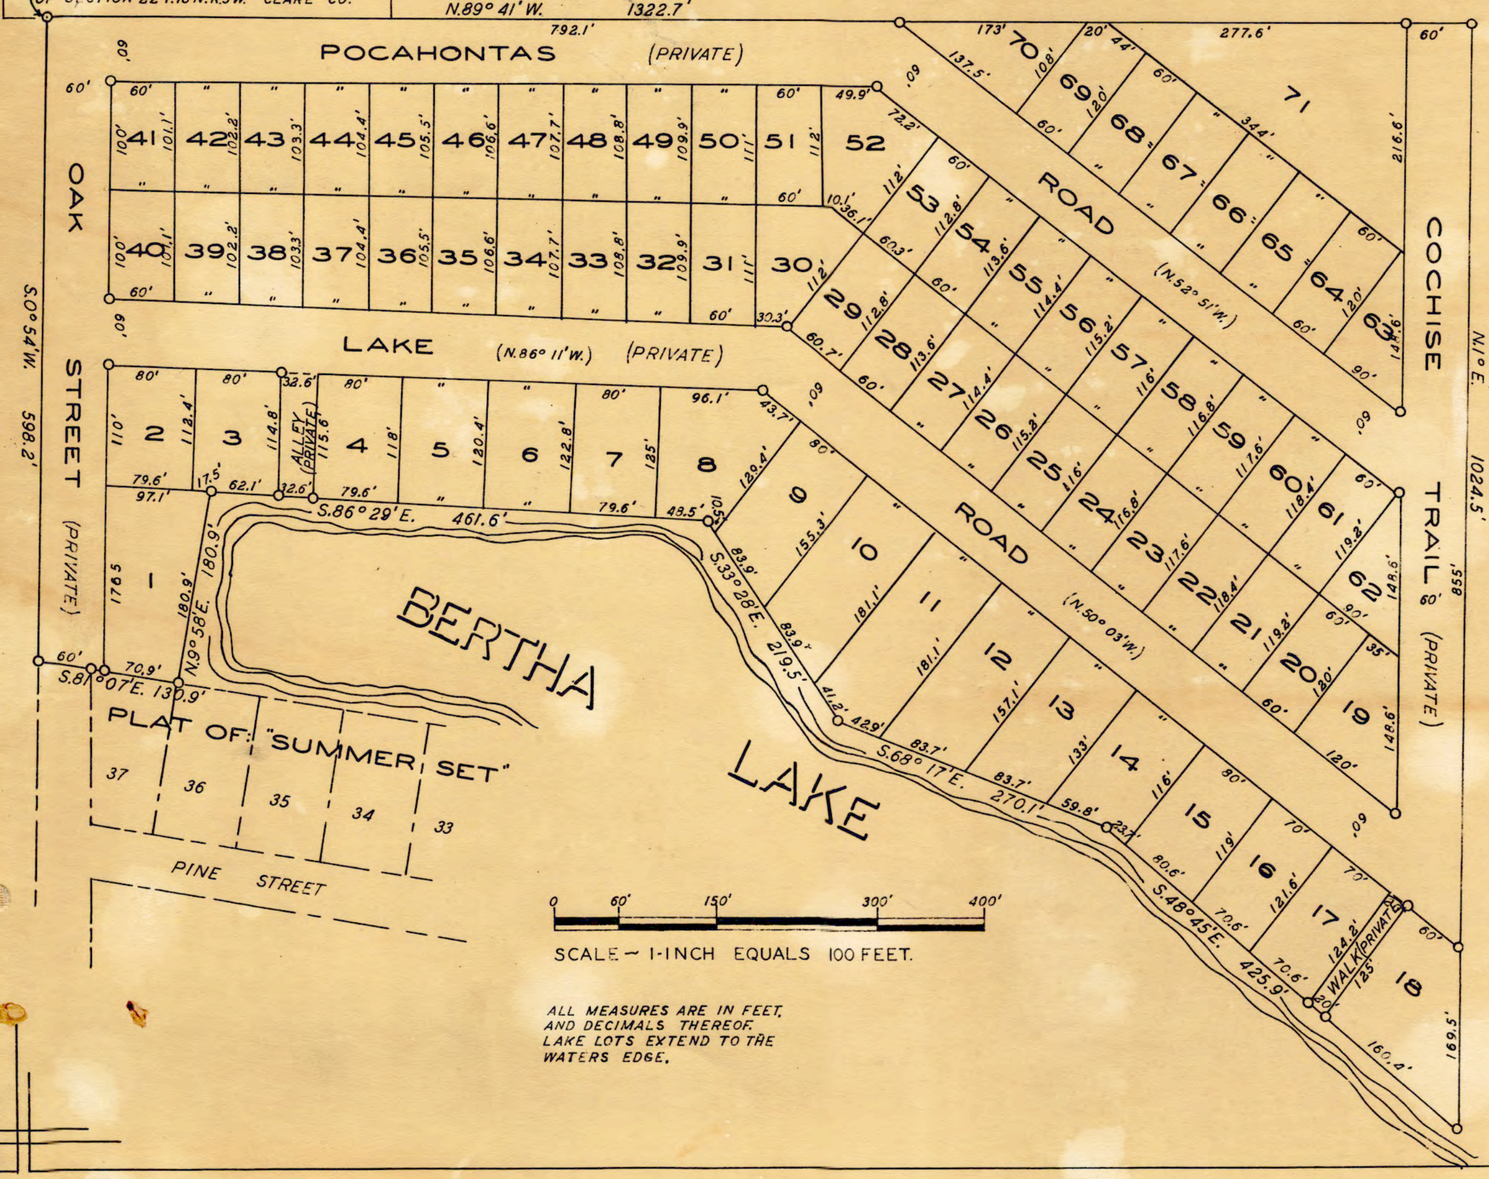

ALL MEASURES ARE IN FEET, AND DECIMALS THEREOF. LAKE LOTS EXTEND TO THE WATERS EDGE.

DEDICATION

KNOW ALL MEN BY THESE PRESENTS, that we A. Lee Swallow and Margaret I. Swallow his wife as proprietors, have caused the land embraced in the annexed plat to be surveyed, laid out and platted, to be known as Plat of Canoe Subdivision Located in the NW 1/4 of the SE1/4 of section 22 T18N (Lincoln) R5W Clare County, State of Michigan and that the streets, ALLEYS AND WALKS as shown on said plat are hereby dedicated to the use of THE LOT OWNERS.

Signed and Sealed in the Presence of:

James Davis (Witness) A. Lee Swallow (L. S.)
JAMES DAVIS A Lee Swallow

Doris N. Davis (Witness) Margaret I. Swallow (L. S.)
DORIS N. DAVIS Margaret I. Swallow

ACKNOWLEDGMENT

STATE OF MICHIGAN } ss.
County of Clare

On this 11 day of July 1958, before me, a Notary Public in and for said County, personally came the above named A Lee Swallow and Margaret I. Swallow - his wife known to me to be the persons who executed the above dedication, and acknowledged the same to be their free act and deed.

James Davis
JAMES DAVIS Notary Public Clare County
My Commission expires Nov. 9, 1959

DESCRIPTION OF LAND PLATTED

The land embraced in the annexed plat of Canoe Subdivision Located in the NW1/4 of the SE1/4 of section 22 T18N, (Lincoln) R5W Clare County, State of Michigan is described as follows:

Beginning at the NW corner of the SE1/4 of section 22 T18N, R5W, Clare County, Thence S54°W 598.2 ft., Thence S81°07'E 130.9 ft., Thence N9°58'E 180.9 ft., Thence S86°29'E 461.6 ft., Thence S33°28'E 219.5 ft., Thence S68°17'E 270.1 ft., Thence S48°45'E 425.9 ft., Thence N1°E 1024.5 ft., Thence N89°41'W 1322.7 ft. to the place of beginning. There are 71 lots in this description.

COPY

Register's Office } ss.
Clare County.
Plat of Canoe Subdivision
was Recorded this 29th day of September A.D., 1958 at 8:15 o'clock A M, in Liber 5 of plats on Page 27
Wm. A. Henderson
Register of Deeds
ORIGINAL ON FILE

I hereby certify this copy is a true copy of map or plat forwarded the Register of deeds for recording.
Date September 26, 1958
FILED IN AUDITOR GENERAL'S DEPT.
Date October 6, 1958
EXAMINED AND APPROVED
Date September 26, 1958
Auditor General
Plat Engineer

COUNTY TREASURER'S CERTIFICATE

Office of County Treasurer, Clare County.
I hereby certify, that there are no tax liens or titles held by the State on the lands described hereon, and that there are no tax liens or titles held by individuals on said lands, for the five years preceding the 12th day of September 1958 and that the taxes for said period of five years are all paid, as shown by the records of this office:

This certificate does not apply to taxes, if any, now in process of collection by township, city or village collecting officers.

Lewis F. Rutter
LEWIS F. RUTTER (County Treasurer)

SURVEYOR'S CERTIFICATE

I hereby certify that the plat hereon delineated is a correct one and that permanent metal monuments consisting of bars not less than one-half inch in diameter and 36 inches in length, or shorter bars of not less than one-half inch in diameter tapped over each other at least 6 inches with an over-all length of not less than 36 inches, encased in a concrete cylinder at least 4 inches in diameter and 36 inches in depth have been placed at points marked thus (O) as thereon shown at all angles in the boundaries of the land platted, at all the intersections of streets, intersections of alleys, or of streets and alleys, and at the intersections of streets and alleys with the boundaries of the plat as shown on said plat.

Frank McClung
Registered Land Surveyor
Frank McClung