Plat of the "DAVIS SUBDIVISION"

BEING A TRACT OF LAND IN THE NE. CORNER OF THE SW.1/4 OF THE SE.1/4 OF SEC. 7 OF T.18N.(LINCOLN) R.5W. CLARE COUNTY, STATE OF MICHIGAN.

COUNTY TREASURER'S CERTIFICATE

Office of County Treasurer, Clare County.

I hereby certify, that there are no tax liens or titles held by the State on the lands described hereon, and that there are no tax liens or titles held by individuals on said lands, for the five years preceding the 15 day of December 1960 and that the taxes for said period of five years are all paid, as shown by the records of this office .....

.....

This certificate does not apply to taxes, if any, now in process of collection by township, city or village collecting officers.

Lewis F. Rutter (County Treasurer)

LEWIS F. RUTTER

APPROVAL BY COUNTY PLAT BOARD

This plat was approved on the 15th day of December 1960 by the Clare County Plat Board


Wm. A. Henderson (County Register of Deeds)

Albert Haley (Chairman of Supervisors)

Lewis F. Rutter (County Treasurer)

Bruce Williams (County Drain Commissioner)

WEST END ST.

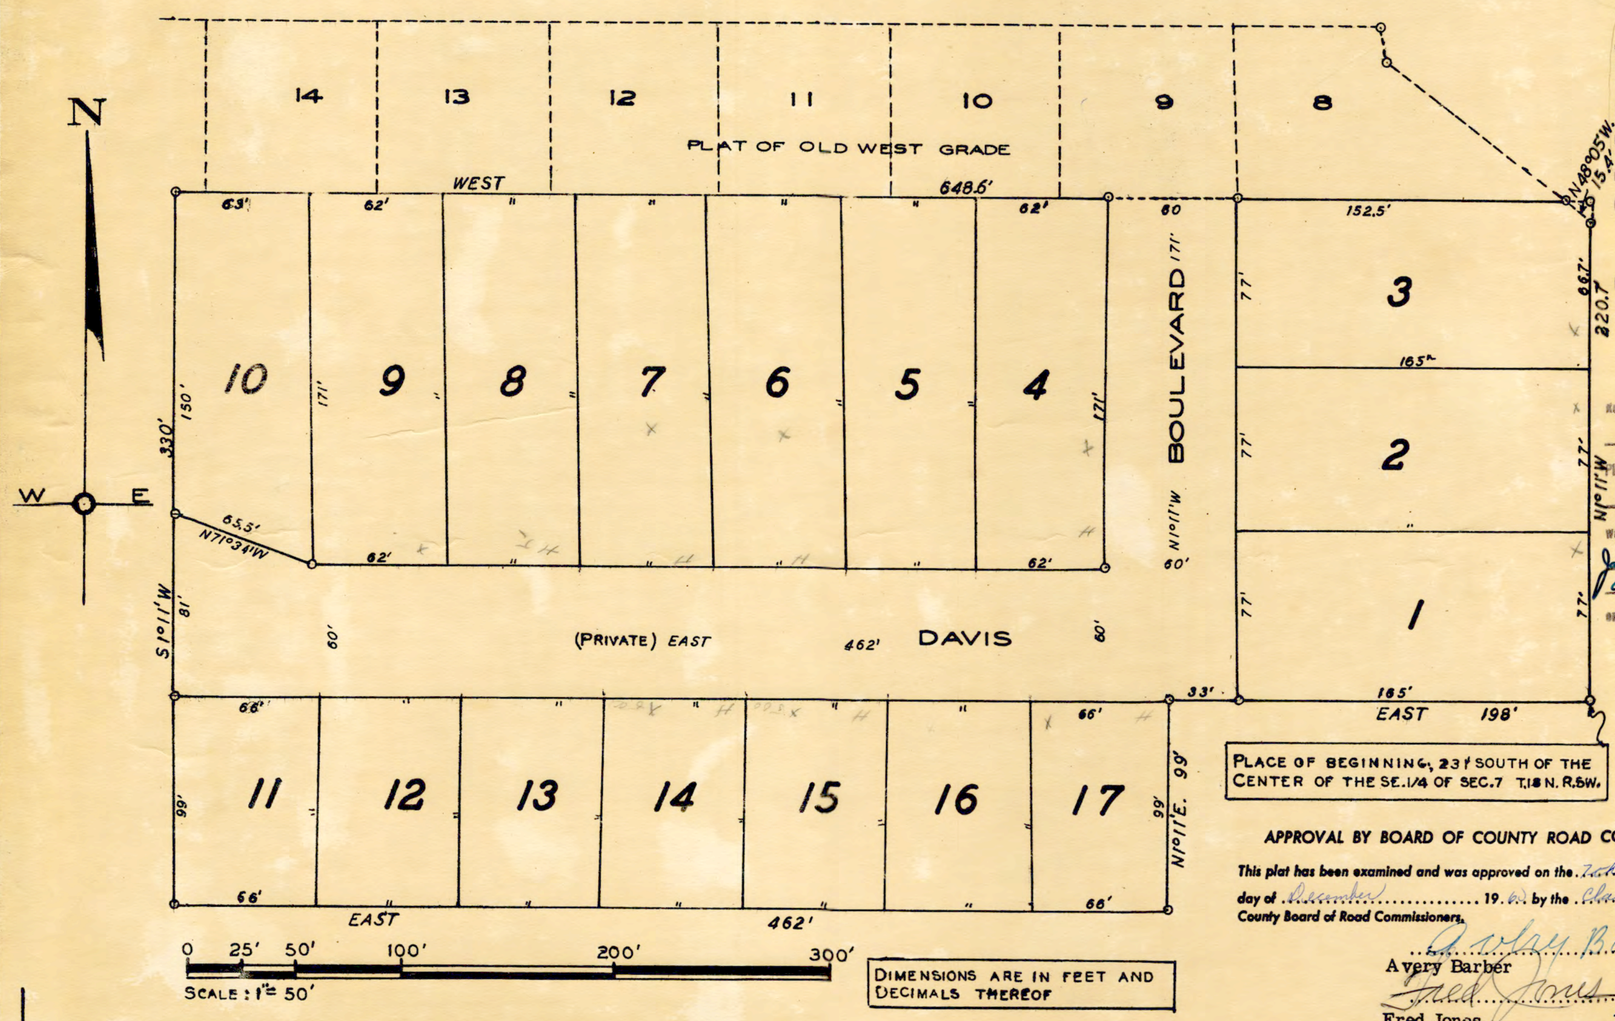

PLACE OF BEGINNING, 231 SOUTH OF THE CENTER OF THE SE.1/4 OF SEC.7 T.18 N. R.5W.

DIMENSIONS ARE IN FEET AND DECIMALS THEREOF

APPROVAL BY BOARD OF COUNTY ROAD COMMISSIONERS

This plat has been examined and was approved on the 7th day of December 19 60 by the Clare County Board of Road Commissioners.

Avery Barber (Chairman)

Fred Jones (Member)

Norman Myers (Member)

I hereby certify this copy is a true copy of map or plat forwarded the register of deeds for recording.

Date January 23, 1961

FILED IN AUDITOR GENERAL'S DEPT.

Date February 2, 1961

EXAMINED AND APPROVED

Date January 23, 1961

Otis M. Smith

OTIS M. SMITH
AUDITOR GENERAL

By Lynn N. Munroe
DEPUTY AUDITOR GENERAL
DIRECTOR, TAX DIVISION

COPY

Register's Office } ss.
Clare County.

Plat of Davis Subdivision was Recorded this 24th day of January A.D., 1961 at 11:00 O'clock A M, in Liber 6 of plats on Page 9

Wm. A. Henderson
Register of Deeds

ORIGINAL ON FILE

SURVEYOR'S CERTIFICATE

I hereby certify that the plat hereon delineated is a correct one and that permanent metal monuments consisting of bars not less than one-half inch in diameter and 36 inches in length, or shorter bars of not less than one-half inch in diameter lapped over each other at least 6 inches with an over-all length of not less than 36 inches, encased in a concrete cylinder at least 4 inches in diameter and 36 inches in depth have been placed at points marked thus (O) as thereon shown at all angles in the boundaries of the land platted, at all the intersections of streets, intersections of alleys, or of streets and alleys, and at the intersections of streets and alleys with the boundaries of the plat as shown on said plat.

Frank McClung
Registered Land Surveyor Professional Engineer
Frank McClung

DEDICATION

KNOW ALL MEN BY THESE PRESENTS, that we James L. Davis and wife Doris N. Davis, Robert B. Kring and wife Violet M. Kring

as proprietors, have caused the land embraced in the annexed plat to be surveyed, laid out and platted, to be known as Plat of the Davis Subdivision Being a tract of land in the NE corner of the SW1/4 of the SE1/4 of Sec. 7 of T18N (Lincoln) R5W Clare County, State of Michigan

and that the streets Davis Boulevard as shown on said plat are hereby dedicated to the use of the lot owners

Signed and Sealed in the Presence of:

Frank McClenathen (Witness) James L. Davis (L. S.)
FRANK McCLENATHEN
James L. Davis

Whilden Hughes (Witness) Doris N. Davis (L. S.)
Whilden Hughes
Doris N. Davis

Robert B. Kring (L. S.)
Robert B. Kring

Violet M. Kring (L. S.)
Violet M. Kring

ACKNOWLEDGMENT

STATE OF MICHIGAN } ss.
County of Clare

On this 30th day of November 1960 before me, a Notary Public in and for said County, personally came the above named James L. Davis and wife Doris N. Davis, Robert B. Kring and wife Violet M. Kring

known to me to be the persons who executed the above dedication, and acknowledged the same to be their free act and deed.

Frank McClenathen
FRANK McCLENATHEN
Notary Public Clare County
My Commission expires Sept 21 1962

DESCRIPTION OF LAND PLATTED

The land embraced in the annexed plat of Davis Subdivision

Being a tract of land in the NE corner of the SW1/4 of the SE1/4 of Section 7, of T18N (Lincoln) R5W Clare County, State of Michigan

is described as follows

Beginning 231 ft. south of the center of the SE1/4 of Sec. 7 of T18N R5W, Thence N1°11'E 220.7 ft., Thence N48°05'W 15.4 ft., Thence West 648.6 ft., Thence S1°11'W 330 ft., Thence East 462 ft., Thence N1°11'E 99 ft., Thence East 198 ft. to the place of beginning.
There are 17 lots in this plat.

CERTIFICATE OF MUNICIPAL APPROVAL

This plat was approved by the Township Board of the Township of Lincoln at a meeting held November 21, 1960 and that the width of lots is in compliance with requirements of Section 30, Act 172, of 1929, as amended.

Virgil Stiner
Virgil Stiner Clerk.