HILLIARD HILLS

Part of the West 1/2 of the West 1/2 of Section 23,
T18N, R5W, Lincoln Township, Clare County, State
of Michigan.

0 50 100 200 300 400 500
Scale: 1"=100'

PAUL B. LAPHAM
LAND SURVEYOR
No. 9433

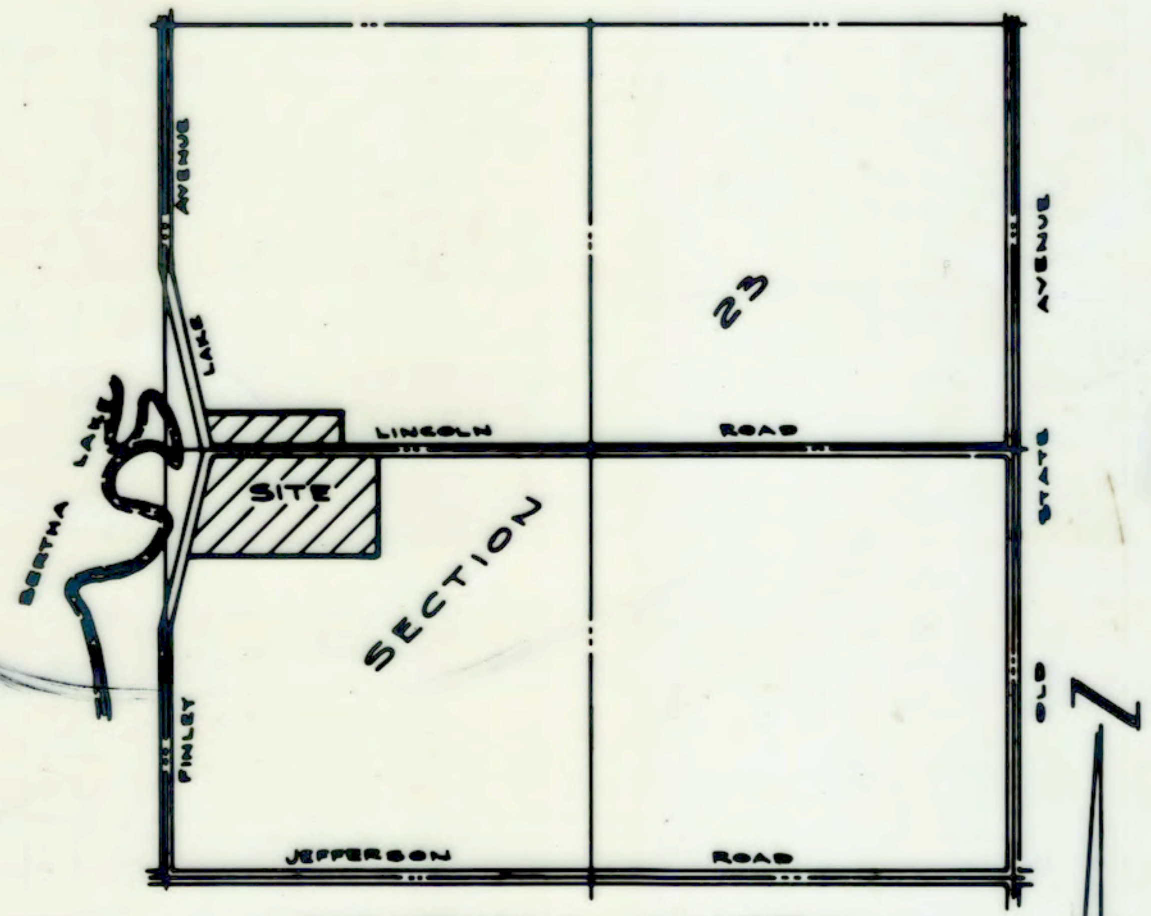

LOCATION SKETCH
NO SCALE

CURVE DATA

	LENGTH	RADIUS	DELTA	TANGENT	LONG CHORD
1.	254.04'	516.58'	28° 10' 39"	129.65'	S 03° 00' 19" W 251.49'
2.	101.20'	576.58'	10° 03' 23"	50.73'	S 12° 03' 57" W 101.07'
3.	96.15'	576.58'	09° 33' 16"	48.19'	S 06° 18' 23" E 96.04'

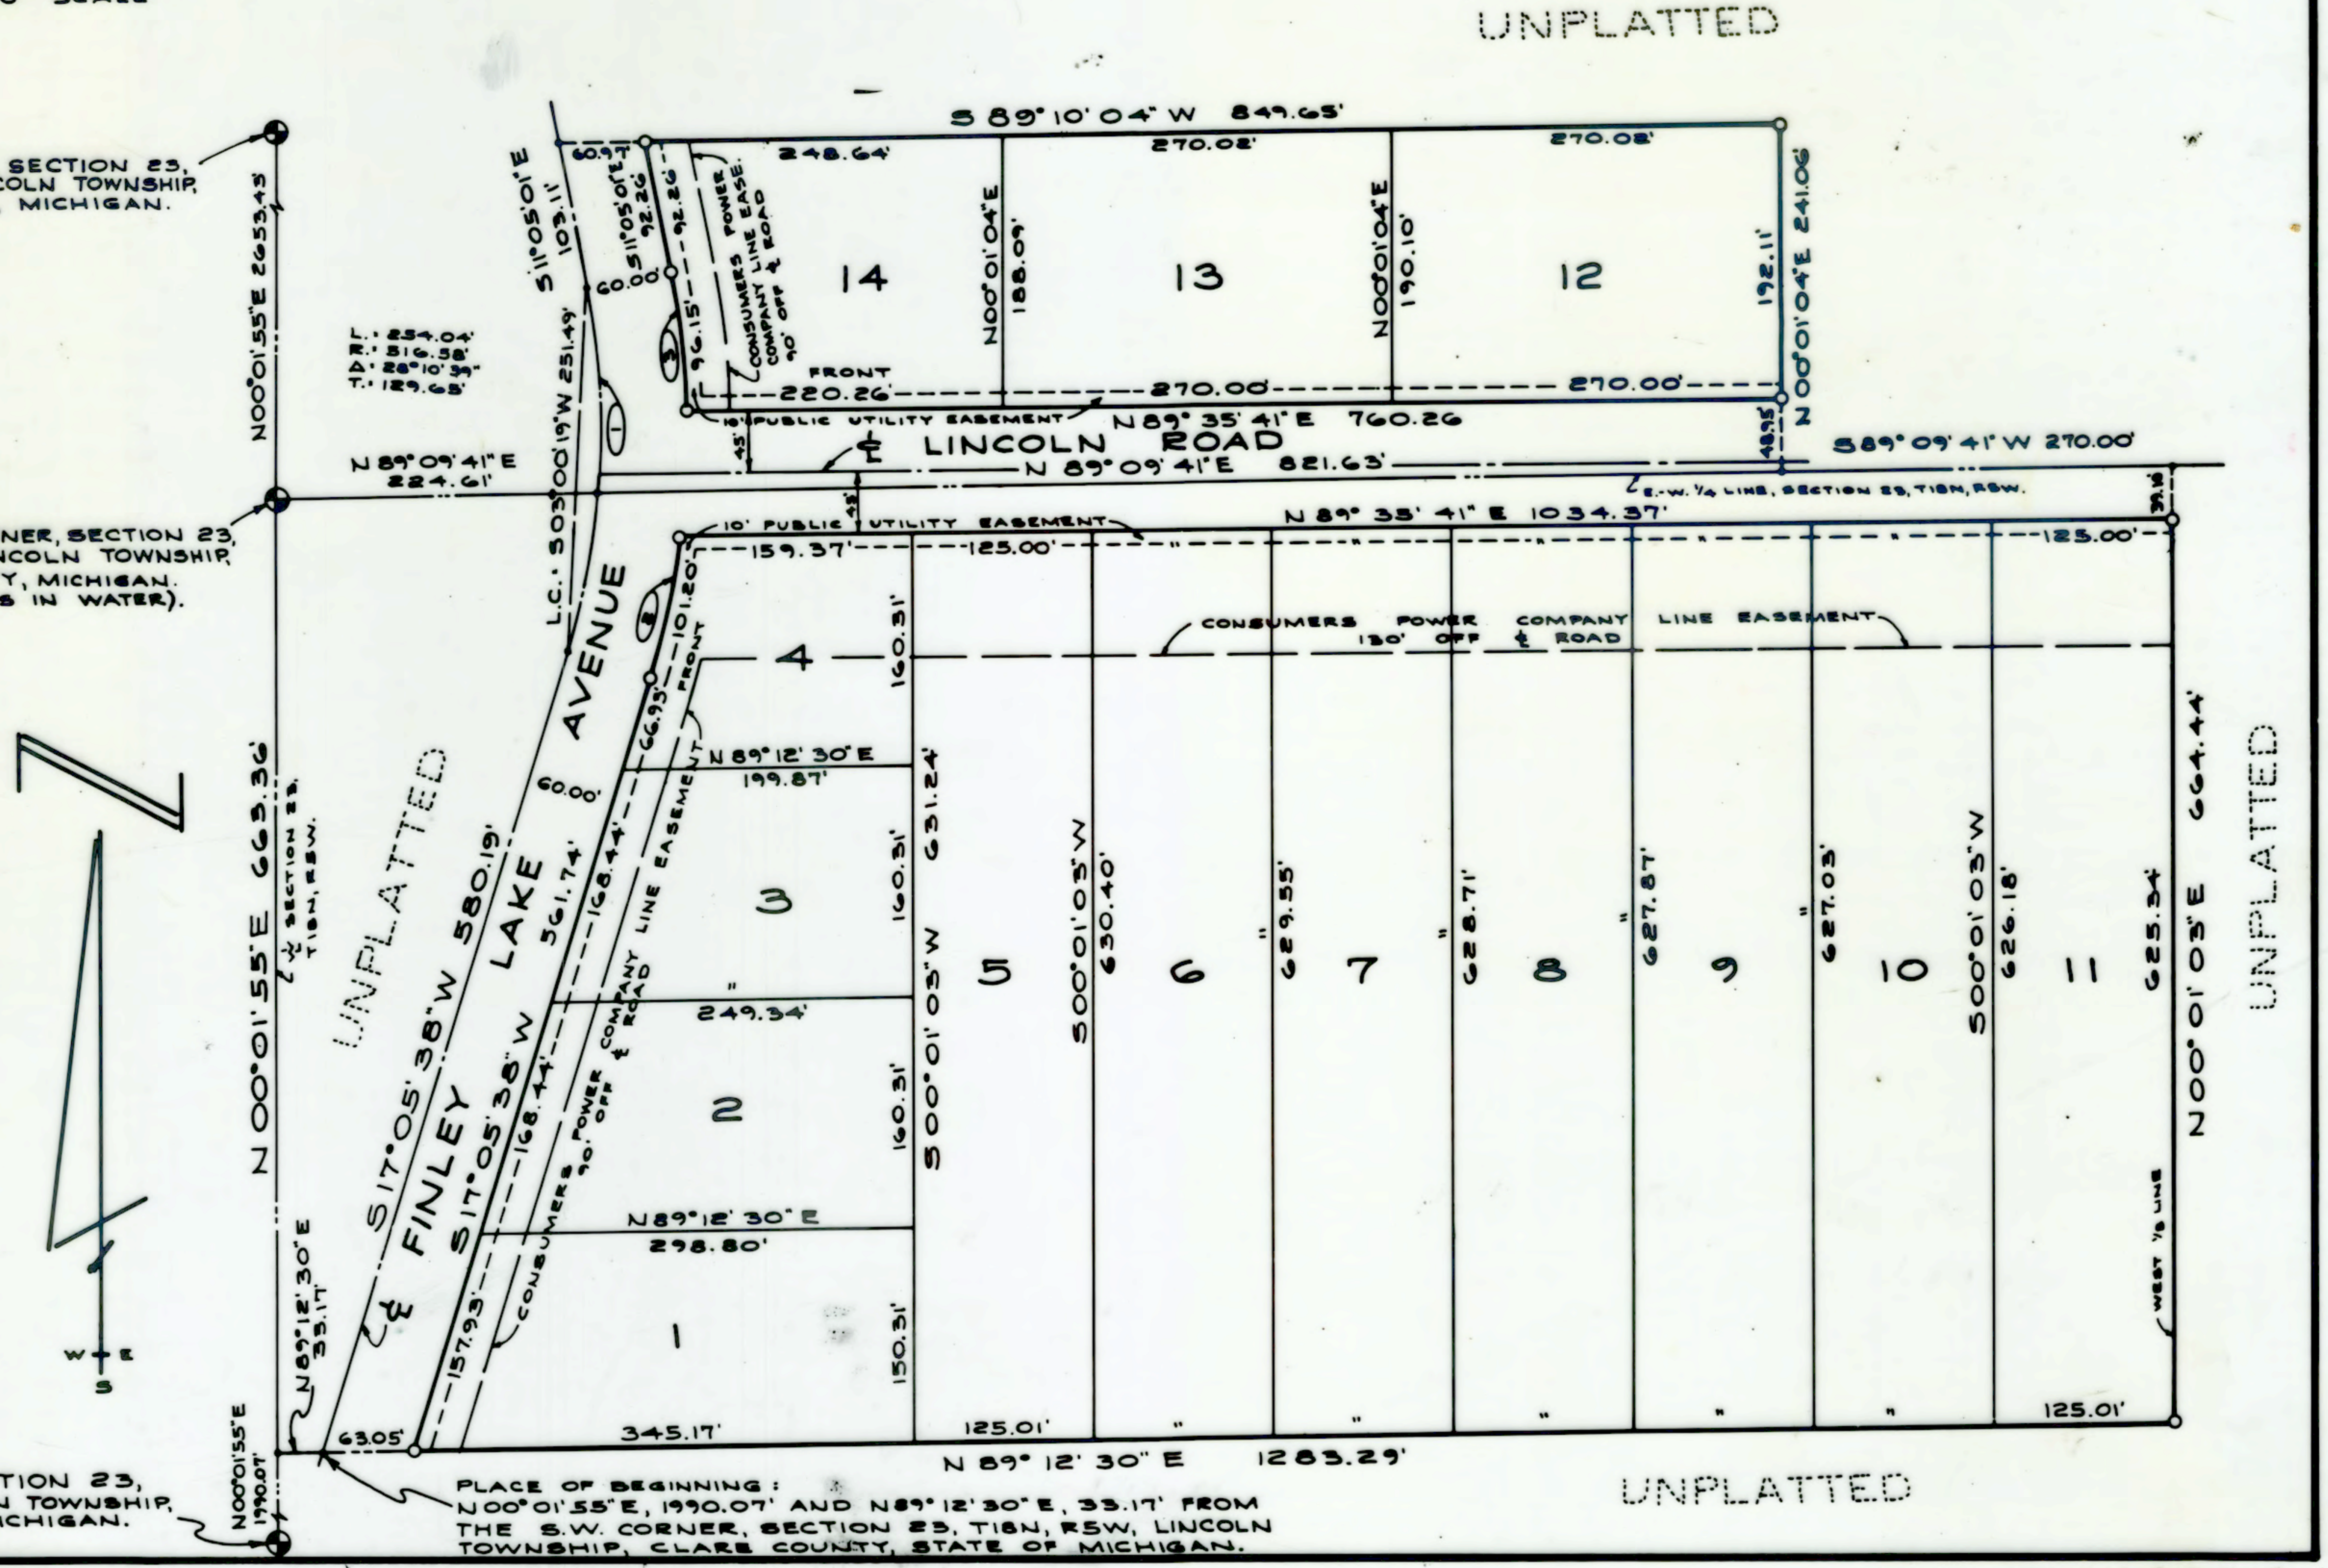

N.W. CORNER, SECTION 23,
T18N, R5W, LINCOLN TOWNSHIP,
CLARE COUNTY, MICHIGAN.

WEST 1/4 CORNER, SECTION 23,
T18N, R5W, LINCOLN TOWNSHIP,
CLARE COUNTY, MICHIGAN.
(CORNER FALLS IN WATER).

S.W. CORNER, SECTION 23,
T18N, R5W, LINCOLN TOWNSHIP,
CLARE COUNTY, MICHIGAN.

PLACE OF BEGINNING:
N00°01'55"E, 1990.07' AND N89°12'30"E, 33.17' FROM
THE S.W. CORNER, SECTION 23, T18N, R5W, LINCOLN
TOWNSHIP, CLARE COUNTY, STATE OF MICHIGAN.

LEGEND:

1. ALL DIMENSIONS ARE IN FEET.
2. CONCRETE MONUMENTS HAVE BEEN PLACED AT ALL POINTS MARKED "O".
3. ALL LOT CORNERS HAVE BEEN MARKED WITH 1/2" IRON BARS 18" IN LENGTH.
4. CURVE DIMENSIONS ARE ARC LENGTHS.
5. BEARINGS WERE ESTABLISHED FROM JEFFERSON ROAD - FINLEY LAKE AVENUE COUNTY ROAD PLANS - DECEMBER 1966.

HILLIARD HILLS

Part of the West 1/2 of the West 1/2 of Section 23, T18N, R5W, Lincoln Township, Clare County, State of Michigan.

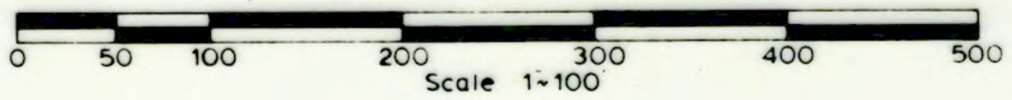

SURVEYOR'S CERTIFICATE

I, PAUL B. LAPHAM, SURVEYOR, CERTIFY:

THAT I HAVE SURVEYED, DIVIDED AND MAPPED THE LAND SHOWN ON THIS PLAT, DESCRIBED AS FOLLOWS: "HILLIARD HILLS, PART OF THE WEST ½ OF THE WEST ½ OF SECTION 23, T 18 N, R 5 W, LINCOLN TOWNSHIP, CLARE COUNTY, STATE OF MICHIGAN", BEGINNING N 00° 01' 55" E, ALONG THE WEST SECTION LINE, 1990.07 FEET AND N 89° 12' 30" E, 33.17 FEET FROM THE SOUTHWEST CORNER OF SAID SECTION 23; THENCE CONTINUING N 89° 12' 30" E, 1283.29 FEET TO THE WEST ONE-EIGHTH LINE; THENCE N 00° 01' 03" E, ALONG SAID WEST ONE-EIGHTH LINE, 664.44 FEET TO THE EAST-WEST ONE-QUARTER LINE; THENCE S 89° 09' 41" W, ALONG SAID EAST-WEST ONE-QUARTER LINE, 270.00 FEET; THENCE N 00° 01' 04" E, PARALLEL TO THE WEST ONE-EIGHTH LINE, 241.06 FEET; THENCE S 89° 10' 04" W, PARALLEL TO THE NORTH ONE-EIGHTH LINE, 849.65 FEET TO THE CENTER LINE OF FINLEY LAKE AVENUE; THENCE ALONG SAID CENTER LINE OF FINLEY LAKE AVENUE ON THE FOLLOWING THREE COURSES, S 11° 05' 01" E, 103.11 FEET; THENCE 254.04 FEET ON A 516.58 FOOT RADIUS CURVE TO THE RIGHT, HAVING A DELTA OF 28° 10' 39", A TANGENT OF 129.65 FEET AND A LONG CHORD BEARING S 03° 00' 19" W, 251.49 FEET; THENCE S 17° 05' 38" W, 580.19 FEET BACK TO THE PLACE OF BEGINNING. CONTAINING 14 LOTS.

THAT I HAVE MADE SUCH SURVEY, LAND-DIVISION AND PLAT BY THE DIRECTION OF THE OWNERS OF SUCH LAND.

THAT SUCH PLAT IS A CORRECT REPRESENTATION OF ALL THE EXTERIOR BOUNDARIES OF THE LAND SURVEYED AND THE SUBDIVISION OF IT.

THAT THE REQUIRED MONUMENTS AND LOT MARKERS HAVE BEEN LOCATED IN THE GROUND OR THAT SURETY HAS BEEN DEPOSITED WITH THE MUNICIPALITY, AS REQUIRED BY SECTION 125 OF THE ACT.

THAT THE ACCURACY OF SURVEY IS WITHIN THE LIMITS REQUIRED BY SECTION 126 OF THE ACT.

THAT THE BEARINGS SHOWN ON THE PLAT ARE EXPRESSED AS REQUIRED BY SECTION 126(3) OF THE ACT AND AS EXPLAINED IN THE LEGEND.

10-10-75
DATE

PAUL B. LAPHAM & ASSOCIATES, INC.
631 WEST U.S. 10, CLARE, MICHIGAN 48617

Paul B Lapham
PAUL B. LAPHAM R.L.S. NO. 9433 PRESIDENT

PAUL B. LAPHAM
LAND SURVEYOR
No. 9433

PROPRIETOR'S CERTIFICATE

WE AS PROPRIETORS CERTIFY THAT WE CAUSED THE LAND EMBRACED IN THIS PLAT TO BE SURVEYED, DIVIDED, MAPPED AND DEDICATED AS REPRESENTED ON THIS PLAT AND THAT FINLEY LAKE AVENUE AND LINCOLN ROAD ARE FOR THE USE OF THE PUBLIC; THAT THE PUBLIC UTILITY EASEMENTS ARE PRIVATE EASEMENTS AND THAT ALL OTHER EASEMENTS ARE FOR THE USES SHOWN ON THE PLAT.

WITNESS

Frances M. Lodes
FRANCES M. LODES

Donald G. Richmond, Jr.
DONALD G. RICHMOND, JR.

Rev. Charles E. Hilliard
REV. CHARLES E. HILLIARD, 7047 COLONVILLE ROAD
CLARE, MICHIGAN 48617

Ruth Ann Hilliard
RUTH ANN HILLIARD, 7047 COLONVILLE ROAD
CLARE, MICHIGAN 48617

ACKNOWLEDGEMENT

STATE OF MICHIGAN }
} S.S.
CLARE COUNTY }

PERSONALLY CAME BEFORE ME THIS 20th DAY OF Oct., 1975, THE ABOVE NAMED REV. CHARLES E. HILLIARD AND RUTH ANN HILLIARD, HIS WIFE, TO ME KNOWN TO BE THE PERSONS WHO EXECUTED THE FOREGOING INSTRUMENT AND ACKNOWLEDGED THAT THEY EXECUTED THE SAME AS THEIR FREE ACT AND DEED.

NOTARY PUBLIC Elva Lea Lapham
ELVA LEA LAPHAM

Clare COUNTY, MICHIGAN
CLARE

MY COMMISSION EXPIRES 10-1-77

COUNTY TREASURER'S CERTIFICATE

THE RECORDS IN MY OFFICE SHOW NO UNPAID TAXES OR SPECIAL ASSESSMENTS FOR THE FIVE YEARS PRECEDING November 4, 1975, INVOLVING THE LANDS INCLUDED IN THIS PLAT.

Clare
CLARE COUNTY, MICHIGAN

Ellen Ulch
ELLEN ULCH COUNTY TREASURER

COUNTY DRAIN COMMISSIONER'S CERTIFICATE

APPROVED ON November 25, 1975 AS COMPLYING WITH SECTION 192 OF ACT 288, P.A. 1967 AND THE APPLICABLE RULES AND REGULATIONS PUBLISHED BY MY OFFICE IN THE COUNTY OF CLARE.

Mortimer Shea
MORTIMER SHEA DRAIN COMMISSIONER

CERTIFICATE OF COUNTY ROAD COMMISSIONERS

APPROVED ON 12-3-75 AS COMPLYING WITH SECTION 183 OF ACT 288, P.A. 1967 AND THE APPLICABLE PUBLISHED RULES AND REGULATIONS OF THE BOARD OF ROAD COMMISSIONERS OF CLARE COUNTY.

Howard E. Eaton
HOWARD E. EATON CHAIRMAN

Norman V. Myers
NORMAN V. MYERS VICE CHAIRMAN

Donald L. Armentrout
DONALD L. ARMENTROUT MEMBER

CERTIFICATE OF MUNICIPAL APPROVAL

I CERTIFY THAT THIS PLAT WAS APPROVED BY THE TOWNSHIP BOARD, OF THE TOWNSHIP OF LINCOLN, AT A MEETING HELD December 8, 1975 AND WAS REVIEWED AND FOUND TO BE IN COMPLIANCE WITH ACT 288, P.A. OF 1967. THIS PLAT WAS APPROVED BY THE CLARE COUNTY HEALTH DEPARTMENT ON AUGUST 21, 1975.

Sally Smith Clerk
SALLY SMITH CLERK

COUNTY PLAT BOARD CERTIFICATE

THIS PLAT HAS BEEN REVIEWED AND IS APPROVED BY THE CLARE COUNTY PLAT BOARD ON January 8, 1976, AS BEING IN COMPLIANCE WITH ALL OF THE PROVISIONS OF ACT. 288, P.A. 1967, AND THE PLAT BOARD'S APPLICABLE RULES AND REGULATIONS.

Louis W. Becker
LOUIS W. BECKER
REGISTER OF DEEDS

L. Thomas Bradley
L. THOMAS BRADLEY
CHAIRMAN OF BOARD OF COUNTY COMMISSIONERS

Ellen Ulch
ELLEN ULCH
COUNTY TREASURER

RECORDING CERTIFICATE

STATE OF MICHIGAN }
} S.S.
CLARE COUNTY }

THIS PLAT WAS RECEIVED FOR RECORD ON THE 16th DAY OF MARCH, 19 76 AT 3:15 P. M, AND RECORDED IN LIBER 15 OF PLATS ON PAGES 23;24.

s/s Louis W. Becker
LOUIS W. BECKER REGISTER OF DEEDS

Certified true copy of Recorded plat

Allison Green
ALLISON GREEN
STATE TREASURER

By Richard E. Lomax/jio
Richard E. Lomax - Plat Examiner
Date March 18, 1976