# HOLMES DEVELOPMENT NO.1

Part of the Southwest One-quarter of the Southeast One-quarter of Section 7, T 18 N, R 5 W, Lincoln Township, Clare County, Michigan.

## DEDICATION

KNOW ALL MEN BY THESE PRESENTS, That we, Allen W. Holmes, and Alice Holmes, his wife, as proprietors, have caused the land embraced in the annexed plat to be surveyed, laid-out and platted, to be known as "HOLMES DEVELOPMENT NO. 1, Part of the Southwest one-quarter of the Southeast one-quarter of Section 7, T 18 N, R 5 W, Lincoln Township, Clare County, Michigan.", and that the Drives, as shown on said plat are hereby dedicated to the use of the public, and that the Private Alley, Mary's Lane, is hereby dedicated to the use of the property owners, and that the Private Utility Easements as shown on said plat shall be in accordance with Act 131, Public Acts of 1953, as amended.

Witnesses: Paul B. Lapham (Paul B Lapham) — Signed: Allen W. Holmes (Allen W. Holmes)

John Meyers (John Meyers) — Alice Holmes (Alice Holmes)

STATE OF MICHIGAN )
County of Clare ) ss

On this 8 day of AUGUST 1963, before me, a Notary Public, in and for said county, personally came the above named Allen W. Holmes and Alice Holmes, his wife, known to me to be the persons who executed the above dedication and acknowledged the same to be their free act and deed.

Elva Lea Lapham (Elva Lea Lapham)
Notary Public, Clare County, Mich.

My commission expires 12-12-66

## DESCRIPTION OF LAND PLATTED

The land embraced in the annexed plat of "HOLMES DEVELOPMENT NO.1, Part of the Southwest one-quarter of the Southeast one-quarter of Section 7, T 18 N, R 5 W, Lincoln Township, Clare County, Michigan.", is described as follows: Beginning N 01° 33' 40" E, 330.0 feet from the South ¼ corner of Section 7, T 18 N, R 5 W, Lincoln Township, Clare County, Michigan; thence, N 01° 33' 40" E, 420.0 feet; thence, S 89° 04'40"E, 157.41 feet; thence, S 01° 33' 40" W, 120.0 feet; thence, S 89°04'40"E, 693.0 feet; thence, N 01° 21' 20" E, 377.00 feet; thence,S 89°53'40"E, 468.35 feet; thence, S 01° 21' 20" W, 683.65 feet; thence,N 89°04'40"W, 1319.82 feet; back to the place of beginning. Containing 51 numbered lots.

## CERTIFICATE OF MUNICIPAL APPROVAL

This plat was approved by the Township Board of the Township of Lincoln at a meeting held Oct 7 1963, and complies with Section 19A and the width of lots is in compliance with requirements of Section 30, Act 172, of 1929, as amended.

Howard Ryckman
Howard Ryckman, Clerk

## CERTIFICATE OF APPROVAL BY BOARD OF COUNTY ROAD COMMISSIONERS

This plat has been examined and was approved on the 16th day of October 1963, by the Clare County Board of Road Commissioners.

Norman V. Myers, Chairman

Fred Jones, Member

Glenn Lloyd, Member

COPY

Register's Office } S. S.
Clare County.

Plat of Holmes Development No. 1 was Recorded this 13th day of Dec. A.D., 19 63 at 1:30 o'clock P M, in Liber 7 of plats on Page 21

Wm. A. Henderson
Register of Deeds

ORIGINAL ON FILE

I hereby certify this copy is a true copy of map or plat forwarded the Register of Deeds for recording.
Date Dec. 12, 1963
FILED IN AUDITOR GENERAL'S DEPT.
Date Dec. 16, 1963
EXAMINED AND APPROVED
Date Dec. 12, 1963

Billie S. Farnum
BILLIE S. FARNUM
AUDITOR GENERAL
By Richard E. Lomax
Richard E. Lomax - Plat Examiner

## CERTIFICATE OF APPROVAL BY COUNTY BOARD

This plat was approved on the 14th day of November 1963 by the Clare County Plat Board.

Louis Becker — Bruce Williams

Louis Becker, Ch.of.Bd.of Supervisors — Bruce Williams, Drain Commissioner

Wm.A. Henderson — Lewis F. Rutter

Wm.A. Henderson, Reg.of Deeds — Lewis F. Rutter, Treasurer

## COUNTY TREASURER'S CERTIFICATE RELATING TO TAXES

Office of County Treasurer
Clare County, Michigan.

I hereby certify that there are no tax liens or titles held by the State on the lands described hereon, and that there are no tax liens or titles held by individuals on said lands for the five years preceeding the 14 day of Nov 1963, and that the taxes for said period of five years are paid, as shown by the records of this office. This certificate does not apply to taxes, if any, now in the process of collection by township, city or village collecting officers.

Lewis F. Rutter
Lewis F. Rutter, Treasurer

## SURVEYOR'S CERTIFICATE


I hereby certify that the plat hereon delineated is a correct one and that permanent metal monuments consisting of bars not less than one-half inch in diameter and 36 inches in length, encased in a concrete cylinder at least four inches in diameter and 36 inches in depth, have been placed at points marked thus (o) as thereon shown at all angles in the boundaries of the land platted, at all intersections of streets, intersections of alleys, or of streets and alleys, and at the intersections of streets and alleys with the boundaries of the plat as shown on said plat.

Paul B. Lapham
Paul B. Lapham
Registered Surveyor No.9433

ALL DIMENSIONS ARE IN FEET AND DECIMALS

0 100 200 300 400 500

SCALE 1" = 100'

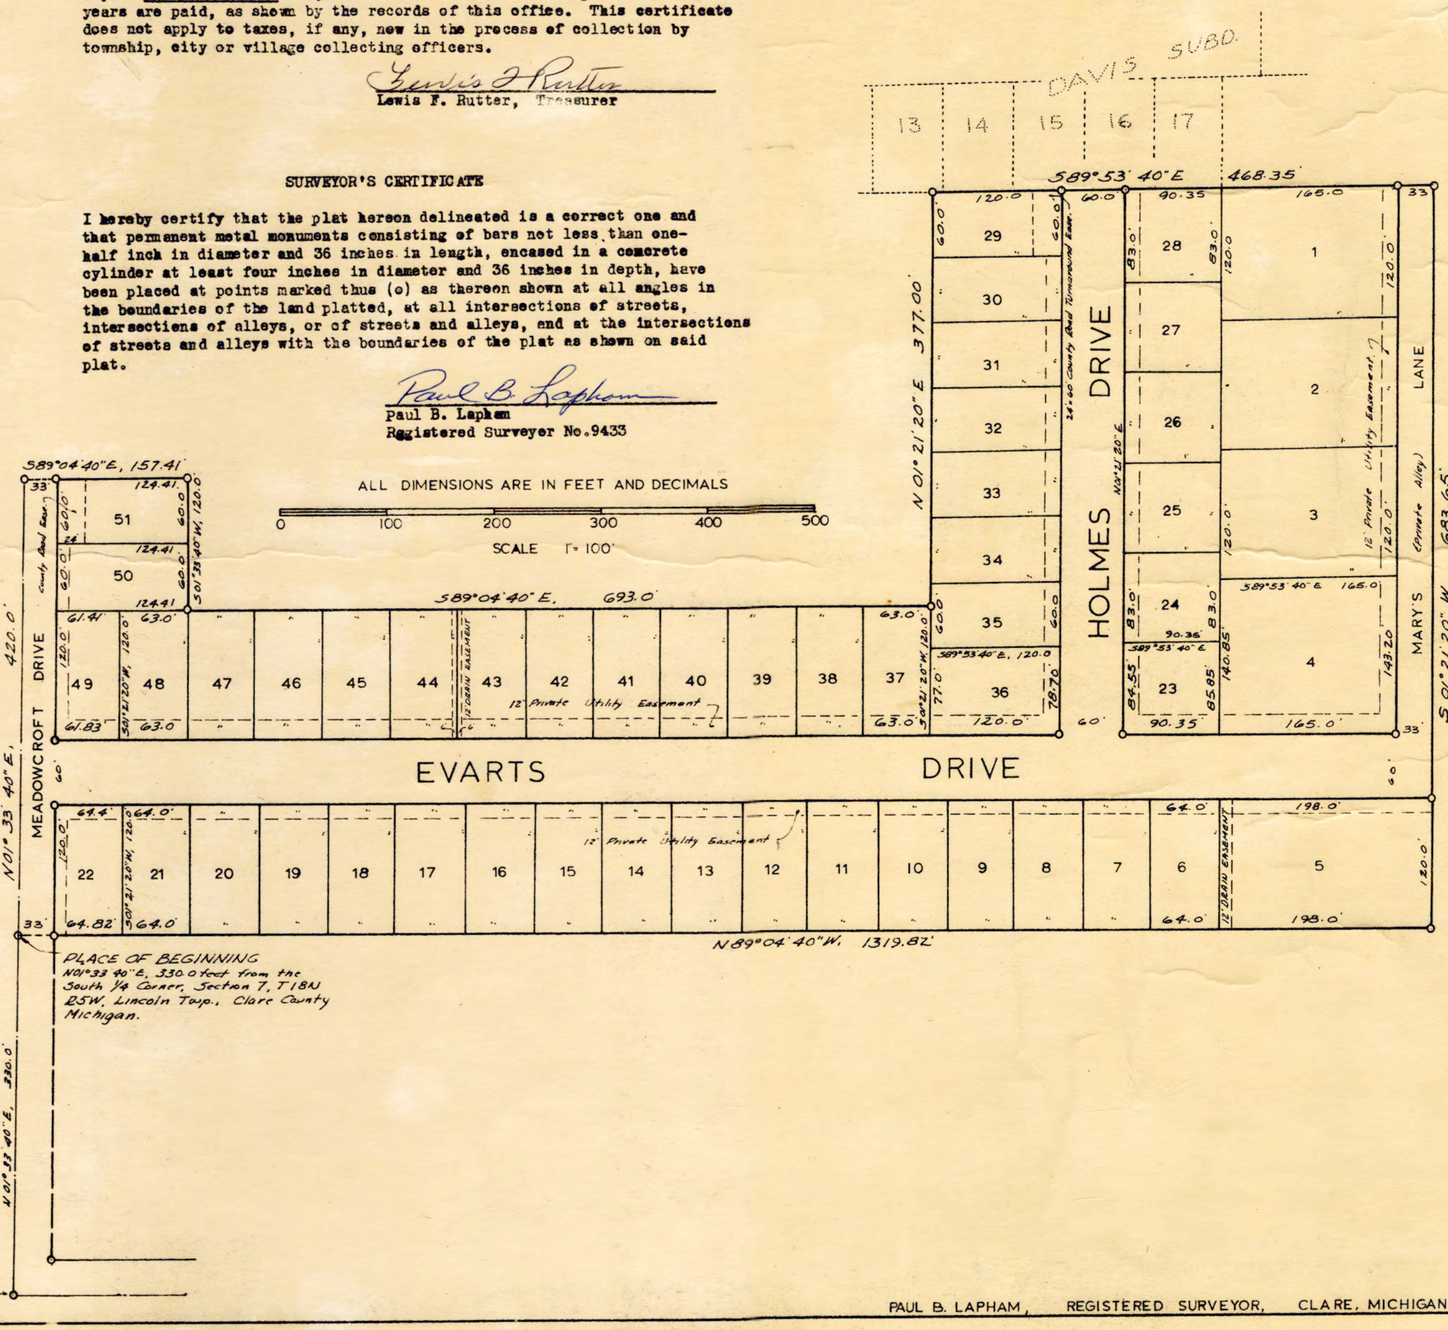


PAUL B. LAPHAM, REGISTERED SURVEYOR, CLARE, MICHIGAN