COPY.

PLAT OF "LAKE WOOD SUBDIVISION."

On and part of Govt Lot 3 Section 8 and Govt Lot 1 Section 17
T.18.N.R.5.W. Clare Co. Michigan.

DEDICATION

KNOW ALL MEN BY THESE PRESETS, That I Ella M. McCray as proprietor have caused the land embraced in the annexed plat to be surveyed laid out and platted to be known as "Lake Wood Subdivision" being on and part of Govt Lot 3 Section 8 and Govt Lot 1 Section 17. T.18.N.R.5.W. Clare Co. Michigan. and that the streets and alleys as shown on said plat are hereby dedicated to the use of the public.

Signed and sealed in presence of

Carolyn Plugge ---------- | ------ Ella M. McCray ------ [L.S]
P. E. Brown ---------- | ---------------------------- [L.S.]

STATE OF Indiana } ss.
County of. Marion }

On this 11 day of August 1926 before me a Notary Public. in and for said County, personally came the above named Ella M. McCray known to me to be the person who executed the above dedication. and acknowledged the same to be her free act and deed.

Adale C. Bush.

Notary Public. Marion Co Indiana

My Commission expires June 24 1928

DESCRIPTION.

Commencing at a point 10 chains S and 19.14 chains E. of 1/8 post at the N.W. corner of Govt Lot 3 Section 8 T.18.N.R.5.W. Clare Co. Michigan. Proceeding thence S. 12° 30' E. 1805 feet. Thence S. 87°E. 726 feet. Thence N. 24°W 200 feet. Thence N. 13° 30' W. 200 feet. Thence N 5°E 139 feet. Thence N. 30° 30' W 110 feet.' Thence N. 5° 30' W. 125 feet. Thence. N 45° 30' W. 421 feet. Thence N 35° 30' W. 187 feet. Thence N. 9° W. 218 feet. Thence N. 18° 30' W 271 feet. Thence N. 43° W 193 feet. Thence N. 87° W. 286.5 feet. To place of beginning The entire plat being on and part of Govt Lot 3 Section 8 and Govt Lot 1 Section 17.

Sept 8-1926
Jno. L. Haun

CERTIFICATE OF MUNICIPAL APPROVAL.

This plat was approved by the Township Board of the Township of Lincoln at a meeting held. ---- Aug 21 ---------- 1926

Harry Davis ----
Clerk.

CERTIFICATE OF APPROVAL BY COUNTY BOARD.

This plat was approved on the 3rd day of ------ September ------ 1926

Thomas S. Dorsey - Judge of Probate
Emma Hoag County Clerk
Fred W. Schaaf County Treasurer

I HEREBY CERTIFY, That there are no tax liens or titles held by the State on the lands described in this instrument and that there are no tax liens or titles held by individual on the said lands, and that the taxes on said lands for the five years preceding the date of said instrument are all paid, as shown by the records of this office.

Harrison, Mich. Sept. 3. 1926.

Fred W. Schaaf County Treasurer

SURVEYORS CERTIFICATE.

I hereby certify that the plat hereon delineated is a correct one and that permanent metal monuments, of not less than one inch in diameter and fifteen inches in length, set in a concrete base at least four inches in diameter and forty-eight inches in depth have been placed at points marked thus (o) as thereon shown at all angles in the boundaries of the land platted, at all the intersections of streets, intersection of alleys, or of streets and alleys, and at the intersections of streets and alleys with the boundaries of the plat as shown on said plat.

------ Arthur J. Johnson ------

Registered Civil Engineer

Date of survey July 1926

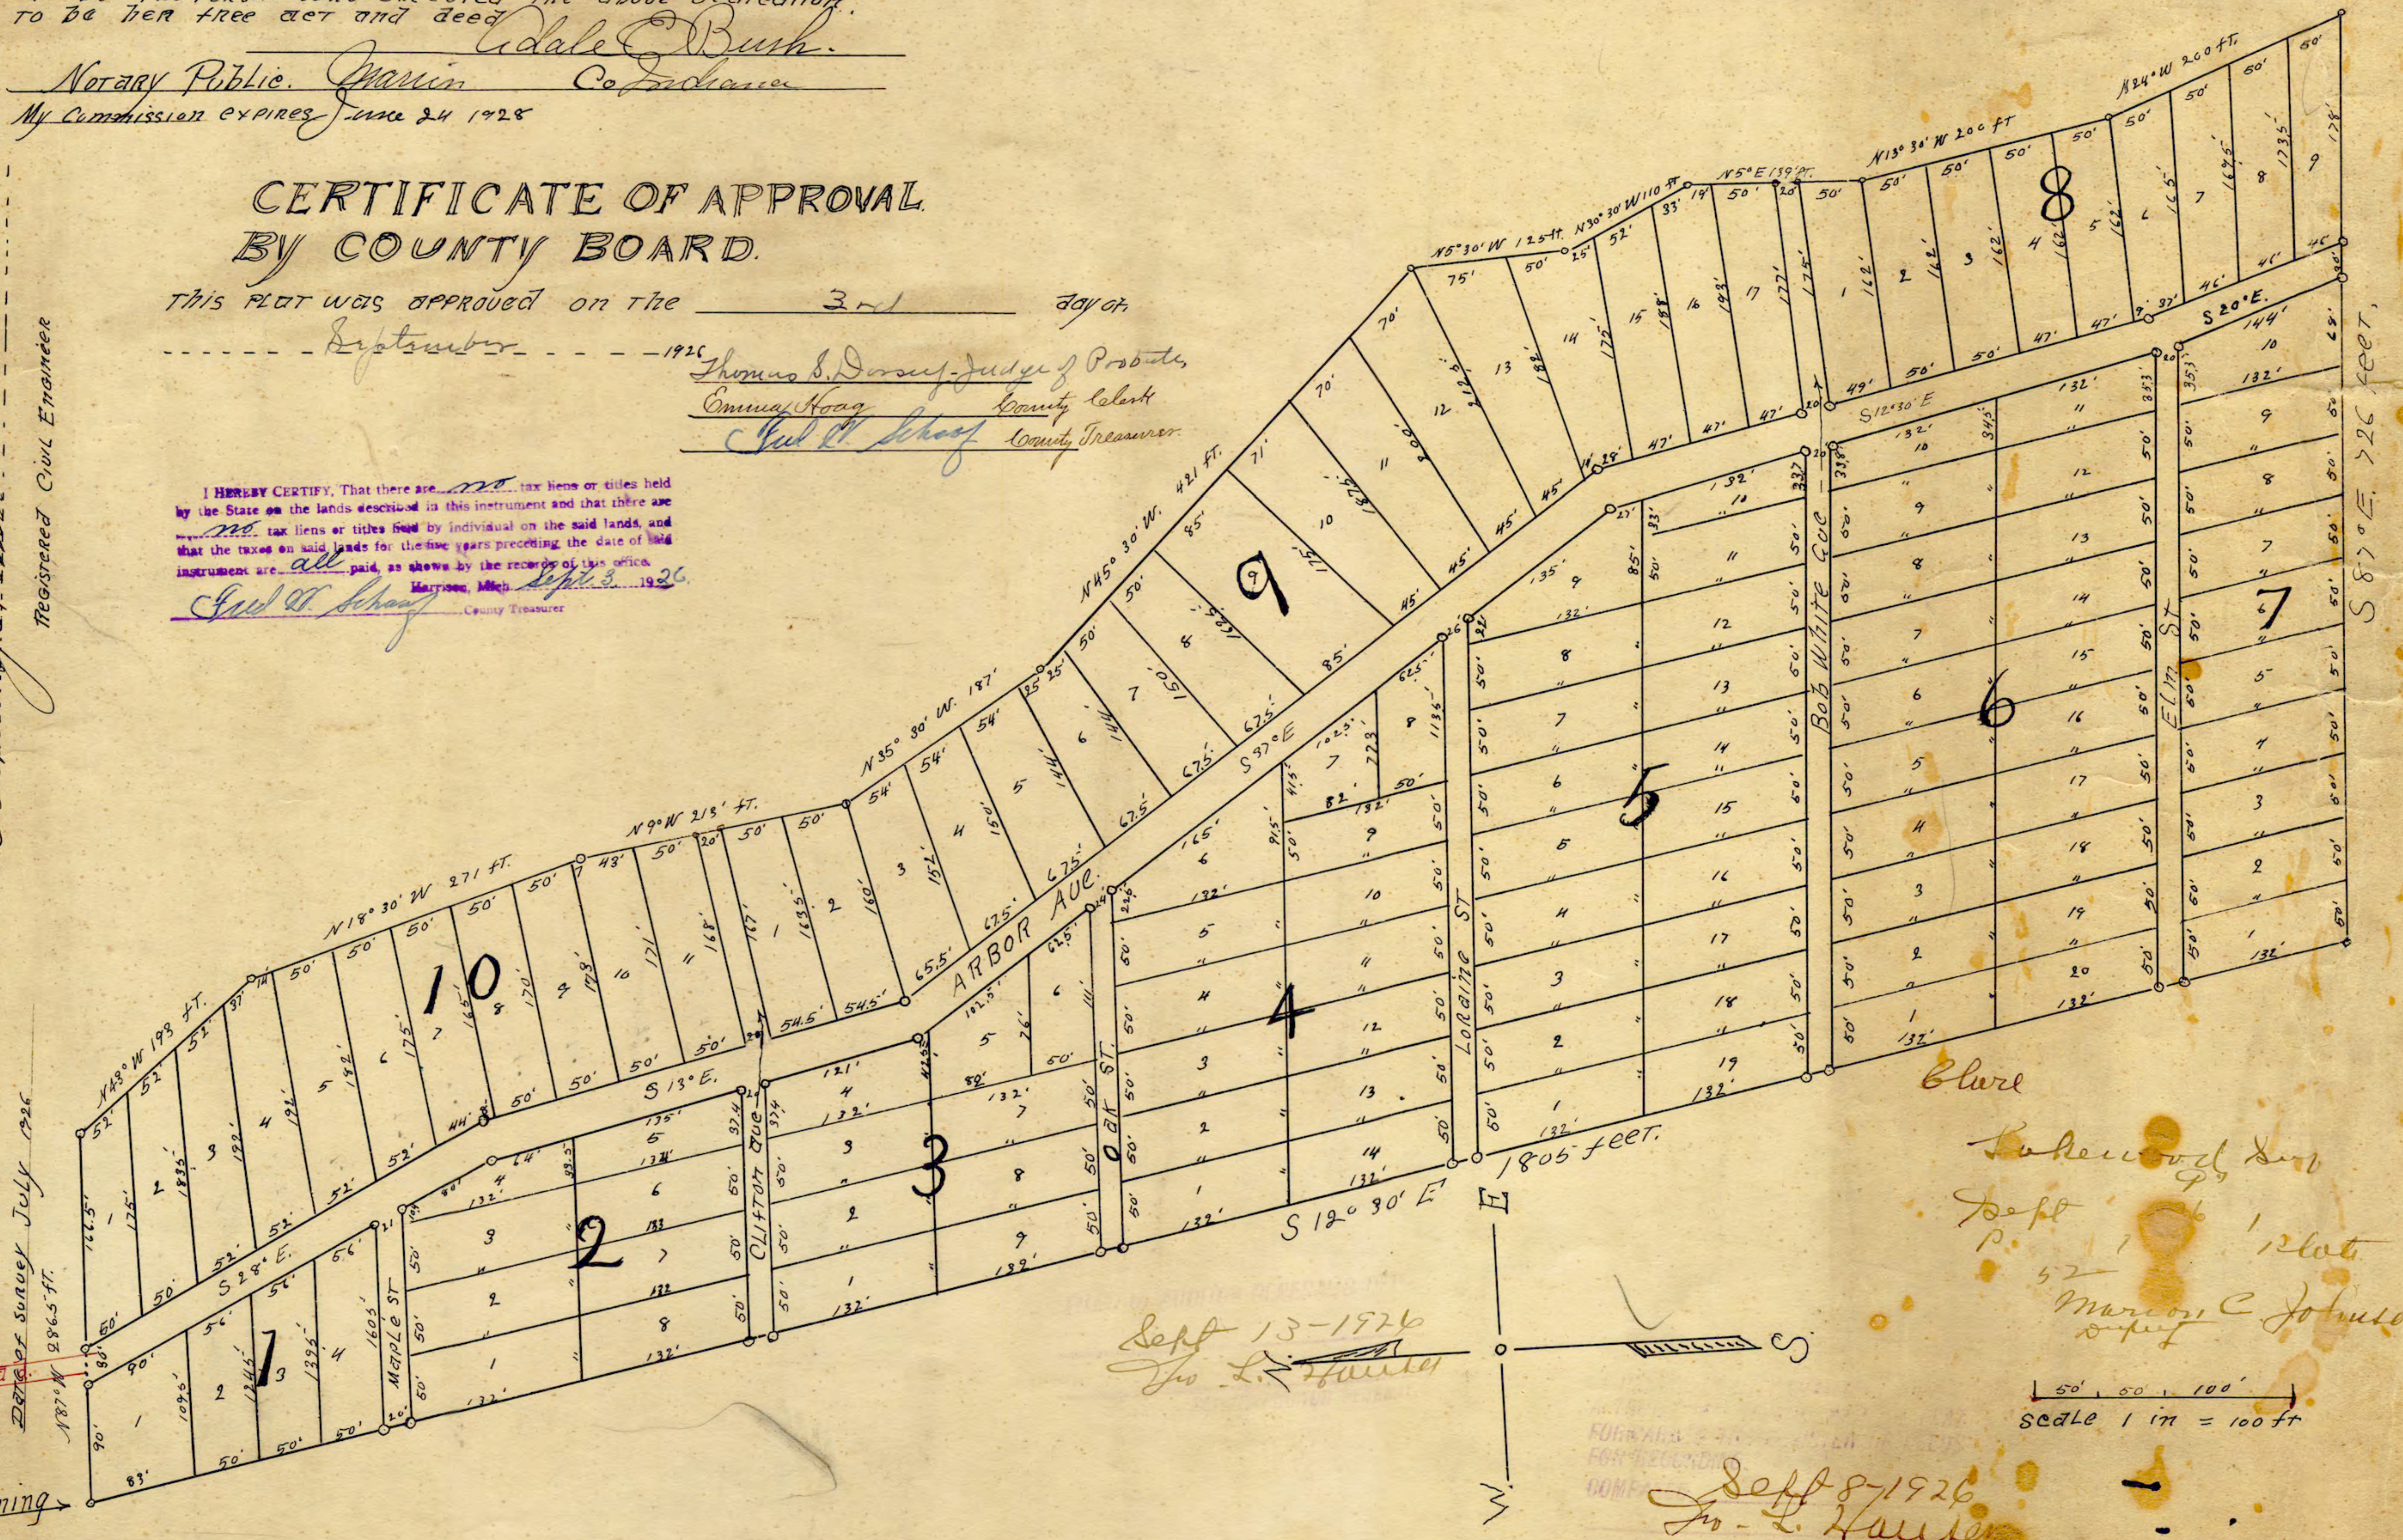

Place of beginning

Sept 13-1926
Jno. L. Haun

Clare

Lakewood Sub
Sept 1926
P. 1 Plats
52
Marion C. Johnson
Deputy

50' 50' 100'
scale 1 in = 100 ft

Sept 8-1926
Jno. L. Haun