
# ASSESSOR'S PLAT OF LINCOLN NO. 1


Part of Government Lot 5, Section 16, T18N, R5W, Lincoln Township,
Clare County, State of Michigan.

0 50' 100' 200' 300' 400'
Scale: 1"=60'

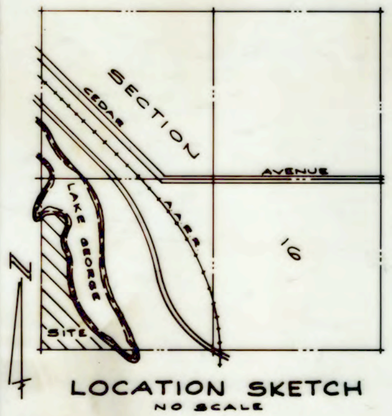


LOCATION SKETCH
NO SCALE

LEGEND:
1. ALL DIMENSIONS ARE IN FEET.
2. CONCRETE MONUMENTS HAVE BEEN PLACED AT ALL POINTS MARKED "O".
3. ALL LOT CORNERS HAVE BEEN MARKED WITH ½" IRON BARS 18" IN LENGTH.
4. BEARINGS WERE ESTABLISHED FROM THE NORTH PLAT LINE OF "WIGWAH TRAILS SUBDIVISION NUMBER 1" AS RECORDED IN LIBER 6 OF PLATS ON PAGE 1.
5. LOTS EXTEND TO THE WATERS EDGE.

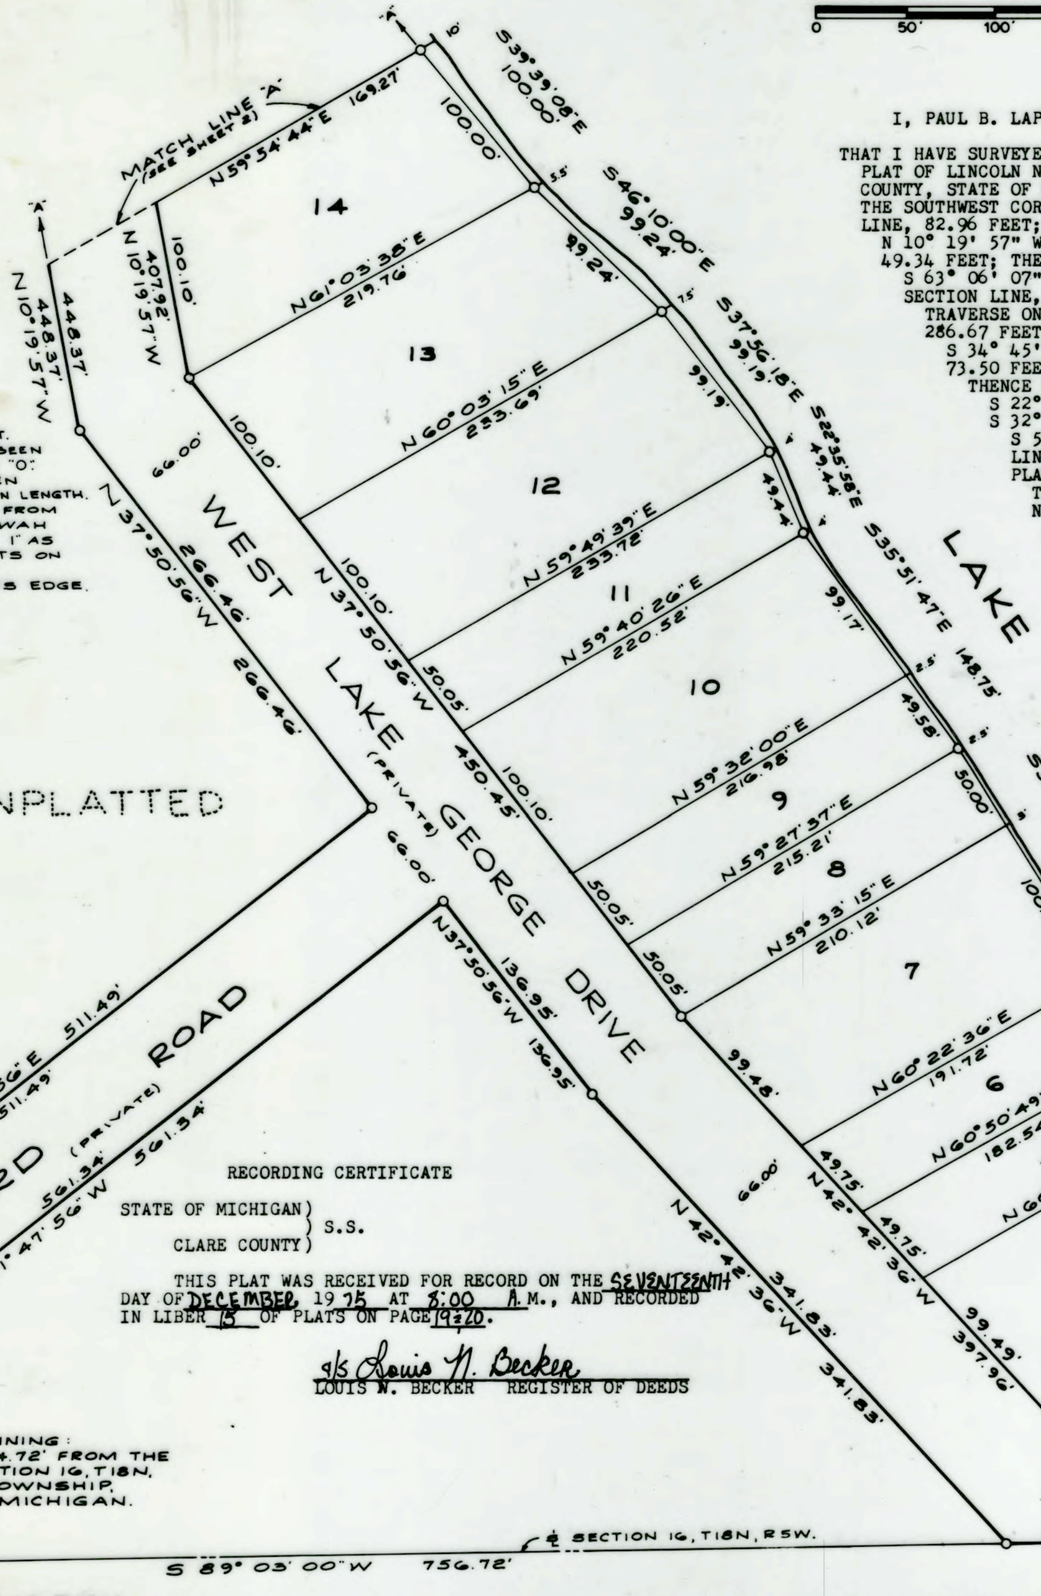


SURVEYOR'S CERTIFICATE

I, PAUL B. LAPHAM, SURVEYOR, CERTIFY:

THAT I HAVE SURVEYED, DIVIDED AND MAPPED THE LAND SHOWN ON THIS PLAT, DESCRIBED AS FOLLOWS: "ASSESSOR'S PLAT OF LINCOLN NO. 1, PART OF GOVERNMENT LOT 5, SECTION 16, T 18 N, R 5 W, LINCOLN TOWNSHIP, CLARE COUNTY, STATE OF MICHIGAN," BEGINNING N 00° 55' 09" W, ALONG THE WEST SECTION LINE, 24.72 FEET FROM THE SOUTHWEST CORNER OF SAID SECTION 16; THENCE CONTINUING N 00° 55' 09" W, ALONG SAID WEST SECTION LINE, 82.96 FEET; THENCE N 51° 47' 56" E, 511.49 FEET; THENCE N 37° 50' 56" W, 266.46 FEET; THENCE N 10° 19' 57" W, 448.37 FEET; THENCE N 30° 04' 51" E, 206.54 FEET; THENCE N 33° 25' 10" W, 49.34 FEET; THENCE N 59° 49' 50" W, 157.81 FEET; THENCE N 06° 13' 42" W, 135.12 FEET; THENCE S 63° 06' 07" W, 117.65 FEET TO THE WEST SECTION LINE; THENCE N 00° 55' 09" W, ALONG SAID WEST SECTION LINE, 300.00 FEET TO A SHORE LINE TRAVERSE OF LAKE GEORGE; THENCE ALONG SAID SHORE LINE TRAVERSE ON THE FOLLOWING 17 COURSES: N 53° 44' 41" E, 409.50 FEET; THENCE S 47° 46' 14" E, 286.67 FEET; THENCE S 19° 56' 23" W, 274.01 FEET; THENCE S 27° 04' 14" E, 104.84 FEET; THENCE S 34° 45' 28" E, 215.97 FEET; THENCE S 28° 27' 45" W, 281.64 FEET; THENCE S 33° 13' 24" W, 73.50 FEET; THENCE S 04° 42' 01" E, 122.77 FEET; THENCE S 39° 39' 08" E, 100.00 FEET; THENCE S 46° 10' 00" E, 99.24 FEET; THENCE S 37° 56' 18" E, 99.19 FEET; THENCE S 22° 35' 58" E, 49.44 FEET; THENCE S 35° 51' 47" E, 148.75 FEET; THENCE S 32° 00' 04" E, 215.45 FEET; THENCE S 51° 36' 49" E, 234.55 FEET; THENCE S 57° 14' 17" E, 116.24 FEET; THENCE S 69° 44' 46" E, 125.00 FEET TO THE SOUTH SECTION LINE AND THE NORTH LINE OF WIGWAH TRAILS SUBDIVISION NO. 1, AS RECORDED IN LIBER 6 OF PLATS ON PAGE 1, CLARE COUNTY, MICHIGAN PUBLIC RECORDS; THENCE LEAVING SAID SHORE LINE TRAVERSE S 89° 03' 00" W, ALONG SAID SOUTH SECTION LINE, 486.30 FEET; THENCE N 42° 42' 36" W, 341.83 FEET; THENCE N 37° 50' 56" W, 136.95 FEET; THENCE S 51° 47' 56" W, 561.34 FEET BACK TO THE PLACE OF BEGINNING. CONTAINING 23 LOTS AND 1 PRIVATE PARK.

THAT I HAVE MADE SUCH SURVEY, LAND DIVISION AND PLAT BY THE DIRECTION OF THE LINCOLN TOWNSHIP BOARD, ON JANUARY 13, 1975.

THAT SUCH PLAT IS A CORRECT REPRESENTATION OF ALL THE EXTERIOR BOUNDARIES OF THE LAND SURVEYED AND THE SUBDIVISION OF IT.

THAT THE REQUIRED MONUMENTS AND LOT MARKERS HAVE BEEN LOCATED IN THE GROUND.

THAT THE ACCURACY OF SURVEY IS WITHIN THE LIMITS REQUIRED BY SECTION 126 OF THE ACT.

THAT THE BEARINGS SHOWN ON THE PLAT ARE EXPRESSED AS REQUIRED BY SECTION 126 (3) OF THE ACT AND AS EXPLAINED IN THE LEGEND.

STATE OF MICHIGAN · PAUL B. LAPHAM LAND SURVEYOR No. 9433 · REGISTERED LAND SURVEYOR

PAUL B. LAPHAM & ASSOCIATES, INC.
631 WEST U.S. 10
CLARE, MICHIGAN 48617

Paul B. Lapham
PAUL B. LAPHAM — PRINCIPAL
R.L.S. NO. 9433

April 18th 1975
DATE

RECORDING CERTIFICATE

STATE OF MICHIGAN )
CLARE COUNTY ) S.S.

THIS PLAT WAS RECEIVED FOR RECORD ON THE SEVENTEENTH DAY OF DECEMBER, 1975 AT 8:00 A.M., AND RECORDED IN LIBER 15 OF PLATS ON PAGE 19 & 20.

d/s Louis N. Becker
LOUIS N. BECKER REGISTER OF DEEDS

Certified true copy of Recorded plat

Allison Green
ALLISON GREEN
STATE TREASURER
By Richard E. Lomax/ps
Richard E. Lomax - Plat Examiner
Date December 19 1975

# ASSESSOR'S PLAT OF LINCOLN NO. 1

Part of Government Lot 5, Section 16, T18N, R5W, Lincoln Township,
Clare County, State of Michigan.

0 50 100 200 300 400
Scale 1"=60'

## ASSESSOR'S CERTIFICATE

I, AS SUPERVISOR, BY VIRTUE OF THE AUTHORITY VESTED IN SECTION 201 (2) ACT 288 OF P.A. OF 1967, HAVING BEEN DULY AUTHORIZED BY THE TOWNSHIP OF LINCOLN, CLARE COUNTY, STATE OF MICHIGAN, HAVE CAUSED THE LAND DESCRIBED IN THE ANNEXED PLAT TO BE SURVEYED, LAID OUT AND PLATTED AND CERTIFY THAT THE ROADS AS SHOWN ON THE PLAT HAVE BEEN ACQUIRED THROUGH ADVERSE POSSESSION FOR PRIVATE USE OF THE LOT OWNERS OF SAID PLAT AND THAT THE DRIVEWAY EASEMENT ACROSS LOT 19 HAS BEEN ACQUIRED BY ADVERSE POSSESSION AND IS PRIVATE FOR THE USE OF THE OWNERS OF LOTS 16-23 INCLUSIVE AND THAT BIRCH PARK IS A PRIVATE PARK FOR THE USE OF THE LOT OWNERS OF WIGWAH TRAILS SUBDIVISION NO. 1 AND THAT THE PLAT CONFORMS TO SECTIONS 201 THROUGH 213 OF ACT 288 OF P.A. OF 1967, AS AMENDED.

Allan A. Kowalk
ALLAN A. KOWALK

Helen A. Kowalk
HELEN A. KOWALK

W. C. McConica
W. C. McCONICA — SUPERVISOR
882 BRINGOLD ROAD
LAKE GEORGE, MICHIGAN 48633

## ACKNOWLEDGEMENT

STATE OF MICHIGAN)
)S.S.
COUNTY OF CLARE )

ON THIS 24 DAY OF Oct A.D. 1975, BEFORE ME PERSONALLY CAME THE ABOVE NAMED W. C. McCONICA, SUPERVISOR OF LINCOLN TOWNSHIP, KNOWN TO ME TO BE THE PERSON WHO EXECUTED THE ABOVE DEDICATION, AND ACKNOWLEDGED THE SAME TO BE HIS FREE ACT AND DEED AS SUCH SUPERVISOR.

Jeffrey Brian Smith
NOTARY PUBLIC IN AND FOR CLARE COUNTY.

MY COMMISSION EXPIRES: 2-11-79

## CERTIFICATE OF MUNICIPAL APPROVAL

THIS PLAT WAS APPROVED ON October 24, 1975, BY THE TOWNSHIP BOARD OF THE TOWNSHIP OF LINCOLN, AS HAVING BEEN MADE AND COMPLYING WITH THE REQUIREMENTS OF SECTION 201 AND 209 (4) OF P.A. 288 OF 1967.

Sally Smith
SALLY SMITH — CLERK

## CERTIFICATE OF COUNTY ROAD COMMISSION

THE BOARD OF COUNTY ROAD COMMISSIONERS OF THE COUNTY OF CLARE HEREBY CERTIFIES THAT THERE ARE NO PUBLIC ROADS ON THE PLAT. THIS CERTIFICATION IS MADE THIS August 20, 1975 IN ACCORDANCE WITH SECTION 209 (1) OF ACT 288 OF 1967.

Howard E. Eaton — CHAIRMAN
Norman V. Myers — VICE-CHAIRMAN
Donald L. Armentrout — MEMBER

