ORIGINAL.

MAP OF

"OAKDALE RESORT" ON LAKE GEORGE

PART of GOVT LOTS 3 and 4. SECTION 16. T.18.N.R.6.W. CLARE COUNTY MICHIGAN

July 11-1927

DESCRIPTION OF LAND PLATTED.

The Land embraced in the annexed plat of "Oakdale Resort" on Lake George being on and part of Govt. Lots 3 and 4 Section 16 T.18.N.R.6W. Clare County Michigan. is described as follows. Comencing at Meander Corner at the S.W. Corner of Govt. Lot 4 Section 16. T.18.N.R.6.W. Clare County Michigan. Proceeding thence N 46° 30' W. 274 ft. Thence N. 15° 30' W. 352 ft. Thence N. 68° 30' W. 450 ft. Thence N. 16° 30' W. 615 ft. Thence N. 2° 30' E 370 ft. Thence N. 35° W 143 ft. Thence N. 73° 45' W. 149.5 ft. Thence N. 3° E 194 ft. Thence N 27° E 360 ft. Thence N 21° W 265 ft. Thence N. 90° E 244 ft. Thence S. 42° E 770 ft. Thence S. 33° 30' E. 243 ft. Thence S. 2° E 1627 ft. Thence S. 8° 30' E 223 ft. to place of beginning. The entire plat being on and part of Govt. Lots 3 and 4.

State of Michigan, } ss.
County of Clare. }
Received for record the 12th day
of July A. D., 1927 at 1
o'clock P M., and recorded in Vol.
2 of Village Plats page 2
Emma Hoag
Register of Deeds.

I HEREBY CERTIFY, That there are no tax liens or titles held by the State on the lands described in this instrument and that there are no tax liens or titles held by individuals on the said lands, and that the taxes on said lands for the five years preceding the date of said instrument are all paid, as shown by the records of this office.

Harrison, Mich. June 27 1927

Fred W. Schaaf
County Treasurer

DEDICATION.

KNOW ALL MEN BY THESE PRESENTS. That we George Bilbrough as proprietor, and Ollie Bilbrough his wife, have caused the land embraced in the annexed plat to be surveyed, laid out and platted, to be known as "Oakdale Resort" on Lake George, Part of Govt Lots 3 and 4 Sec 16 T.18 N.R.6 W. Clare County Michigan, and that the streets and alleys as shown on said plat are hereby dedicated to the use of the public.

Signed and sealed in presence of.
Carl Beyer
Jessie Hadlock

George Bilbrough (L.S.)
Ollie Bilbrough (L.S.)

STATE OF MICHIGAN. } SS.
County of Mecosta }

On this Eighth day of June 1927 before me, a Notary Public in and for said County, personally came the above named George Bilbrough and Ollie Bilbrough his wife, known to me to be the persons who executed the above dedication, and acknowledged the same to be their free act and deed.

Notary Public
Notary Public in and for Mecosta Co., Mich.
My Commission Expires December 8th, 1929
My Commission Expires
Co. Michigan

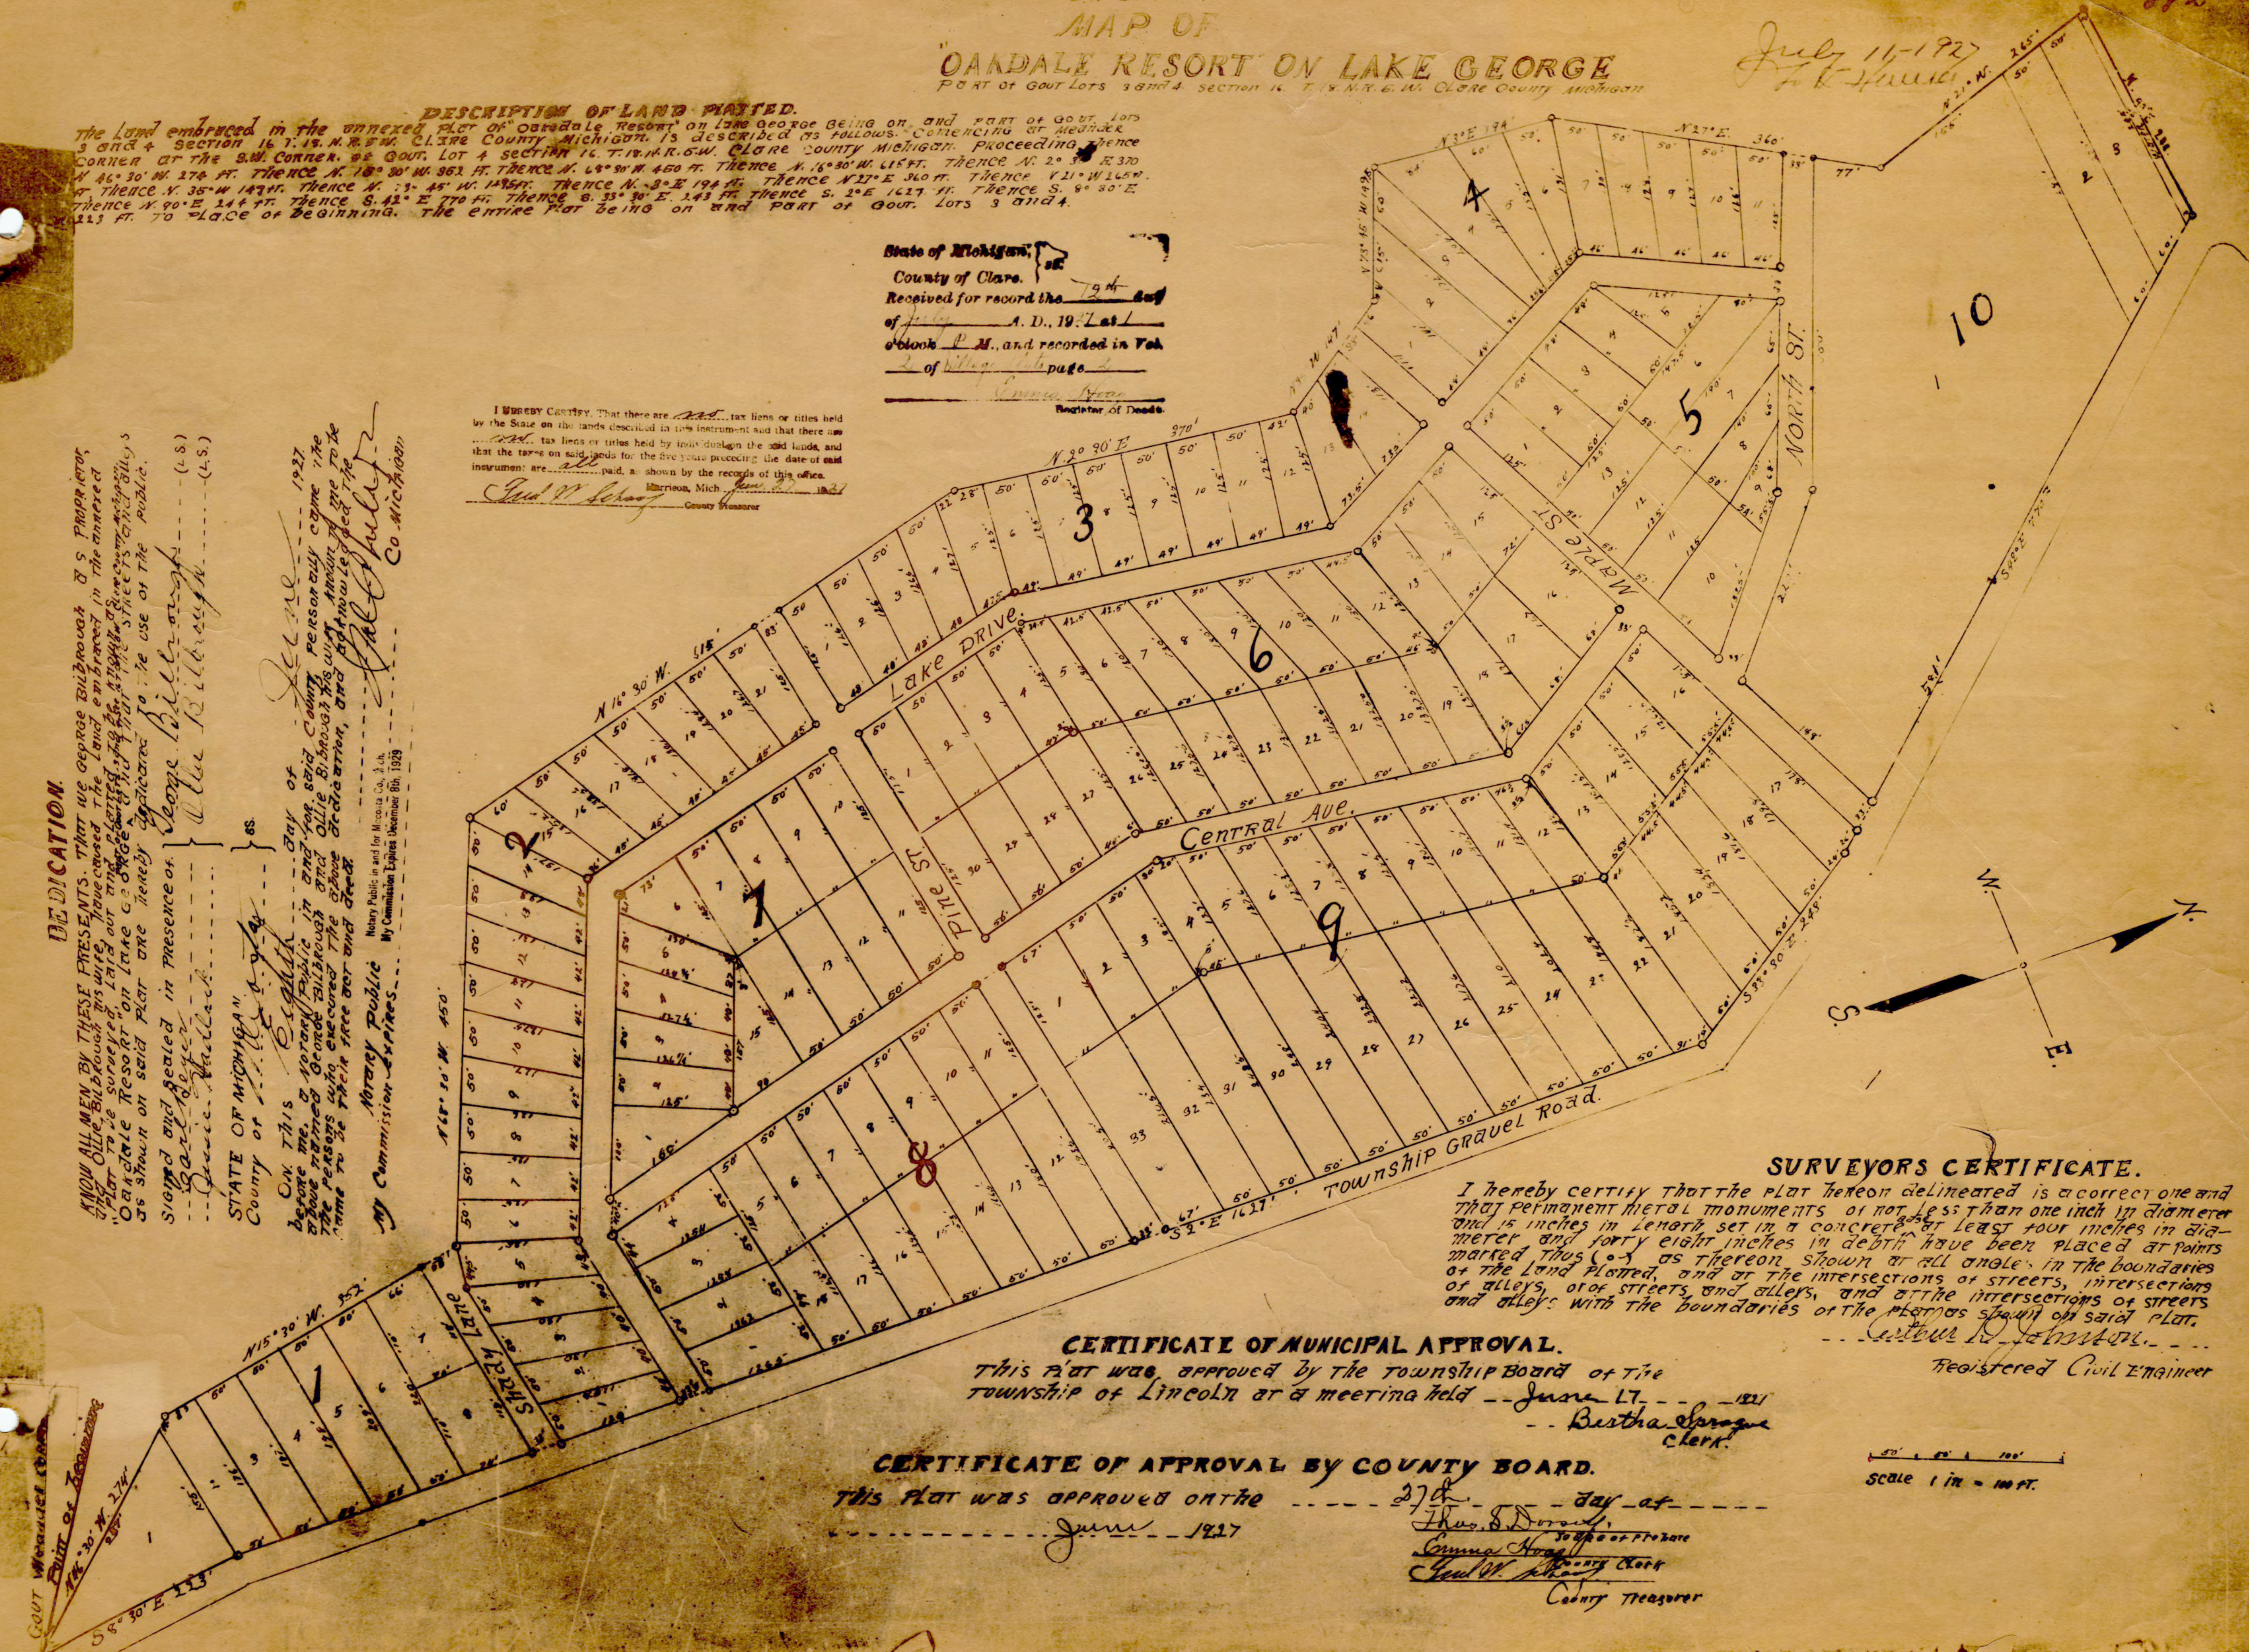

SURVEYORS CERTIFICATE.

I hereby certify that the plat hereon delineated is a correct one and that permanent metal monuments of not less than one inch in diameter and 15 inches in length set in a concrete base or at least four inches in diameter and forty eight inches in depth have been placed at points marked thus (o-) as thereon shown at all angles in the boundaries of the land platted, and at the intersections of streets, intersections of alleys, or of streets and alleys, and at the intersections of streets and alleys with the boundaries of the plat as shown on said plat.

Arthur B. Johnston
Registered Civil Engineer

CERTIFICATE OF MUNICIPAL APPROVAL.

This plat was approved by the Township Board of the Township of Lincoln at a meeting held -- June 17 --- 1927

Bertha Sprague
Clerk.

CERTIFICATE OF APPROVAL BY COUNTY BOARD.

This plat was approved on the 27th day of June 1927

Judge of Probate
Emma Hoag
County Clerk
Fred W. Schaaf
County Treasurer