
OCT 15 1953

Supervisor's Plat of Sherman's Subdivision.

COPY.

Part of the N.W.¼ of S.W.¼ of section 30. T.18.N.R.5.W (Lincoln T.W.P) Clare County Michigan.

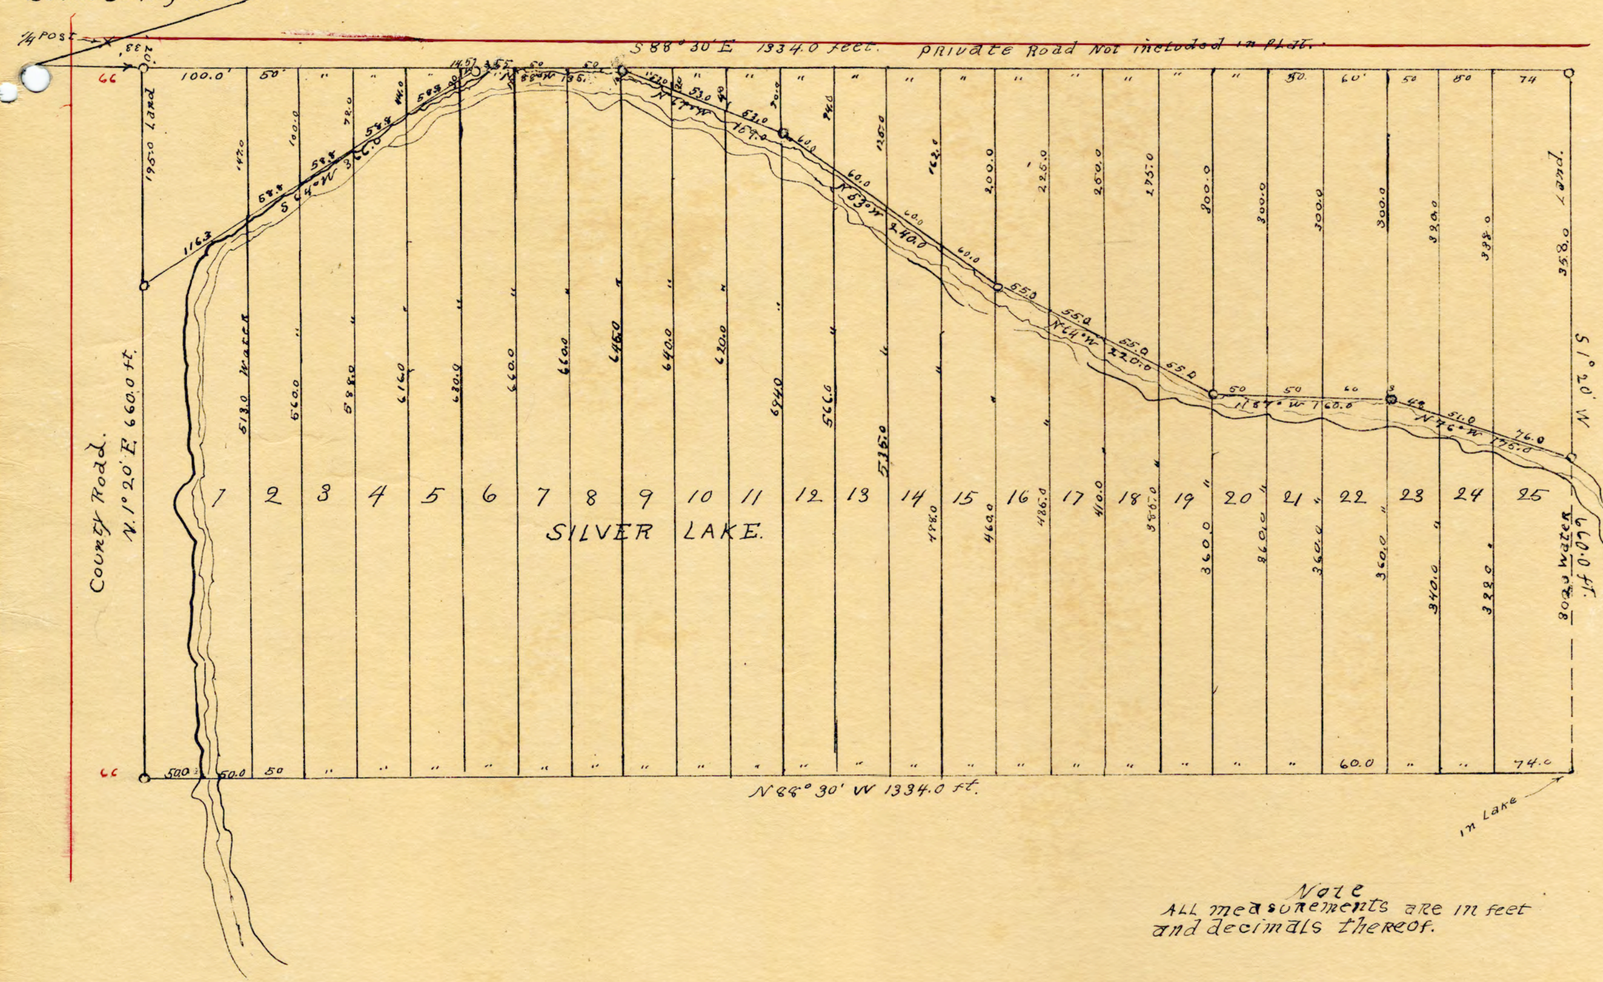

DESCRIPTION

The Land embraced in the annexed SUPERVISOR'S Plat of Sherman's subdivision, PART of the N.W.¼ of SW ¼ of section 30. T.18.N.R.5.W. (Lincoln T.W.P.) Clare County Michigan. is described as follows. Beginning at a point 33 feet East and 20 feet South of the ¼ section Corner on the West side of section 30. Running thence S. 88° 30' E. 1334 feet. thence S 1° 20' W 660 feet (360 ft Land and 300. ft water) thence N. 88° 30' W 1334 ft. thence N 1° 20' E. 660 feet to place of beginning This subdivision contains both Land and watter. as indicated on said Plat.

DEDICATION.

KNOW ALL MEN BY THESE PRESENTS, That I David Reed Supervisor of the Township of Lincoln of Clare County, state of Michigan, by virtue of authority in me vested by section 51, Act 173, of 1929, Having been duly authorised by the Lincoln Township Board have caused the Land and water described in the annexed plat to be surveyed, laid out and platted, to be known as "Supervisor's plat of Sherman's subdivision, PART of the N.W.¼ of S.W.¼ of section 30, T.18, N.R.5.W. (Lincoln T.W.P.) Clare County Michigan," And that the roads as shown on the margin of said plat are now being used for such purposes.

Witneses. Cecil Nubel
Frank Thilly

David Reed. David Reed
Supervisor of the Township of Lincoln

STATE OF MICHIGAN } ss.
County of Clare.

on this ... 13th ... day of August A.D. 1953 before me, a Notary public in and for said county, personally came the above named David Reed (Supervisor of Lincoln Township) known to me to be the person who executed the above dedication, and acknowledged the same to be his free act and deed as such, Supervisor.

Wm. A. Henderson
Notary public in and for Clare County
My commission expires July 9, 1957

APPROVAL BY BOARD OF COUNTY ROAD COMMISSIONERS.

This Plat has been examined and was approved on the ... 3rd ... day of Sept. ... 1953. By the Board of County Road Commissioners.

Ray Harold ... Ray Harold ... Chairman
Aury Barber ... Aury Barber ... Member
Ed Bruce ... Ed R Bruce ... Member.

MUNICIPAL APPROVAL.

This Plat was approved by the Township Board of Lincoln Township. at a meeting held August 12. 1953 (Date)

Frank Thilly
CLERK.

APPROVAL BY COUNTY BOARD.

This Plat was approved on the ... 8th ... day of ... September 1953 By the County Plat Board.

Wm A Henderson Wm. A. Henderson Register of Deeds
Wm A Henderson Wm. A. Henderson County Clerk
Peter A Oman Peter A. Oman County Treasurer
Bruce Williams Bruce Williams Co Drain Commissioner

Note
ALL measurements are in feet and decimals thereof.

Scale
100 50 1
1 inch = 100. feet.

SURVEYOR'S CERTIFICATE.

I hereby certify that the plat hereon delineated is a correct one and that permanent metal monuments Consting of bars not less than one half inch in diameter and 48 inches in length encased in a Concrete Cylinder at least 4 inches in diameter and 48 inches in depth have been placed at points marked thus (○) as thereon Shown at all angles in the boundaries of the Land and water Platted,

Arthur D Johnson Arthur D Johnson
Registered Land Surveyor.

COPY

Register's Office } ss.
Clare County,

Plat of Supervisors Plat of Shermans Subdivision Lincoln Twp.
was Recorded this 19th day of October A.D. 1953 at 8:30 O'clock A.M. in Liber 3 of Plats on Page 43

Village
Wm. A. Henderson
Register of Deeds

ORIGINAL ON FILE

I hereby certify that this copy is a true copy of the map or plat forwarded the Register of Deeds for recording.

Date October 15, 1953

Filed in Auditor General's Dept.
Date October 20, 1953

Examined and Approved
Date October 15, 1953

John B. McFall
AUDITOR GENERAL
By D. L. MacCoy
PLAT ENGINEER