

WHITE BIRCH LAKES OF CLARE NO. 5

Part of the S.E. 1/4 Sec. 27 & Part of the N.E. 1/4 Sec. 34 & Part of the W. 1/2 Sec. 35
Lincoln Twp., T18N, R5W, Clare Co., State of Michigan.

0 50' 100' 200' 300' 400'
SCALE: 1" = 100'

LEGEND :
1. ALL DIMENSIONS ARE IN FEET.
2. CONCRETE MONUMENTS HAVE BEEN PLACED AT ALL POINTS MARKED "O".
3. LOT CORNERS HAVE BEEN MARKED WITH 1/2" IRON BARS 18" IN LENGTH.
4. BEARINGS WERE ESTABLISHED FROM SOLAR OBSERVATIONS.
5. CURVE DIMENSIONS ARE ARC LENGTHS.

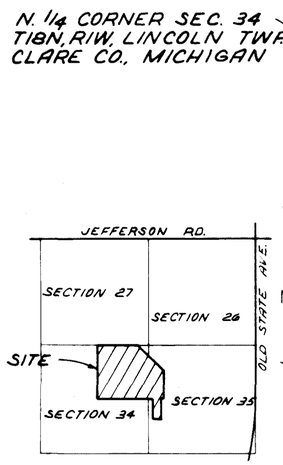

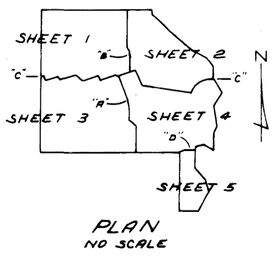

UNPLATTED

UNPLATTED

N. 1/4 CORNER SEC. 34
T18N, R5W, LINCOLN TWP.
CLARE CO., MICHIGAN

N00°22'44"W 33.00'
N 89°37'16"E 330.00'
330.00'

N 1/4 LINE SEC. 34

N89°37'16"E 2301.06'

N SECTION 34 LAUREL LANE (PRIVATE)

N89°37'16"E 640.00'

S00°22'44"E 103.78'

N89°37'16"E 2300.62'

N89°37'16"E 1025.00'

"B"

"C"

MATCH LINE "B" (SEE SHEET 2)

MATCH LINE "C" (SEE SHEET 4)

MATCH LINE "C" (SEE SHEET 3)

885 886 887 888 889 890 891 892 893 894 895 896

849 850 851 852 853 854 855 856 857 858 859 860 861

875 876 877 878 879 880 881 882 883 884

776 777 778 779 780 781 782 775 812 813 814 815

ELKHORN WAY

CHERRY HEMLOCK LANE (60' PRIVATE)

ROAD (60' PRIVATE)

10' PUBLIC UTILITY EASEMENT

SHEET 1 OF 6

WHITE BIRCH LAKES OF CLARE NO. 5

Part of the S.E. 1/4 Sec. 27 & Part of the N.E. 1/4 Sec. 34
& Part of the W 1/2 Sec. 35 Lincoln Twp., T18N, R5W,
Clare Co., State of Michigan

SCALE: 1"=100'

PLACE OF BEGINNING:
N.E. CORNER SEC. 34
T18N, R1W, LINCOLN TWP.
CLARE CO., MICHIGAN

WHITE BIRCH LAKES OF CLARE NO. 3

PLAN
NO SCALE

LOCATION SKETCH
NO SCALE


LEGEND:
1. ALL DIMENSIONS ARE IN FEET.
2. CONCRETE MONUMENTS HAVE BEEN PLACED AT ALL POINTS MARKED "O".
3. LOT CORNERS HAVE BEEN MARKED WITH 1/2" IRON BARS 18" IN LENGTH.
4. BEARINGS WERE ESTABLISHED FROM SOLAR OBSERVATIONS.
5. CURVE DIMENSIONS ARE ARC LENGTHS.

WHITE BIRCH LAKES OF CLARE NO. 5

Part of the S.E. 1/4 Sec. 27 & Part of the N.E. 1/4 Sec. 34 & Part of the W. 1/2 Sec. 35,
Lincoln Twp., T18N, R5W, Clare Co., State of Michigan.

LEGEND :
1. ALL DIMENSIONS ARE IN FEET.
2. CONCRETE MONUMENTS HAVE BEEN PLACED AT ALL POINTS MARKED "O".
3. LOT CORNERS HAVE BEEN MARKED WITH 1/2" IRON BARS 18" IN LENGTH.
4. BEARINGS WERE ESTABLISHED FROM SOLAR OBSERVATIONS.
5. CURVE DIMENSIONS ARE ARC LENGTHS.

0 50' 100' 200' 300' 400'
SCALE: 1" = 100'

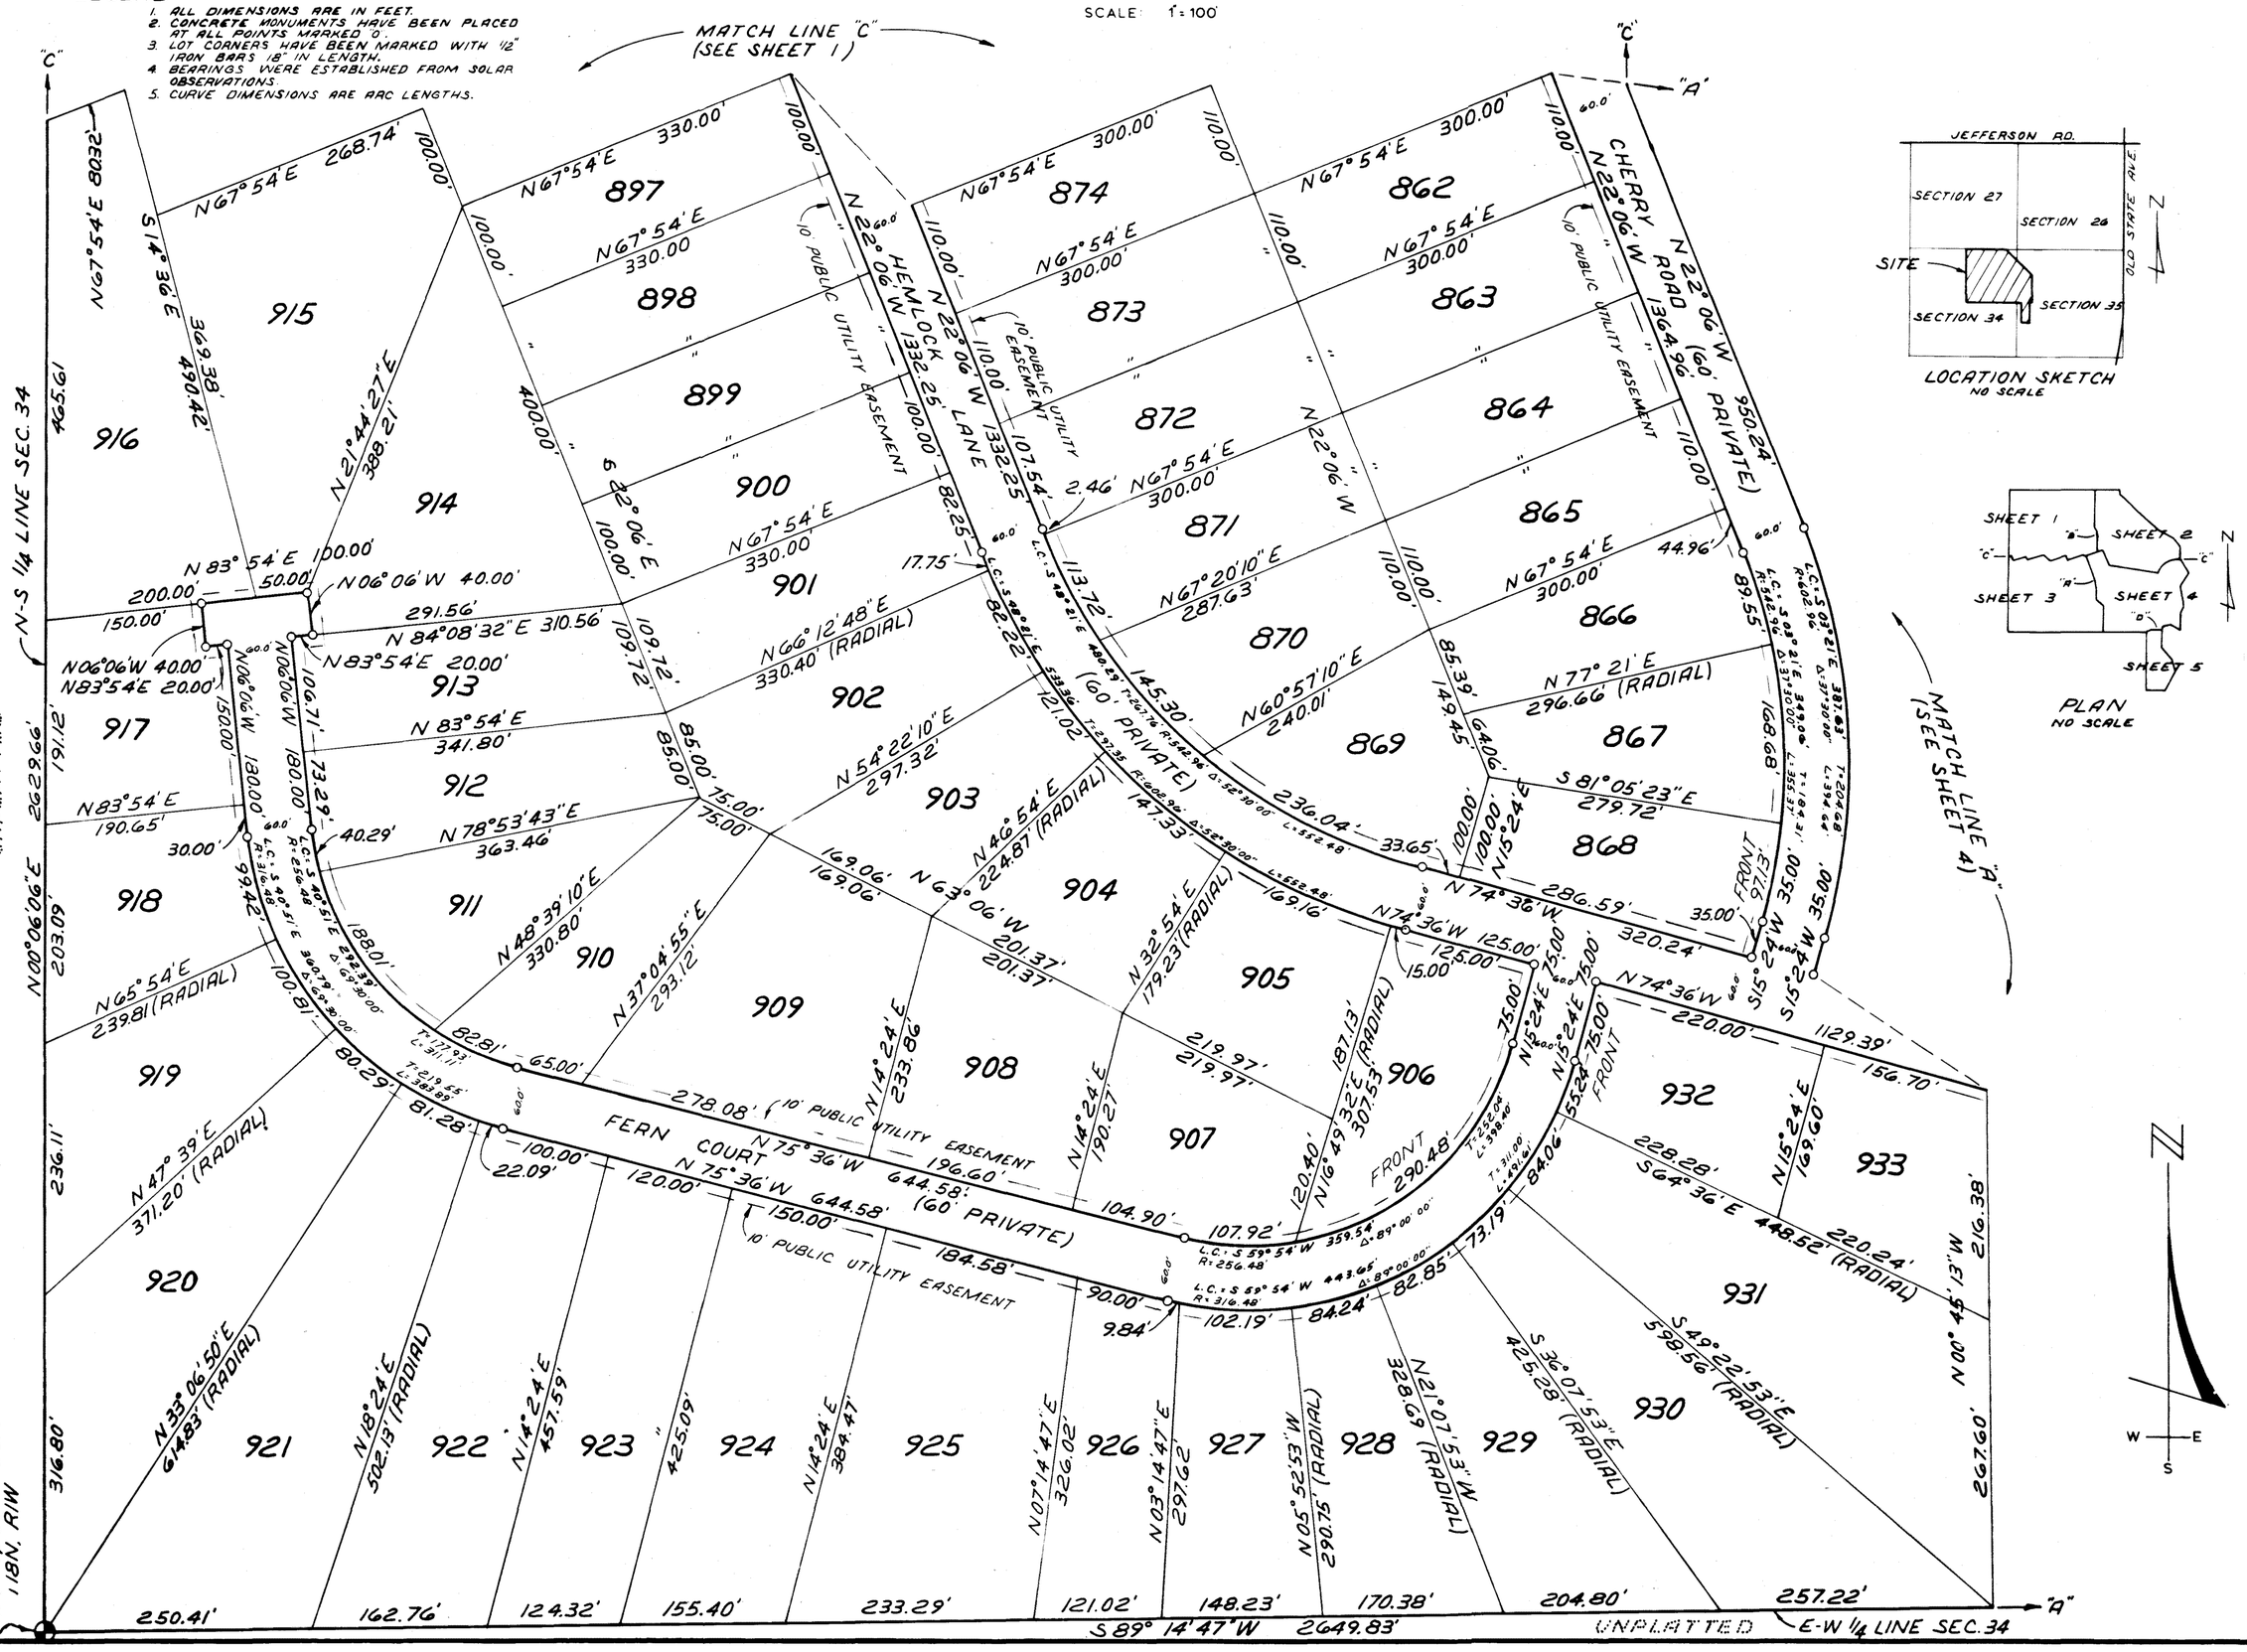

LOCATION SKETCH
NO SCALE

PLAN
NO SCALE

MATCH LINE "A" (SEE SHEET 4)

WHITE BIRCH LAKES OF CLARE NO. 5

Part of the S.E. 1/4 Sec. 27 & Part of the N.E. 1/4 Sec. 34 & Part of the W. 1/2 Sec. 35, Lincoln Twp., T18N, R5W, Clare Co., State of Michigan.

SCALE: 1" = 100'

LEGEND :
1. ALL DIMENSIONS ARE IN FEET.
2. CONCRETE MONUMENTS HAVE BEEN PLACED AT ALL POINTS MARKED "O".
3. LOT CORNERS HAVE BEEN MARKED WITH 1/2" IRON BARS 18" IN LENGTH.
4. BEARINGS WERE ESTABLISHED FROM SOLAR OBSERVATIONS
5. CURVE DIMENSIONS ARE RAC LENGTHS.

PLAN
NO SCALE

LOCATION SKETCH
NO SCALE

SHEET 4 OF 6

WHITE BIRCH LAKES OF CLARE NO. 5


Part of the S.E. 1/4 Sec. 27 & Part of the N.E. 1/4 Sec. 34 & Part of the W. 1/2 Sec. 35, Lincoln Twp., T18N, R5W, Clare Co., State of Michigan.

0 50 100 200 300 400

SCALE: 1" = 100'

LEGEND :

1. ALL DIMENSIONS ARE IN FEET.
2. CONCRETE MONUMENTS HAVE BEEN PLACED AT ALL POINTS MARKED "O".
3. LOT CORNERS HAVE BEEN MARKED WITH 1/2" IRON BARS 18" IN LENGTH.
4. BEARINGS WERE ESTABLISHED FROM SOLAR OBSERVATIONS.
5. CURVE DIMENSIONS ARE ARC LENGTHS.

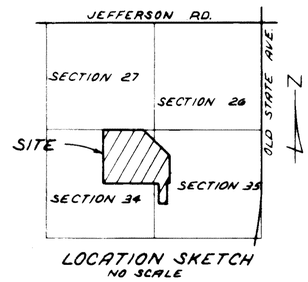

LOCATION SKETCH
NO SCALE

SURVEYOR'S CERTIFICATE

I, PAUL B. LAPHAM, SURVEYOR, CERTIFY:

THAT I HAVE SURVEYED, DIVIDED AND MAPPED THE LAND SHOWN ON THIS PLAT, DESCRIBED AS FOLLOWS: "WHITE BIRCH LAKES OF CLARE NO. 5, PART OF THE S.E. ¼ SEC. 27 & PART OF THE N.E. ¼ SEC. 34 & PART OF THE W ½ SEC. 35 LINCOLN TWP., T18N, R5W, CLARE CO., STATE OF MICHIGAN."; BEGINNING AT THE NORTHEAST CORNER OF SECTION 34, T18N, R1W, LINCOLN TOWNSHIP, CLARE COUNTY, MICHIGAN; THENCE, S 00° 18' 56" E, 33.00 FEET ALONG THE EAST LINE OF SECTION 34 AND THE WEST LINE OF WHITE BIRCH LAKES OF CLARE NO. 3; THENCE, S 89° 37' 16" W PARALLEL TO THE NORTH LINE OF SECTION 34, 515.58 FEET; THENCE, S 32° 24' 53" E, 160.32 FEET; THENCE, S 60° 23' E, 199.22 FEET; THENCE, S 46° 36' E, 356.60 FEET; THENCE, S 53° 06' E, 311.70 FEET; THENCE, S 64° 06' E, 480.65 FEET; THENCE, S 29° 36' E, 143.62 FEET; THENCE, S 07° 24' W, 235.00 FEET; THENCE, S 12° 09' 49" W, 60.21 FEET; THENCE, S 17° 06' E, 85.00 FEET; THENCE, S 34° 24' 12" E, 251.64 FEET; THENCE, S 46° 24' W, 271.42 FEET; THENCE, S 11° 36' E, 333.48 FEET; THENCE, S 31° 51' 35" W, 174.59 FEET; THENCE, S 02° 06' E, 316.67 FEET; THENCE, N 63° 05' 36" W, 198.63 FEET; THENCE, N 89° 38' 01" W, 175.00 FEET; THENCE, S 01° 38' 01" E, 396.60 FEET; THENCE, S 41° 38' 01" E, 267.24 FEET; THENCE, S 12° 38' 01" E, 330.04 FEET; THENCE, S 33° 51' 59" W, 333.88 FEET; THENCE, N 00° 21' 59" E PARALLEL TO THE EAST LINE OF SECTION 34, 1,086.76 FEET; THENCE, S 89° 14' 47" W, 20.00 FEET TO THE EAST ONE-QUARTER CORNER OF SAID SECTION 34; THENCE, S 89° 14' 47" W ALONG THE EAST-WEST ONE-QUARTER LINE OF SECTION 34, 2,649.83 FEET TO THE INTERIOR ONE-QUARTER CORNER OF SAID SECTION 34; THENCE, N 00° 06' 06" E ALONG THE NORTH-SOUTH ONE-QUARTER LINE OF SECTION 34, 2,629.66 FEET TO THE NORTH ONE-QUARTER CORNER OF SAID SECTION 34; THENCE, N 89° 37' 16" E ALONG THE NORTH LINE OF SECTION 34, 330.00 FEET; THENCE N 00° 22' 44" W, 33.00 FEET; THENCE, N 89° 37' 16" E, 2,301.06 FEET; THENCE, S 00° 23' W ALONG THE WEST LINE OF WHITE BIRCH LAKES OF CLARE NO. 3 AND THE EAST LINE OF SECTION 27, 33.00 FEET BACK TO THE PLACE OF BEGINNING. CONTAINING 195 LOTS.

THAT I HAVE MADE SUCH SURVEY, LAND-DIVISION AND PLAT BY THE DIRECTION OF THE OWNERS OF SUCH LAND.

THAT SUCH PLAT IS A CORRECT REPRESENTATION OF ALL EXTERIOR BOUNDARIES OF THE LAND SURVEYED AND THE SUBDIVISION OF IT.

THAT THE REQUIRED MONUMENTS AND LOT MARKERS HAVE BEEN LOCATED IN THE GROUND OR THAT SURETY HAS BEEN DEPOSITED WITH THE MUNICIPALITY, AS REQUIRED BY SECTION 125 OF THE ACT.

THAT THE ACCURACY OF SURVEY IS WITHIN THE LIMITS REQUIRED BY SECTION 126 OF THE ACT.

THAT THE BEARINGS SHOWN ON THE PLAT ARE EXPRESSED AS REQUIRED BY SECTION 126 (3) OF THE ACT AND AS EXPLAINED IN THE LEGEND.

December 1, 1971
DATE

PAUL B. LAPHAM & ASSOCIATES, INC.
631 WEST U.S. 10
CLARE, MICHIGAN 48617

Paul B. Lapham
PAUL B. LAPHAM, PRINCIPAL, R.L.S. NO. 9433

STATE OF MICHIGAN * PAUL B. LAPHAM LAND SURVEYOR No. 9433 * REGISTERED LAND SURVEYOR

COUNTY PLAT BOARD CERTIFICATE

THIS PLAT HAS BEEN REVIEWED AND IS APPROVED BY THE CLARE COUNTY PLAT BOARD ON February 29 1972 AS BEING IN COMPLIANCE WITH ALL OF THE PROVISIONS OF ACT 288, P.A. 1967, AND THE PLAT BOARD'S APPLICABLE RULES AND REGULATIONS.

Louis W. Becker
LOUIS W. BECKER
REGISTER OF DEEDS

Mark McKenna
MARK MC KENNA
CH. BOARD OF COUNTY COMM.


Ellen Ulch
ELLEN ULCH
TREASURER

COUNTY TREASURER'S CERTIFICATE

THE RECORDS IN MY OFFICE SHOW NO UNPAID TAXES OR SPECIAL ASSESSMENTS FOR THE FIVE YEARS PRECEDING December 14, 1971, INVOLVING THE LANDS INCLUDED IN THIS PLAT.

Clare
CLARE COUNTY

Ellen Ulch
ELLEN ULCH COUNTY TREASURER

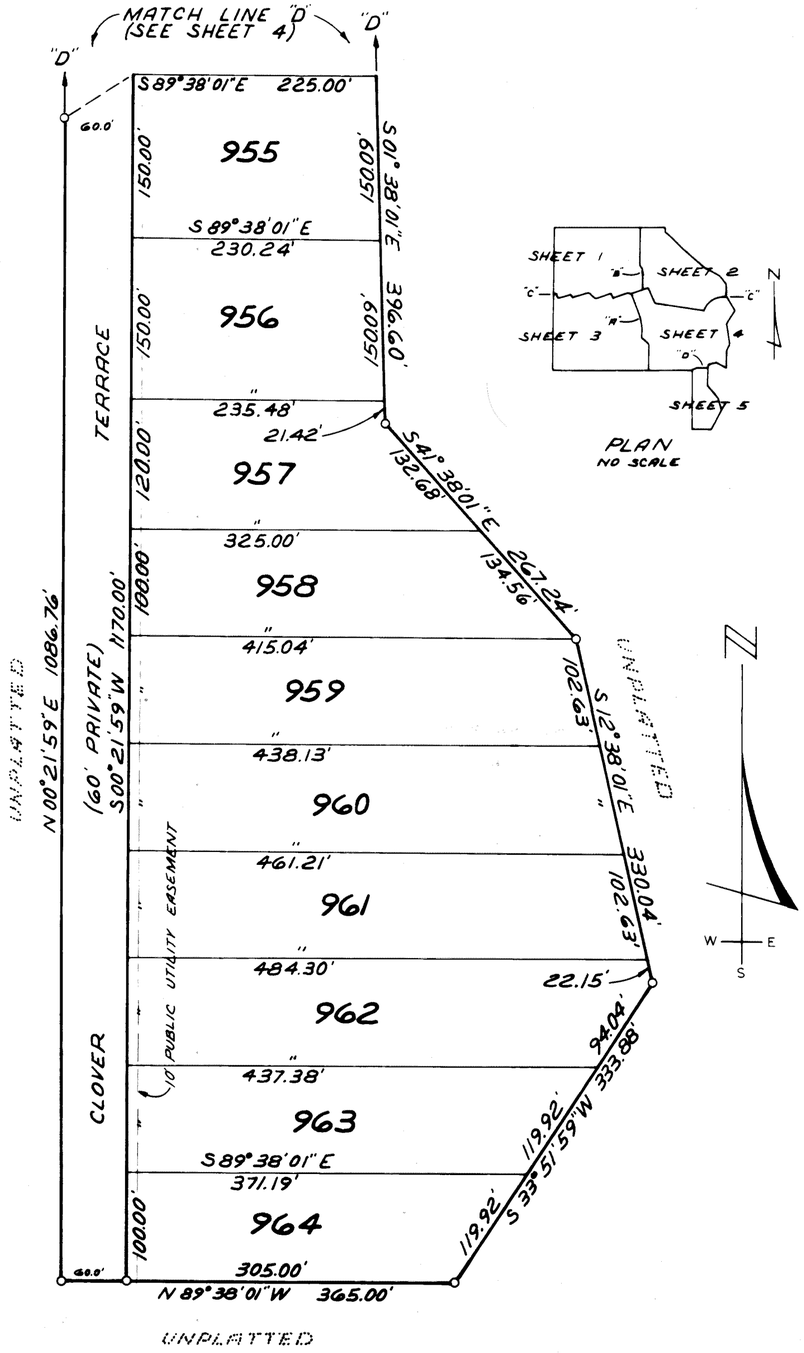

UNPLATTED

PLAN
NO SCALE

WHITE BIRCH LAKES OF CLARE NO. 5

Part of the S.E. 1/4 Sec. 27 & Part of the N.E. 1/4 Sec. 34 & Part of the W. 1/2 Sec. 35, Lincoln Twp., T18N, R5W, Clare Co., State of Michigan.

PROPRIETOR'S CERTIFICATE

NEULAND DEVELOPMENT, INC., AN ILLINOIS CORPORATION DULY ORGANIZED AND EXISTING UNDER THE LAWS OF THE STATE OF MICHIGAN BY RICHARD G. NEUMANN, PRESIDENT, AND JOHN J. MC INERNEY, SECRETARY, AS PROPRIETOR, HAS CAUSED THE LAND TO BE SURVEYED, DIVIDED, MAPPED AND DEDICATED AS REPRESENTED ON THIS PLAT AND THAT LAUREL LANE, ELKHORN WAY, HEMLOCK LANE, DEER COURT, FERN COURT, CHERRY ROAD AND CLOVER TERRACE ARE PRIVATE, DEDICATED ONLY TO THE USE OF THE LOT OWNERS, INCLUDING LOT OWNERS IN CONTIGUOUS SUBDIVISIONS: THAT THE PUBLIC UTILITY EASEMENTS ARE PRIVATE EASEMENTS AND THAT ALL OTHER EASEMENTS ARE FOR THE USES SHOWN ON THE PLAT.

NEULAND DEVELOPMENT, INC.
212 BAUER ROAD
NAPERVILLE, ILLINOIS 60540

WITNESSES:
Edgar F. Neumann
EDGAR F. NEUMANN

Richard G. Neumann
RICHARD G. NEUMANN — PRESIDENT

Mary A. Hayden
MARY A. HAYDEN

John J. Mc Inerney
JOHN J. MC INERNEY — SECRETARY

ACKNOWLEDGEMENT

STATE OF MICHIGAN)
COUNTY OF CLARE) SS.

PERSONALLY CAME BEFORE ME THIS 7 DAY OF DECEMBER, 1971, RICHARD G. NEUMANN, PRESIDENT, AND JOHN J. MC INERNEY, SECRETARY, OF THE ABOVE NAMED CORPORATION, TO ME KNOWN TO BE THE PERSONS WHO EXECUTED THE FOREGOING INSTRUMENT, AND TO ME KNOWN TO BE SUCH PRESIDENT AND SECRETARY OF SAID CORPORATION, AND ACKNOWLEDGED THAT THEY EXECUTED THE FOREGOING INSTRUMENT AS SUCH OFFICERS AS THE FREE ACT AND DEED OF SAID CORPORATION, BY ITS AUTHORITY.

NOTARY PUBLIC, Alan A. Dale (ALAN A. DALE), CLARE COUNTY, MICHIGAN.

MY COMMISSION EXPIRES SEPT. 9 - 1975.

PROPRIETOR'S CERTIFICATE

FIRST MORTGAGE INVESTORS, A MASSACHUSETTS BUSINESS TRUST, BY CARL N. BRETT AS SUBSTITUTE NOMINEE OF THE TRUSTEES OF FIRST MORTGAGE INVESTORS, AS PROPRIETOR, HAS CAUSED THE LAND TO BE SURVEYED, DIVIDED, MAPPED AND DEDICATED AS REPRESENTED ON THIS PLAT AND THAT LAUREL LANE, ELKHORN WAY, HEMLOCK LANE, DEER COURT, FERN COURT, CHERRY ROAD AND CLOVER TERRACE ARE PRIVATE, DEDICATED ONLY TO THE USE OF THE LOT OWNERS, INCLUDING LOT OWNERS IN CONTIGUOUS SUBDIVISIONS; THAT THE PUBLIC UTILITY EASEMENTS ARE PRIVATE EASEMENTS AND THAT ALL OTHER EASEMENTS ARE FOR THE USES SHOWN ON THE PLAT.

FIRST MORTGAGE INVESTORS
A MASSACHUSETTS BUSINESS TRUST
801 41ST STREET
MIAMI BEACH, FLORIDA 33140

WITNESSES:
Robert M. Landis
Robert M. Landis
Mary Ann Torano
Mary Ann Torano

CARL N. BRETT, AS SUBSTITUTE NOMINEE OF THE TRUSTEES OF FIRST MORTGAGE INVESTORS A MASSACHUSETTS BUSINESS TRUST

FIRST MORTGAGE INVESTORS COMMON SEAL -1961- MASSACHUSETTS TRUST

ACKNOWLEDGEMENT

STATE OF Florida)
COUNTY OF Dade) SS.

PERSONALLY CAME BEFORE ME THIS 7th DAY OF December, 1971, CARL N. BRETT, SUBSTITUTE NOMINEE OF THE TRUSTEES OF FIRST MORTGAGE INVESTORS, OF THE ABOVE NAMED TRUST, TO ME KNOWN TO BE THE PERSON WHO EXECUTED THE FOREGOING INSTRUMENT, AND TO ME KNOWN TO BE SUCH NOMINEE OF THE TRUSTEES OF SAID TRUST, AND ACKNOWLEDGED THAT HE EXECUTED THE FOREGOING INSTRUMENT AS SUCH OFFICER AS THE FREE ACT AND DEED OF SAID TRUST BY ITS AUTHORITY.

NOTARY PUBLIC Bonnie D Clayton (Bonnie D. Clayton), State of Florida at Large.

MY COMMISSION EXPIRES March 2, 1973.

BONNIE D. CLAYTON NOTARY PUBLIC STATE OF FLORIDA AT LARGE

RECORDING CERTIFICATE

STATE OF MICHIGAN)
COUNTY OF CLARE)

THIS PLAT WAS RECEIVED FOR RECORD ON THE 28 DAY OF April, 1972, AT 11:00 A.M., AND RECORDED IN LIBER 13 OF PLATS ON PAGES 18-23.

Louis W. Becker
LOUIS W. BECKER
REGISTER OF DEEDS

COUNTY DRAIN COMMISSIONER'S CERTIFICATE

APPROVED ON Dec 14, 1971 AS COMPLYING WITH SECTION 192 OF ACT 288, P.A. 1967, AND THE APPLICABLE RULES AND REGULATIONS PUBLISHED BY MY OFFICE IN THE COUNTY OF CLARE.

Walter Ehle
WALTER EHLE — DRAIN COMMISSIONER

CERTIFICATE OF COUNTY ROAD COMMISSIONERS

APPROVED ON December 15, 1971, AS COMPLYING WITH SECTION 183 OF ACT 288, P.A. 1967, AND THE APPLICABLE PUBLISHED RULES AND REGULATIONS OF THE BOARD OF ROAD COMMISSIONERS OF CLARE COUNTY.

Wm Hileman — WM. HILEMAN — CHAIRMAN
GLENN LLOYD — MEMBER
Fred L. Jones — FRED L. JONES — MEMBER

CERTIFICATE OF MUNICIPAL APPROVAL

I CERTIFY THAT THIS PLAT WAS APPROVED BY THE TOWNSHIP BOARD OF LINCOLN, AT A MEETING HELD ON June 16, 1972 AND WAS REVIEWED AND FOUND TO BE IN COMPLIANCE WITH ACT 288, P.A. OF 1967. THIS PLAT WAS APPROVED BY THE CLARE COUNTY HEALTH DEPARTMENT ON 11-24-71. SURETY HAS BEEN POSTED FOR THE PLACEMENT OF MONUMENTS WITH SUCH PLACEMENT TO BE COMPLETED BEFORE January 1, 1973.

Margaret Mc George
MARGAREY MC GEORGE — CLERK

Certified true copy of recorded plat.
Allison Green
ALLISON GREEN
STATE TREASURER
By Richard E. Lonas
Richard E. Lonas Plat Examiner
Date May 16, 1972