8/9/51

COPY

Register's Office } ss.
Clare County.

Plat of The first Addition to Woodmere Lincoln Township

was Recorded this 16th day of August A.D., 1951 at 9:30 O'clock A M. in Liber 3 of Village Plat on Page 17

Wm. A. Henderson
Register of Deeds

ORIGINAL ON FILE


# Plat of The first Addition to "WOODMERE"

## Being all of Lot 1 Section 16 T.18 N.R. 5W. (Lincoln Township) Clare County, State of Michigan.

State of Michigan )
} ss.
County of Clare )

On this 3rd day of June 1951 before me, a Notary Public in and for said county, personally came the above named George A. Blake and Edna M. Blake, his wife, known to me to be the persons who executed the above dedication, and acknowledged the same to be their free act and deed.

T. O. Bissell
Notary Public, Clare Co., Mich.
My comm exp: Jan 22 - 1954

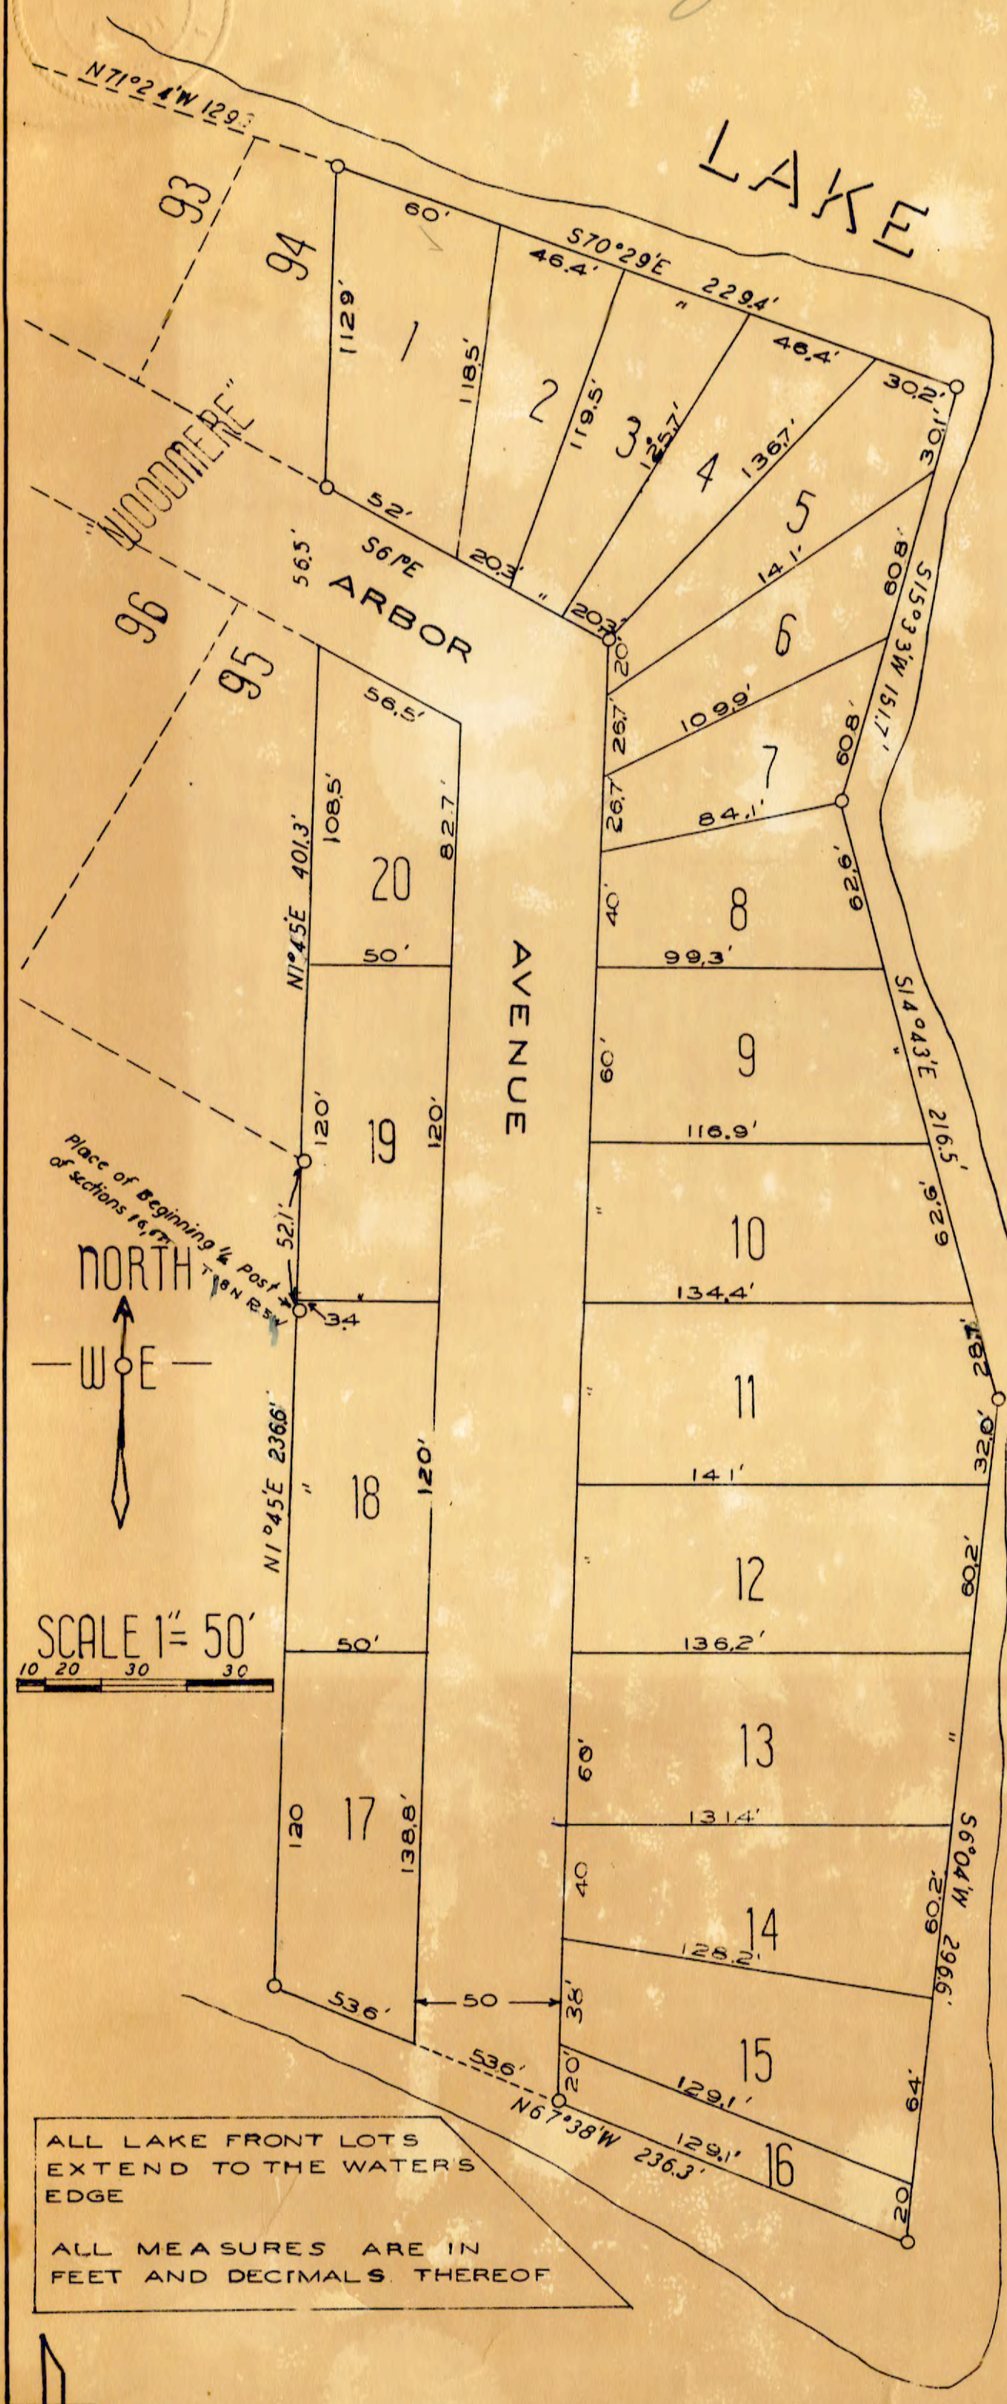


ALL LAKE FRONT LOTS EXTEND TO THE WATER'S EDGE

ALL MEASURES ARE IN FEET AND DECIMALS THEREOF

### DEDICATION

George A. Blake and Edna M. Blake, his wife, owners of the mineral rights, and

KNOW ALL MEN BY THESE PRESENTS? That we, A. Lee Swallow, as proprietor, and Margaret I. Swallow, his wife, have caused the land embraced in the annexed plat to be surveyed, laid out and platted, to be known as The First Addition to "Woodmere" being all of Lot 1, Section 16, T18N, R5W, Lincoln Township, Clare County, Michigan, and that the streets and alleys as shown on said plat are hereby dedicated to the use of the public.

Signed and Sealed in Presence of

A. Lee Swallow (L.S.)

L. R. Shear

Margaret I. Swallow (L.S.)

F. S. Killoran

George A. Blake (L.S.)

Edna M. Blake (L.S.)

STATE OF MICHIGAN, } ss.
County of Clare }

On this 18th day of July 1951 before me, a Notary Public in and for said county, personally came the above named A. Lee Swallow and Margaret I. Swallow, his wife, known to me to be the persons who executed the above dedication, and acknowledged the same to be their free act and deed.

L. R. Shear
Notary Public Clare Co., Mich.
L. R. Shear

My Commission expires May 15, 1955

### DESCRIPTION OF LAND PLATTED.

The land embraced in the annexed plat of The first Addition to "Woodmere" being all of Lot 1, Section 16, T18N, R5W, Lincoln Township, Clare County, State of Michigan, is described as follows:
Beginning at the ¼ post of Sections 16 and 17, T18N, R5W, (Lincoln Twp.) thence N. 1°45' E. 401.3 feet, thence S. 70°29' E. 229.4 feet, thence S15°33' W. 151.7 feet, thence 14°43' E. 216.5 feet, thence S. 6°04' W. 296.6 feet, thence N. 67°38' W. 236.3 feet, thence N 1°45' E. 236.6 feet to the place of beginning.

### SURVEYOR'S CERTIFICATE

I hereby certify that the plat hereon delineated is a correct one and that permanent metal monuments consisting of bars not less than one-half inch in diameter and 48 inches in length, or shorter bars of not less than one-half inch in diameter lapped over each other at least 6 inches with an over-all length of not less than 48 inches, encased in a concrete cylinder at least 4 inches in diameter and 48 inches in depth have been placed at points marked thus (O) as thereon shown at all angles in the boundaries of the land platted, at all the intersections of streets, intersections of alleys, or of streets and alleys, and at the intersections of streets and alleys with the boundaries of the plat as shown on said plat.

Frank McClung
Frank McClung
Registered Land Surveyor

### CERTIFICATE OF APPROVAL BY BOARD OF COUNTY ROAD COMMISSIONERS

This plat has been examined and was approved on the 3rd day of August 1951 by the Clare County Board of Road Commissioners.

I HEREBY CERTIFY THAT THIS COPY IS A TRUE COPY OF THE MAP OR PLAT FORWARDED THE REGISTER OF DEEDS FOR RECORDING.

COMPARED August 9, 1951
DEPUTY AUDITOR GENERAL
Mayme Jewell Purdy

Lear Diment
Lear Diment Chairman.

Ray Harrold
Ray Harrold Member.

Avery Barber
Avery Barber Member.

### CERTIFICATE OF MUNICIPAL APPROVAL

This plat was approved by the Township Board of the Township of Lincoln at a meeting held July 27 - 1951.

David Reed
David Reed Clerk.

### CERTIFICATE OF APPROVAL BY COUNTY BOARD

This plat was approved on the 3rd day of August 1951 by the Clare County Plat Board.

Wm. A. Henderson
Wm. A. Henderson Register of Deeds.

Wm. A. Henderson
Wm. A. Henderson County Clerk.

Peter A. Oman
Peter A. Oman County Treasurer

FILED IN AUDITOR GENERAL'S DEPT.
August 27, 1951
DEPUTY AUDITOR GENERAL
Mayme Jewell Purdy

### COUNTY TREASURER'S CERTIFICATE RELATING TO TAXES

(Sec. 135, Act 206, 1893, as amended--Sec. 4134, C. L. 1915.)
Office of County Treasurer, Clare County.

I hereby certify, That there are no tax liens or titles held by the State on the lands described hereon, and that there are no tax liens or titles held by individuals on said lands, for the five years preceding the 3rd day of Aug. 1951 and that the taxes for said period of five years are all paid, as shown by the records of this office.
This certificate does not apply to taxes, if any, now in process of collection by township, city or village collecting officers.

Peter A. Oman
Peter A. Oman County Treasurer.

Examined and Approved
August 9, 1951
Deputy Auditor General
Mayme Jewell Purdy